


WELD STP

WELD ALL

OVERALL HEIGHT = 221

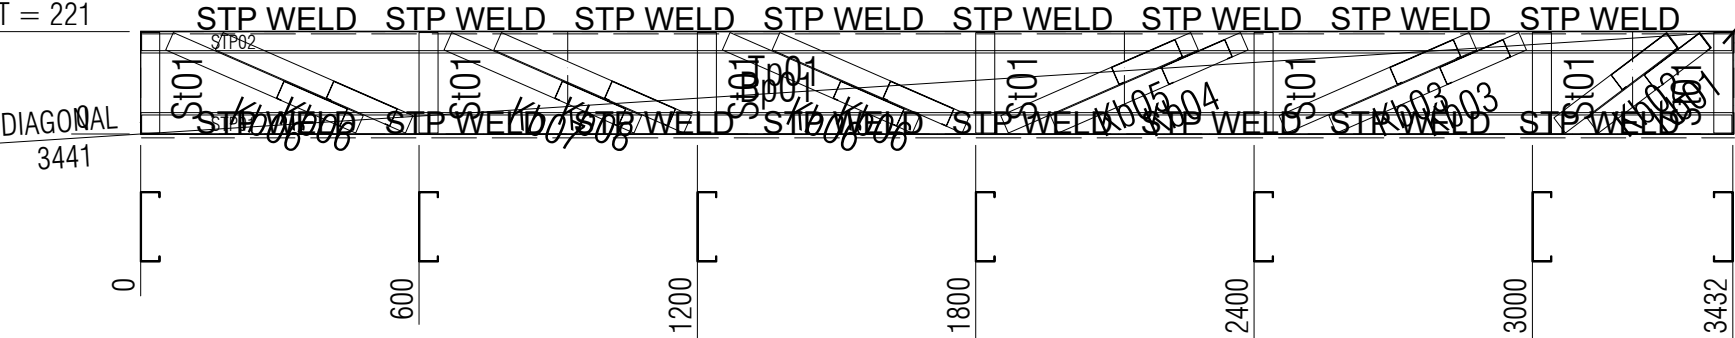

FRAME STICKS				
NAME	LENGTH	WT	QTY	PROFILE
Tp01	3428	6.3	1	150S41-950-500
Bp01	3428	6.3	1	150S41-950-500
St01	217	0.4	7	150S41-950-500
Kb01	305	0.6	1	150S41-950-500
Kb02	305	0.6	1	150S41-950-500
Kb03	447	0.8	2	150S41-950-500
Kb04	447	0.8	1	150S41-950-500
Kb05	447	0.8	1	150S41-950-500
Kb06	447	0.8	4	150S41-950-500
Kb07	447	0.8	1	150S41-950-500
Kb08	447	0.8	1	150S41-950-500
TOTAL	13452	24.8	21	

STEEL SUPPORT MEMBERS				
NAME	PROFILE	LENGTH	WT	QTY
STP01	152U47_095_550	3434	4.4	1
STP02	152U47_095_550	3434	4.4	1
TOTAL			8.8	2

BE3000



DELIVERING SINCE 2003

DRAWN: N.N

PH: 02 4860 1416
OFFICE: 02 4860 1400

REV	DATE	REASON
A	15/09/26	IFC — Issued for construction

AUSTRUSS PROJECT NAME
CALDERWOOD

AUSTRUSS ZONE NUMBER
A3

CLIENT NAME
ADCO

PROJECT ADDRESS
179 CALDERWOOD ROAD
CALDERWOOD NSW 2527

AUSTRUSS PROJECT NUMBER
25363

DRAWING NAME
150 - PANELS

DRAWING NUMBER
LGS-A3-200

REV
A




SCAN FOR 3D


WELD STP

WELD ALL

OVERALL HEIGHT = 221

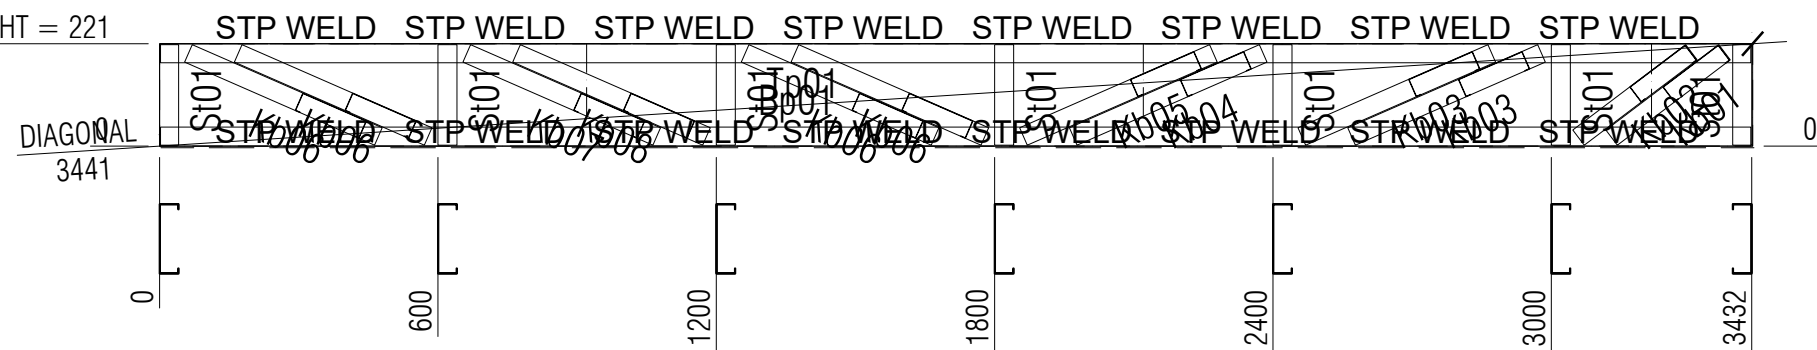

FRAME STICKS				
NAME	LENGTH	WT	QTY	PROFILE
Tp01	3428	6.3	1	150S41-950-500
Bp01	3428	6.3	1	150S41-950-500
St01	217	0.4	7	150S41-950-500
Kb01	305	0.6	1	150S41-950-500
Kb02	305	0.6	1	150S41-950-500
Kb03	447	0.8	2	150S41-950-500
Kb04	447	0.8	1	150S41-950-500
Kb05	447	0.8	1	150S41-950-500
Kb06	447	0.8	4	150S41-950-500
Kb07	447	0.8	1	150S41-950-500
Kb08	447	0.8	1	150S41-950-500
TOTAL	13452	24.8	21	

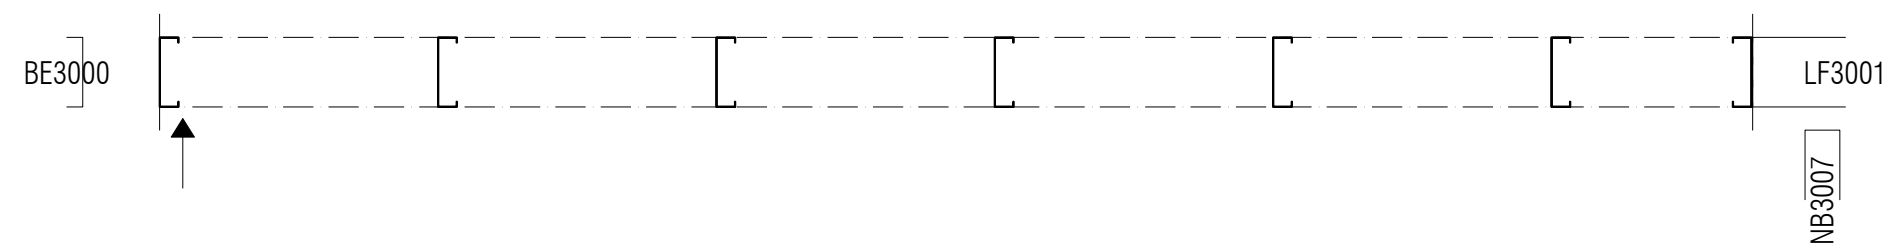

BE3001

AUSTRUSS

DELIVERING SINCE 2003

DRAWN: N.N

PH: 02 4860 1416
OFFICE: 02 4860 1400

REV	DATE	REASON
A	15/09/26	IFC — Issued for construction

AUSTRUSS PROJECT NAME

CALDERWOOD

AUSTRUSS ZONE NUMBER

A3

CLIENT NAME

ADCO

PROJECT ADDRESS

179 CALDERWOOD ROAD
CALDERWOOD NSW 2527

AUSTRUSS PROJECT NUMBER

25363

DRAWING NAME

150 - PANELS

DRAWING NUMBER

LGS-A3-200


REV

A

SCAN FOR 3D

WELD ALL

OVERALL HEIGHT = 1480

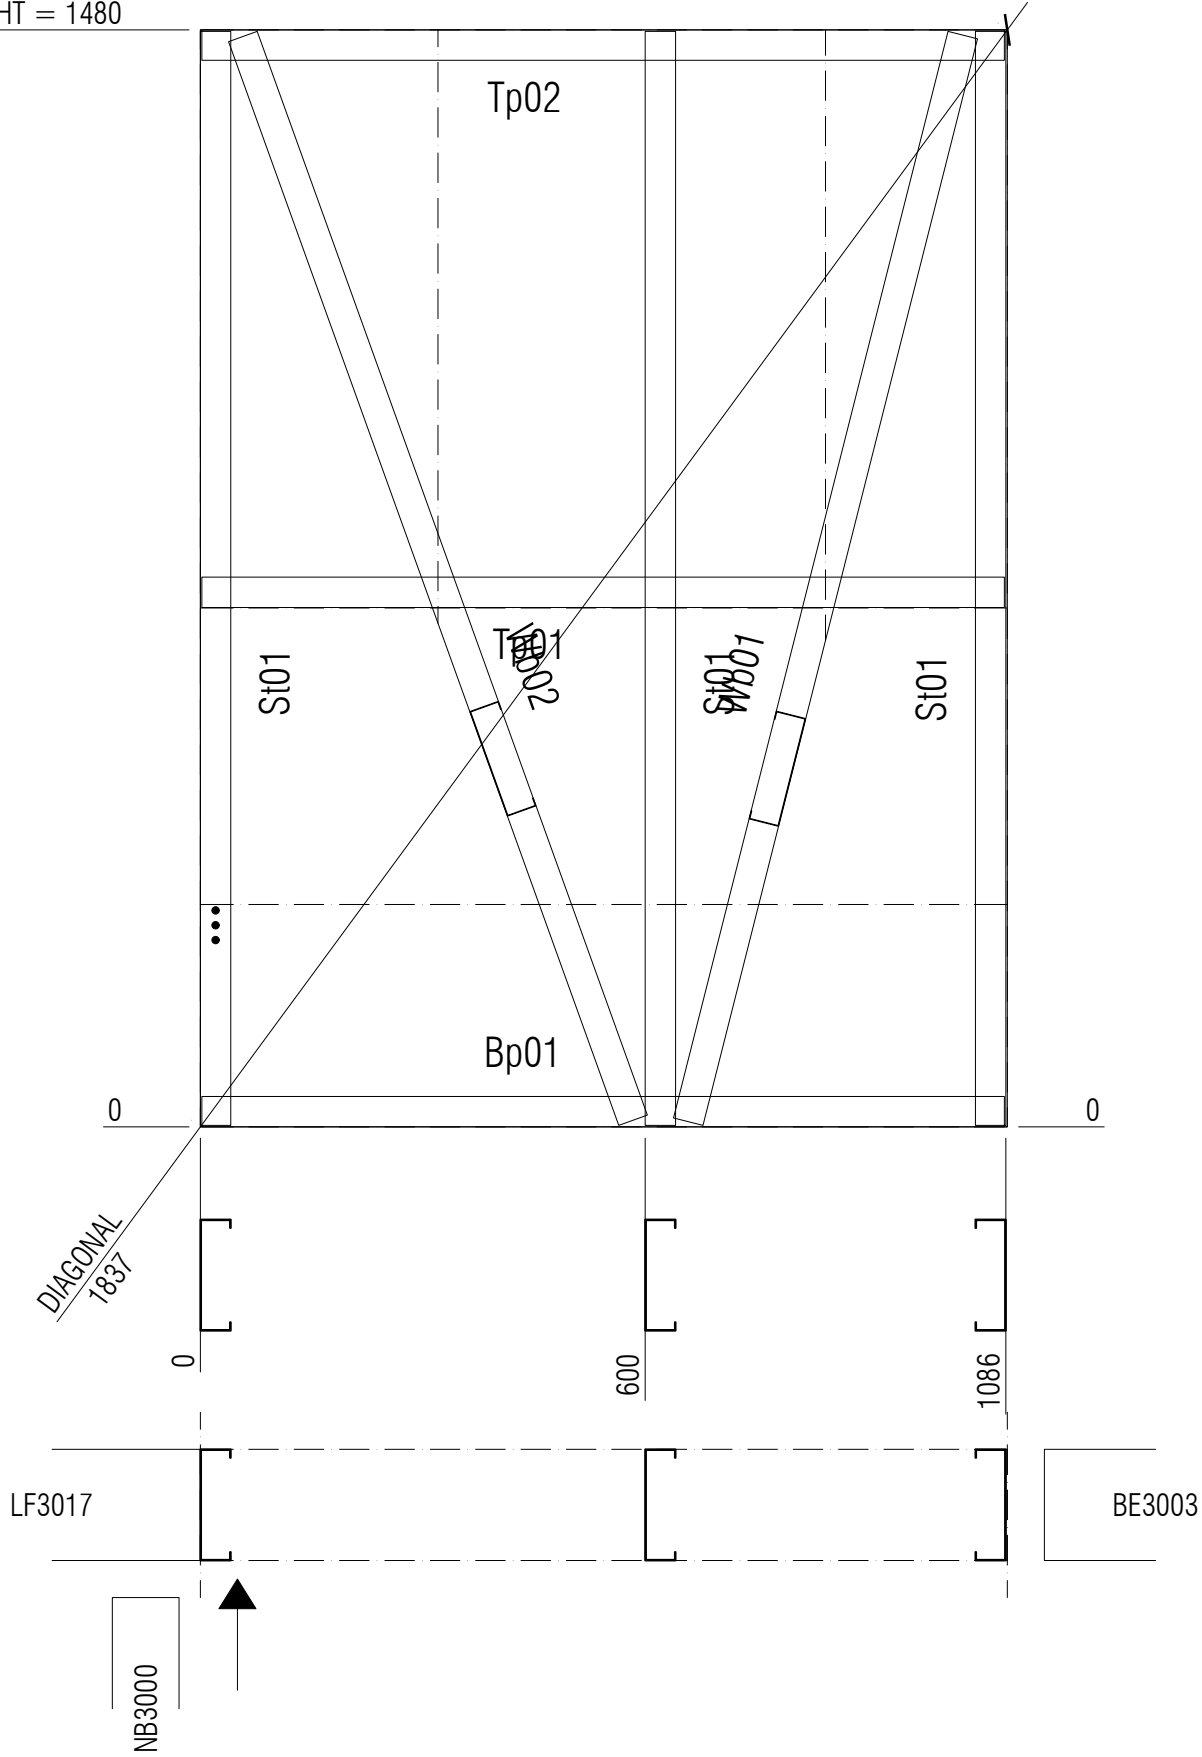

FRAME STICKS NAME	LENGTH	WT	QTY	PROFILE
Tp01	1082	2.0	1	150S41-950-500
Tp02	1082	2.0	1	150S41-950-500
Bp01	1082	2.0	1	150S41-950-500
St01	1476	2.7	3	150S41-950-500
Wb01	1512	2.8	1	150S41-950-500
Wb02	1554	2.9	1	150S41-950-500
TOTAL	10741	19.8	8	

BE3002

AUSTRUSS

DELIVERING SINCE 2003

DRAWN: N.N

PH: 02 4860 1416
OFFICE: 02 4860 1400

REV	DATE	REASON
A	15/09/26	IFC — Issued for construction

AUSTRUSS PROJECT NAME

CALDERWOOD

AUSTRUSS ZONE NUMBER

A3

CLIENT NAME

ADCO

PROJECT ADDRESS

179 CALDERWOOD ROAD
CALDERWOOD NSW 2527

AUSTRUSS PROJECT NUMBER

25363

DRAWING NAME

150 - PANELS

DRAWING NUMBER

LGS-A3-200

REV


A

SCAN FOR 3D

WELD ALL

GUSSET

HEIGHT = 1480

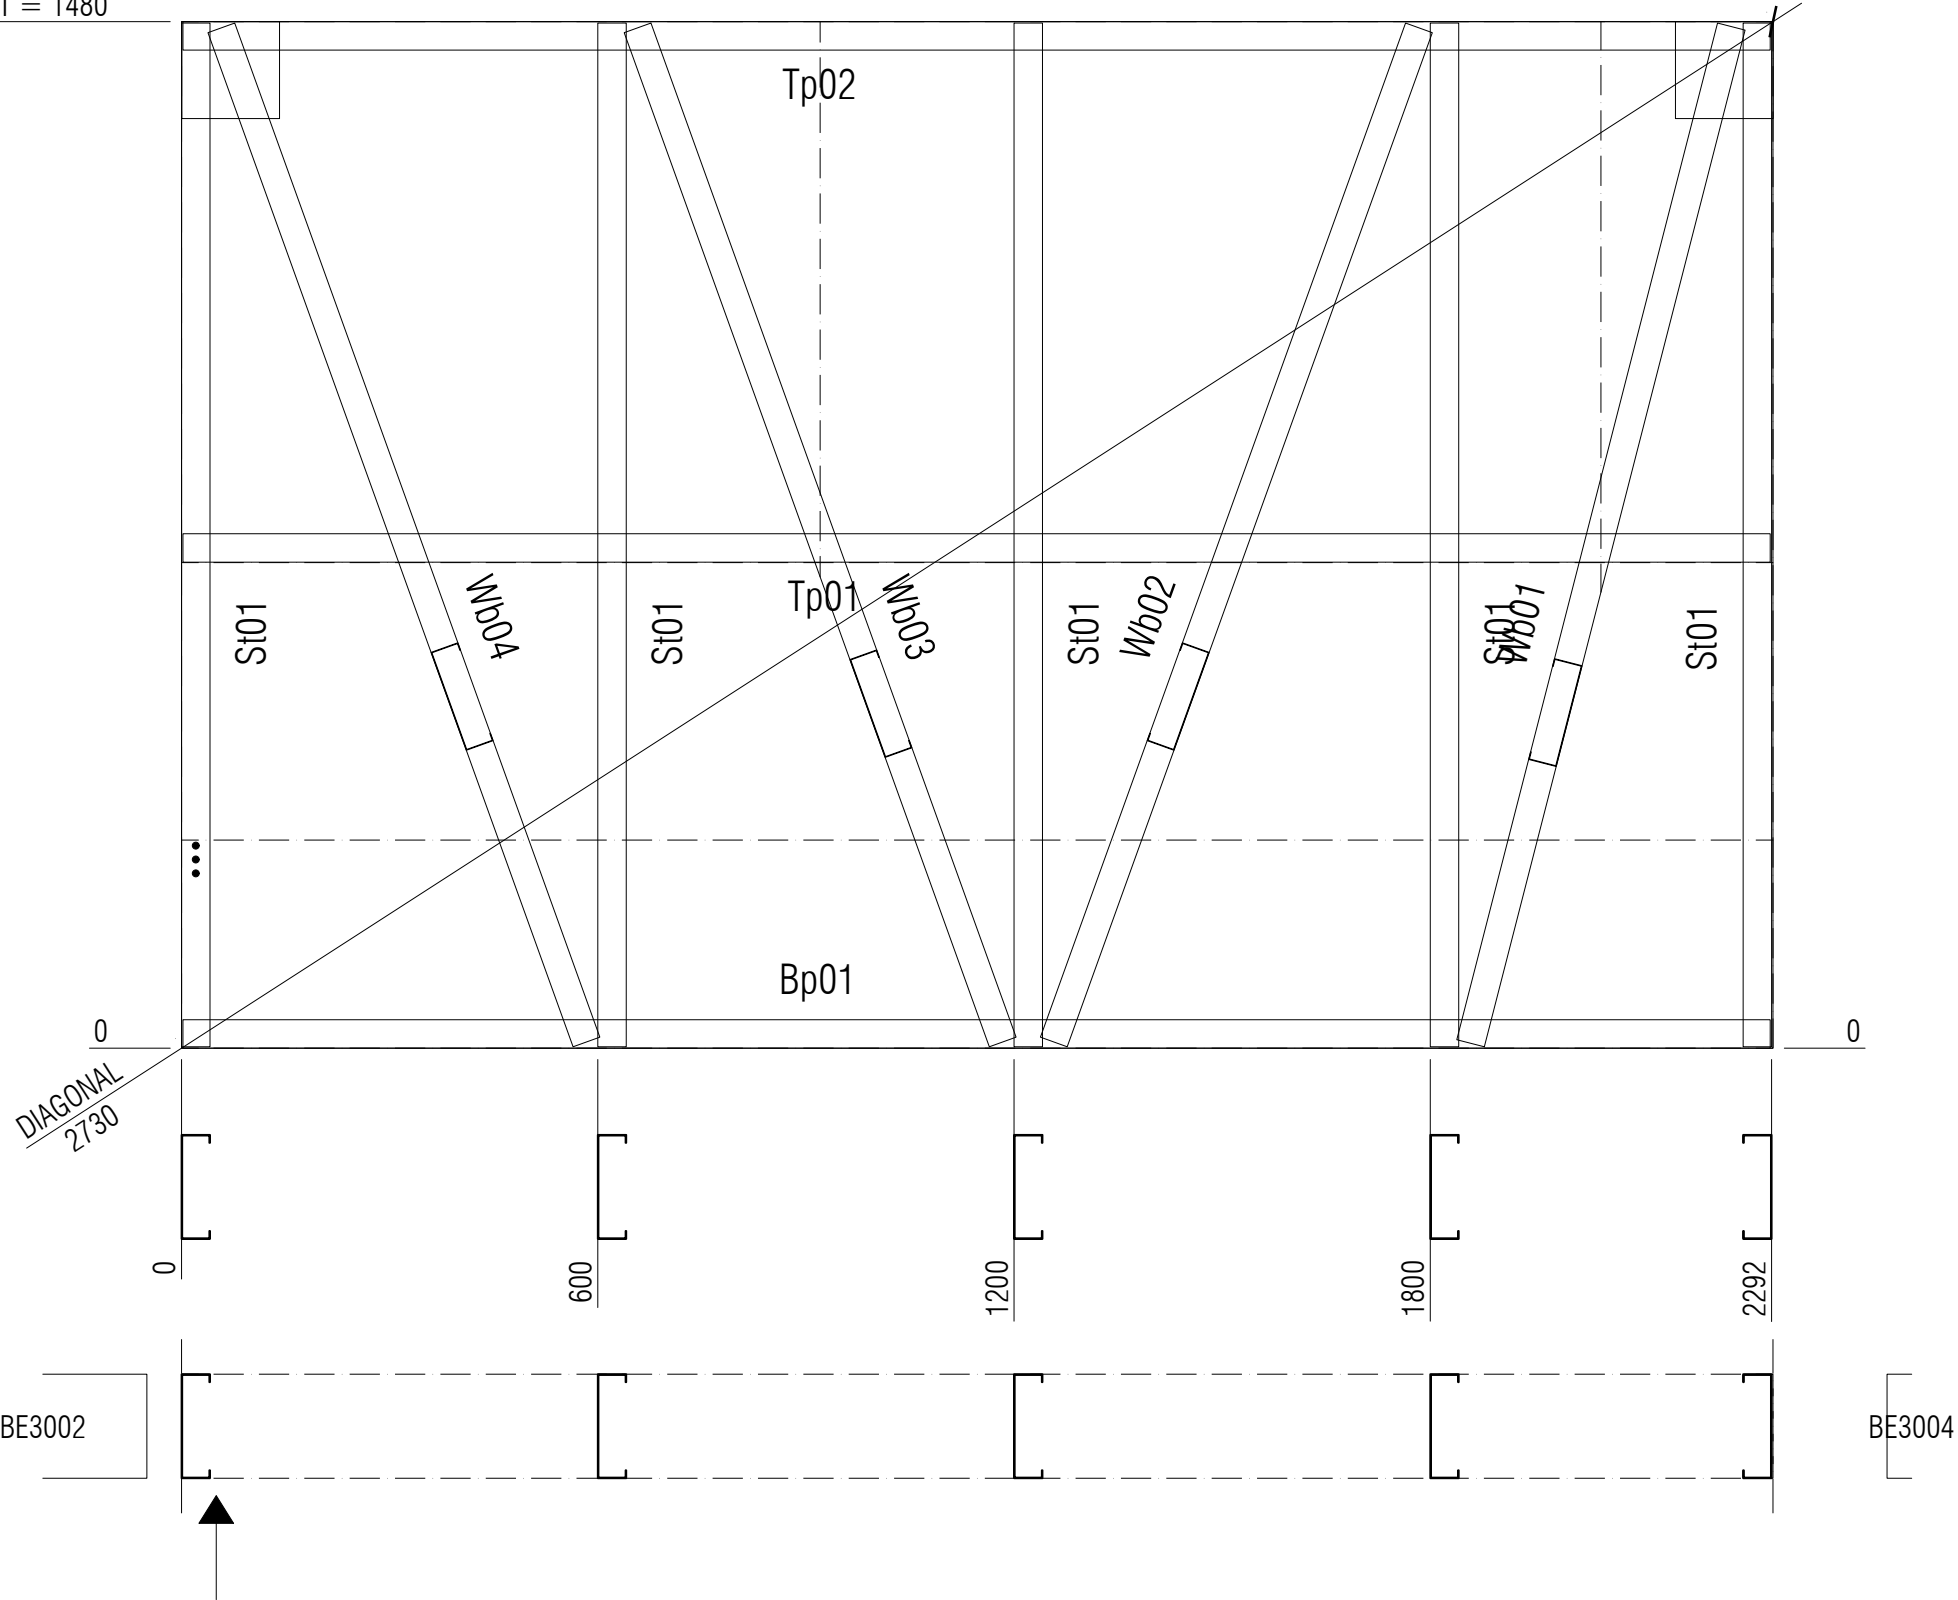

FRAME STICKS				
NAME	LENGTH	WT	QTY	
Tp01	2288	4.2	1	150S41-
Tp02	2288	4.2	1	150S41-
Bp01	2288	4.2	1	150S41-
St01	1476	2.7	5	150S41-
Wb01	1513	2.8	1	150S41-
Wb02	1554	2.9	1	150S41-
Wb03	1554	2.9	1	150S41-
Wb04	1554	2.9	1	150S41-
TOTAL	20418	37.6	12	

BE3003



DELIVERING SINCE 2003

DRAWN: N.N

PH: 02 4860 1416
OFFICE: 02 4860 1400

REV	DATE	REASON
A	15/09/26	IFC — Issued for construction

AUSTRUSS PROJECT NAME
CALDERWOOD

AUSTRUSS ZONE NUMBER
A3

CLIENT NAME
ADCO

PROJECT ADDRESS
**179 CALDERWOOD ROAD
CALDERWOOD NSW 2527**

AUSTRUSS PROJECT NUMBER
25363

DRAWING NAME
150 - PANELS

DRAWING NUMBER
LGS-A3-200

REV
A




SCAN FOR 3D

WELD ALL

GUSSET

HEIGHT = 1480

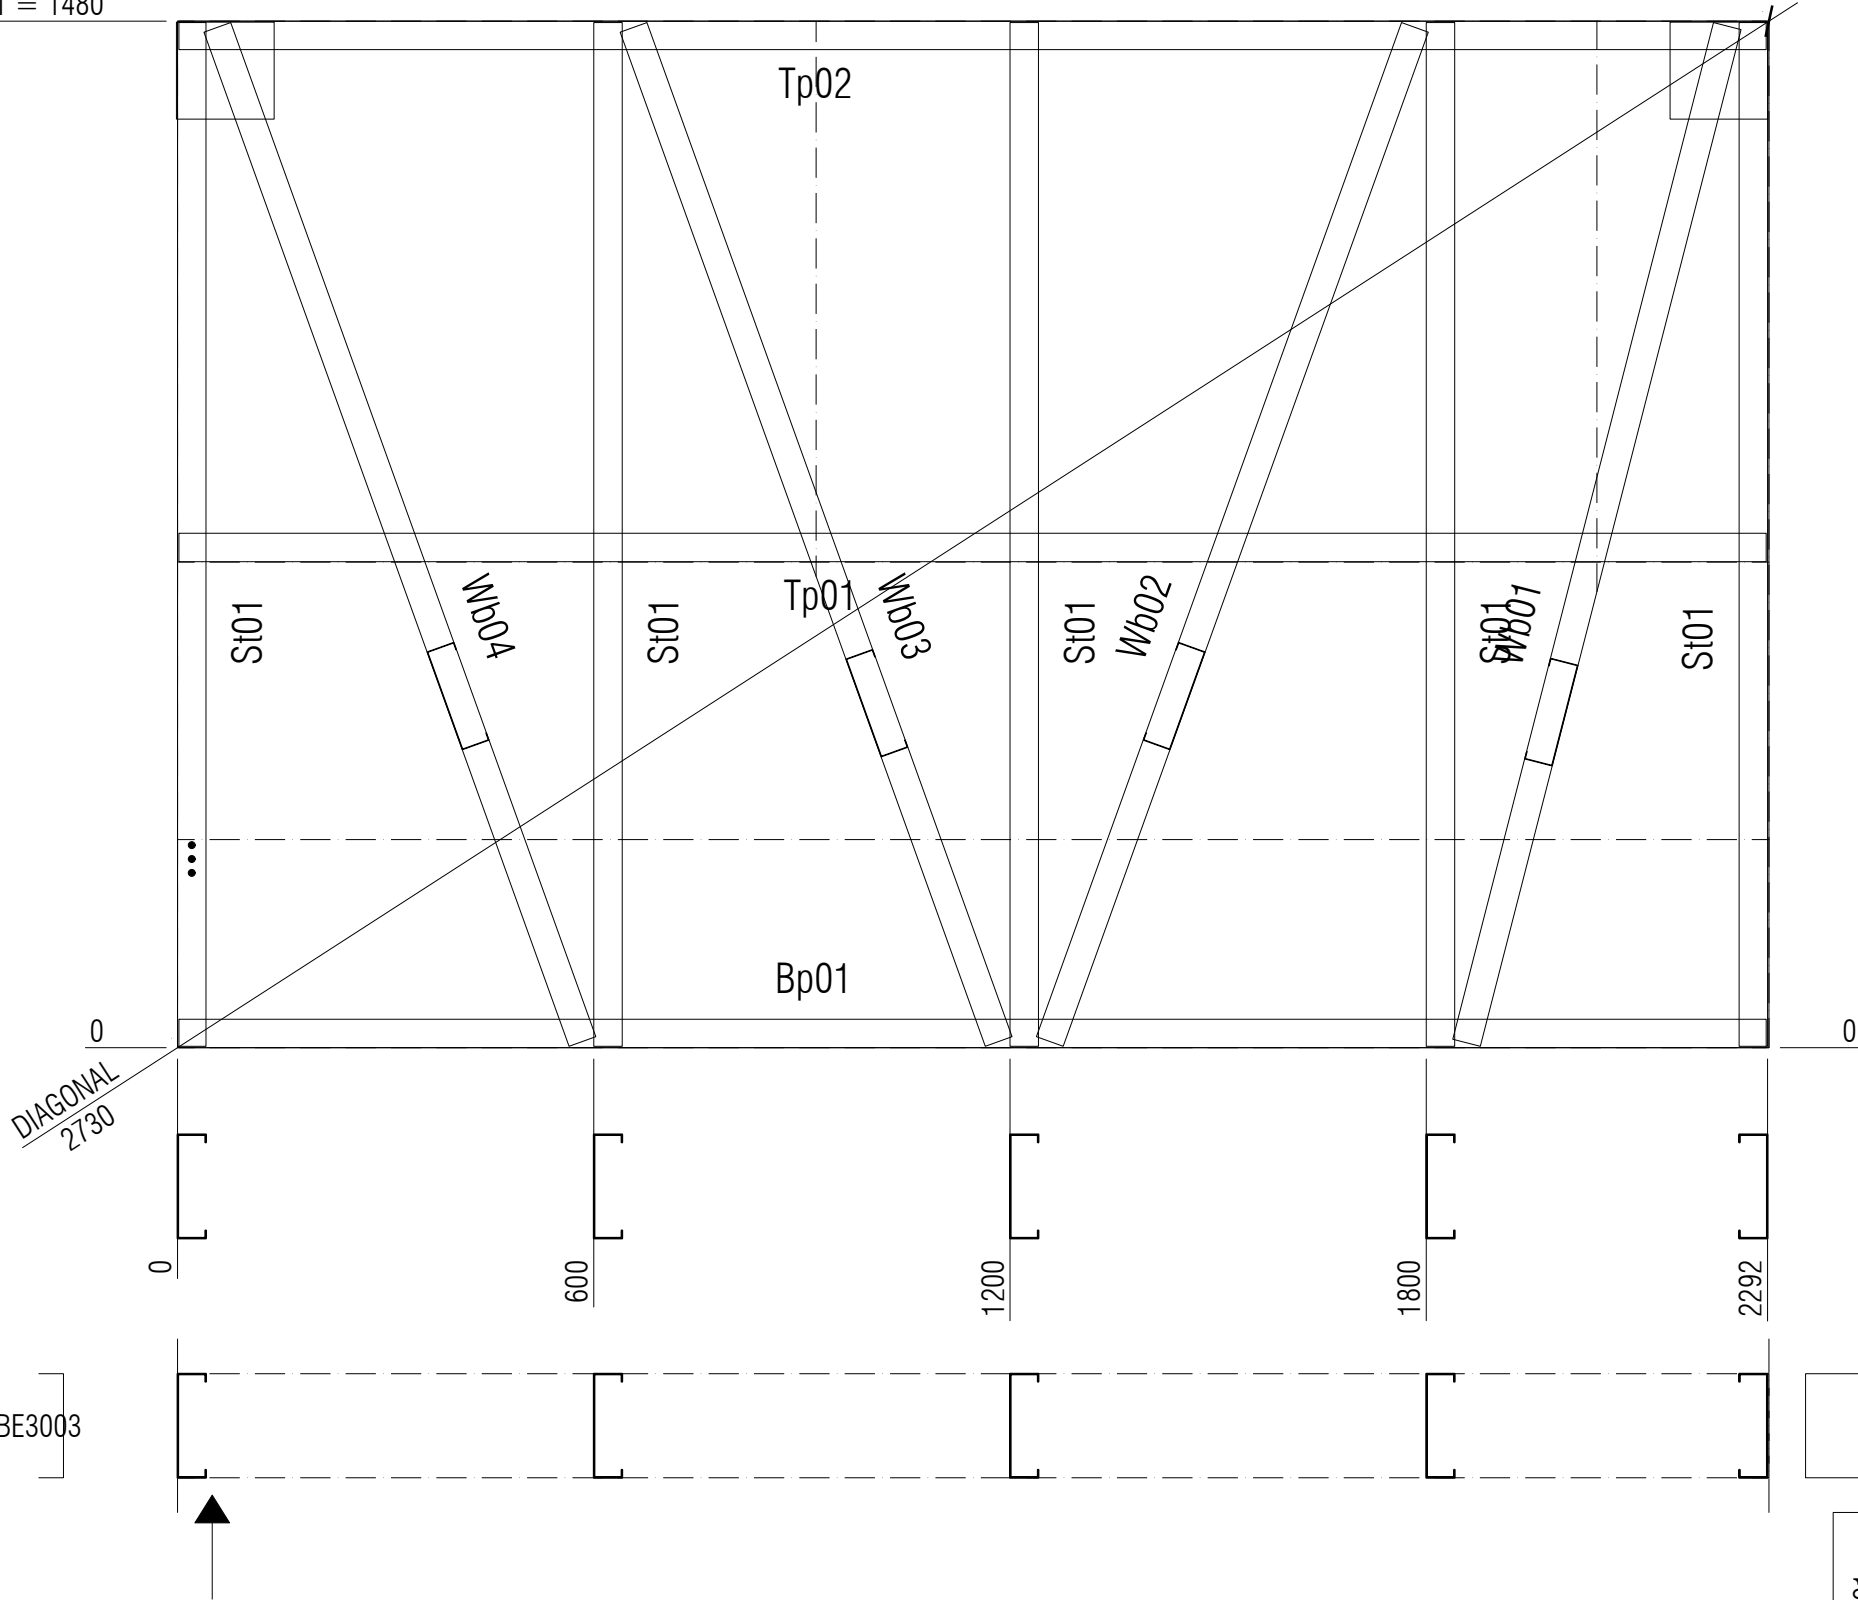

FRAME STICKS				
NAME	LENGTH	WT	QTY	
Tp01	2288	4.2	1	150S41-
Tp02	2288	4.2	1	150S41-
Bp01	2288	4.2	1	150S41-
St01	1476	2.7	5	150S41-
Wb01	1513	2.8	1	150S41-
Wb02	1554	2.9	1	150S41-
Wb03	1554	2.9	1	150S41-
Wb04	1554	2.9	1	150S41-
TOTAL	20418	37.6	12	

BE3004

AUSTRUSS

DELIVERING SINCE 2003

DRAWN: N.N

PH: 02 4860 1416
OFFICE: 02 4860 1400

REV	DATE	REASON
A	15/09/26	IFC — Issued for construction

AUSTRUSS PROJECT NAME

CALDERWOOD

AUSTRUSS ZONE NUMBER

A3

CLIENT NAME

ADCO

PROJECT ADDRESS

179 CALDERWOOD ROAD
CALDERWOOD NSW 2527

AUSTRUSS PROJECT NUMBER

25363

DRAWING NAME

150 - PANELS

DRAWING NUMBER

LGS-A3-200

REV



A

SCAN FOR 3D

WELD ALL

GUSSET

OVERALL HEIGHT = 2300

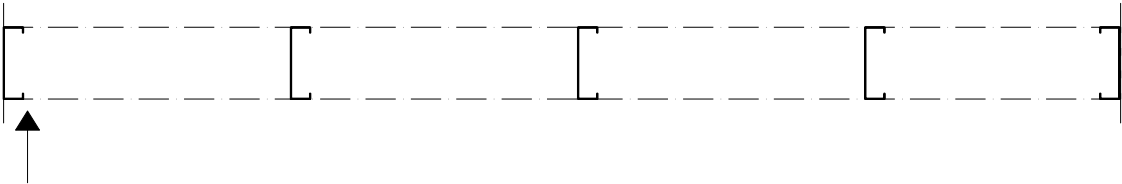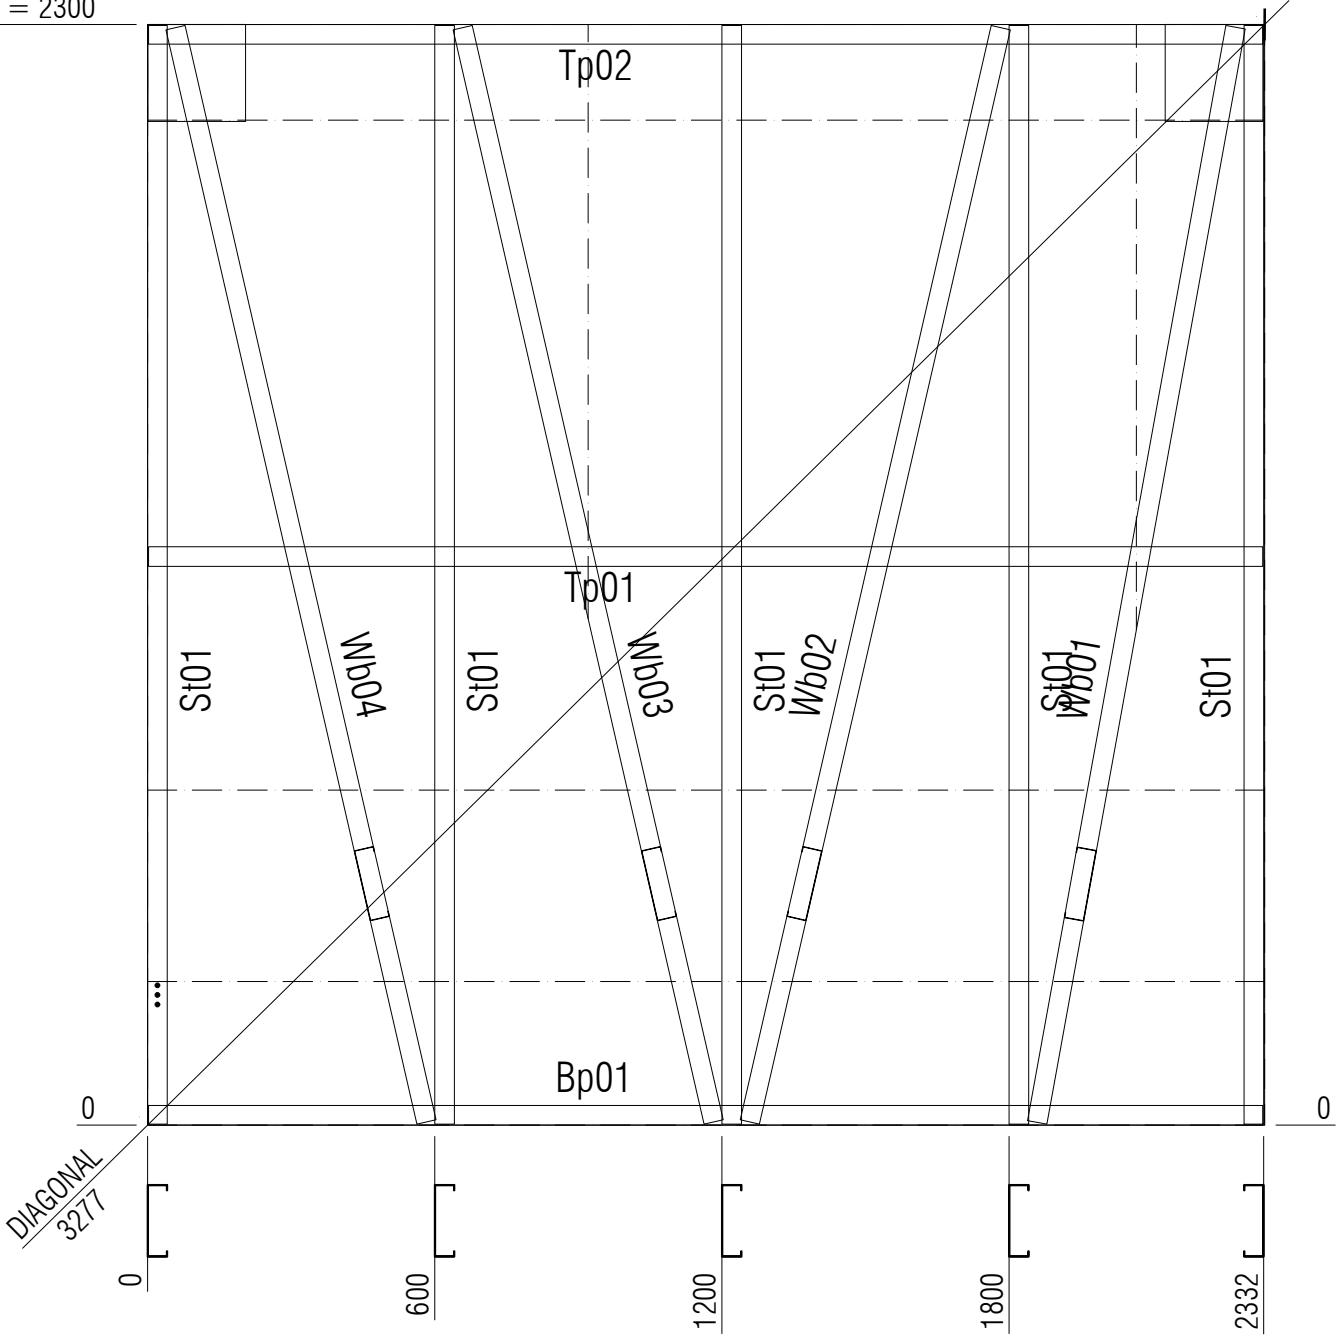

BE3006

FRAME STICKS NAME	LENGTH	WT	QTY	PROFILE
Tp01	2328	4.3	1	150S41-950-500
Tp02	2328	4.3	1	150S41-950-500
Bp01	2328	4.3	1	150S41-950-500
St01	2296	4.2	5	150S41-950-500
Wb01	2326	4.3	1	150S41-950-500
Wb02	2346	4.3	1	150S41-950-500
Wb03	2346	4.3	1	150S41-950-500
Wb04	2346	4.3	1	150S41-950-500
TOTAL	27827	51.2	12	

BE3005

AUSTRUSS

DELIVERING SINCE 2003

DRAWN: N.N

PH: 02 4860 1416
OFFICE: 02 4860 1400

REV	DATE	REASON
A	15/09/26	IFC — Issued for construction

AUSTRUSS PROJECT NAME

CALDERWOOD

AUSTRUSS ZONE NUMBER

A3

CLIENT NAME

ADCO

PROJECT ADDRESS

179 CALDERWOOD ROAD
CALDERWOOD NSW 2527

AUSTRUSS PROJECT NUMBER

25363

DRAWING NAME

150 - PANELS

DRAWING NUMBER

LGS-A3-200

REV


A

SCAN FOR 3D


WELD ALL

GUSSET

OVERALL HEIGHT = 2300

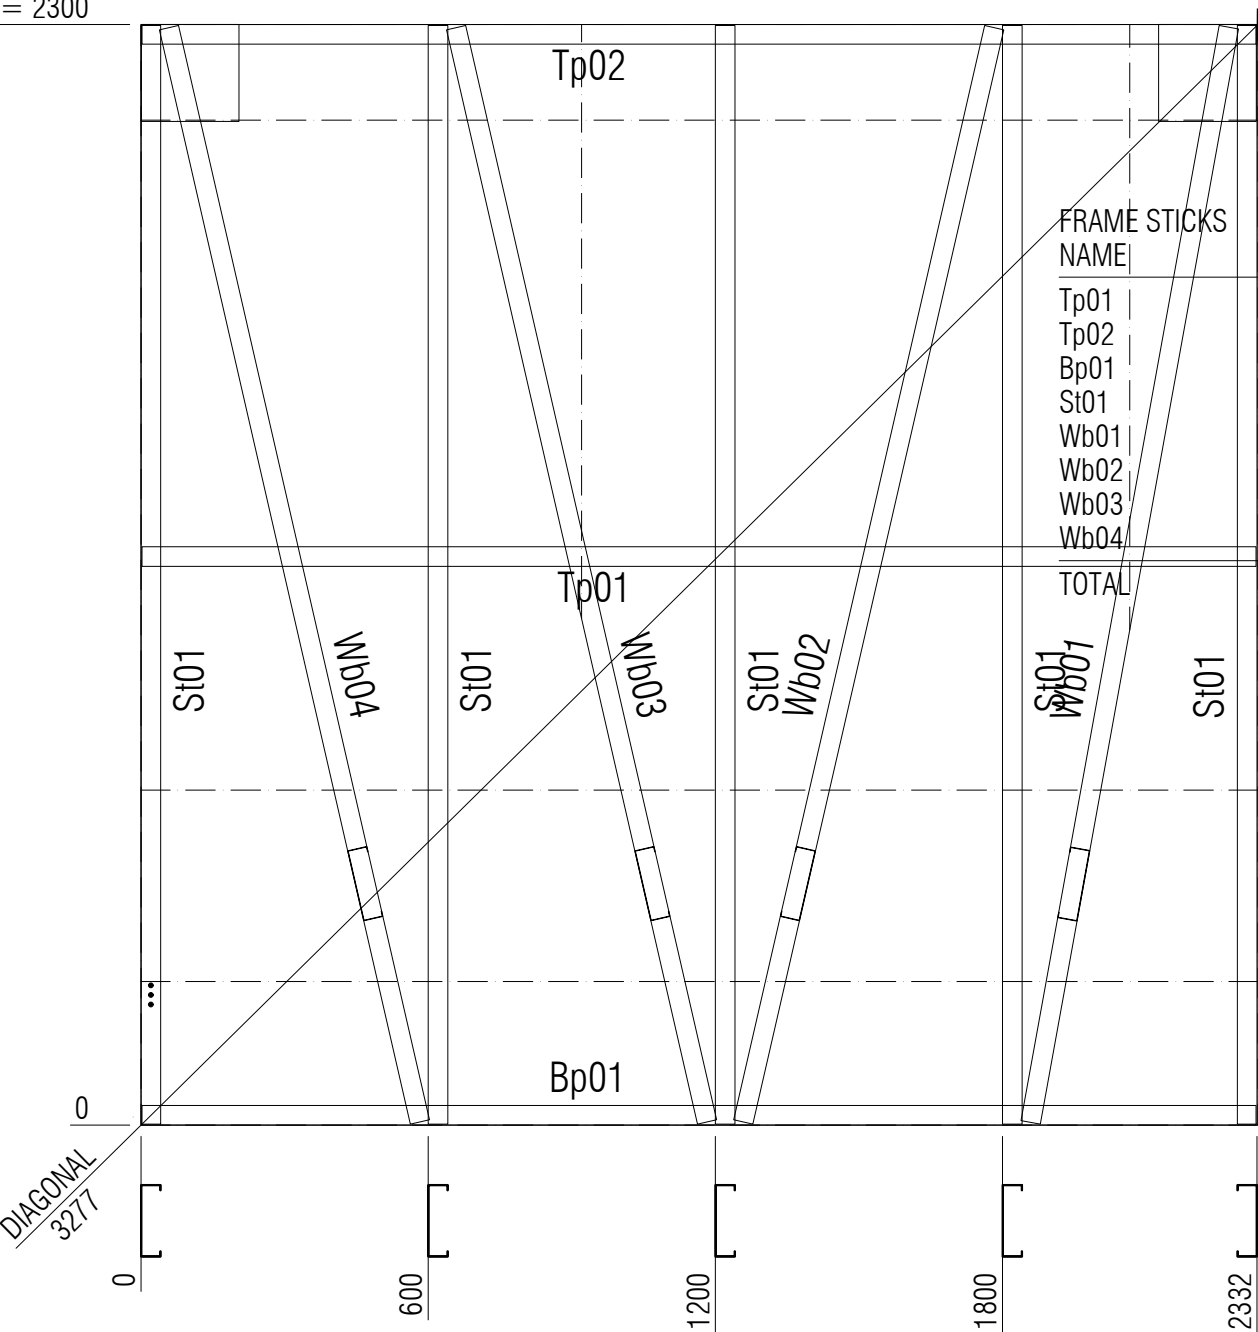

FRAME STICKS				
NAME	LENGTH	WT	QTY	PROFILE
Tp01	2328	4.3	1	150S41-950-500
Tp02	2328	4.3	1	150S41-950-500
Bp01	2328	4.3	1	150S41-950-500
St01	2296	4.2	5	150S41-950-500
Wb01	2326	4.3	1	150S41-950-500
Wb02	2346	4.3	1	150S41-950-500
Wb03	2346	4.3	1	150S41-950-500
Wb04	2346	4.3	1	150S41-950-500
TOTAL	27826	51.2	12	

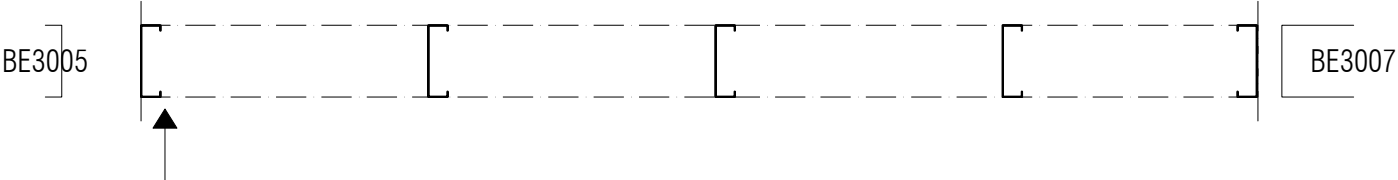

SCAN FOR 3D	
DRAWING NAME	
DRAWING NUMBER	
REV	

BE3006



DELIVERING SINCE 2003

DRAWN: N.N

PH: 02 4860 1416
OFFICE: 02 4860 1400

REV	DATE	REASON
A	15/09/26	IFC — Issued for construction

AUSTRUSS PROJECT NAME

CALDERWOOD

AUSTRUSS ZONE NUMBER

A3

CLIENT NAME

ADCO

PROJECT ADDRESS

179 CALDERWOOD ROAD
CALDERWOOD NSW 2527

AUSTRUSS PROJECT NUMBER

25363

DRAWING NAME

150 - PANELS

DRAWING NUMBER


LGS-A3-200

REV

A

WELD ALL

OVERALL HEIGHT = 2300

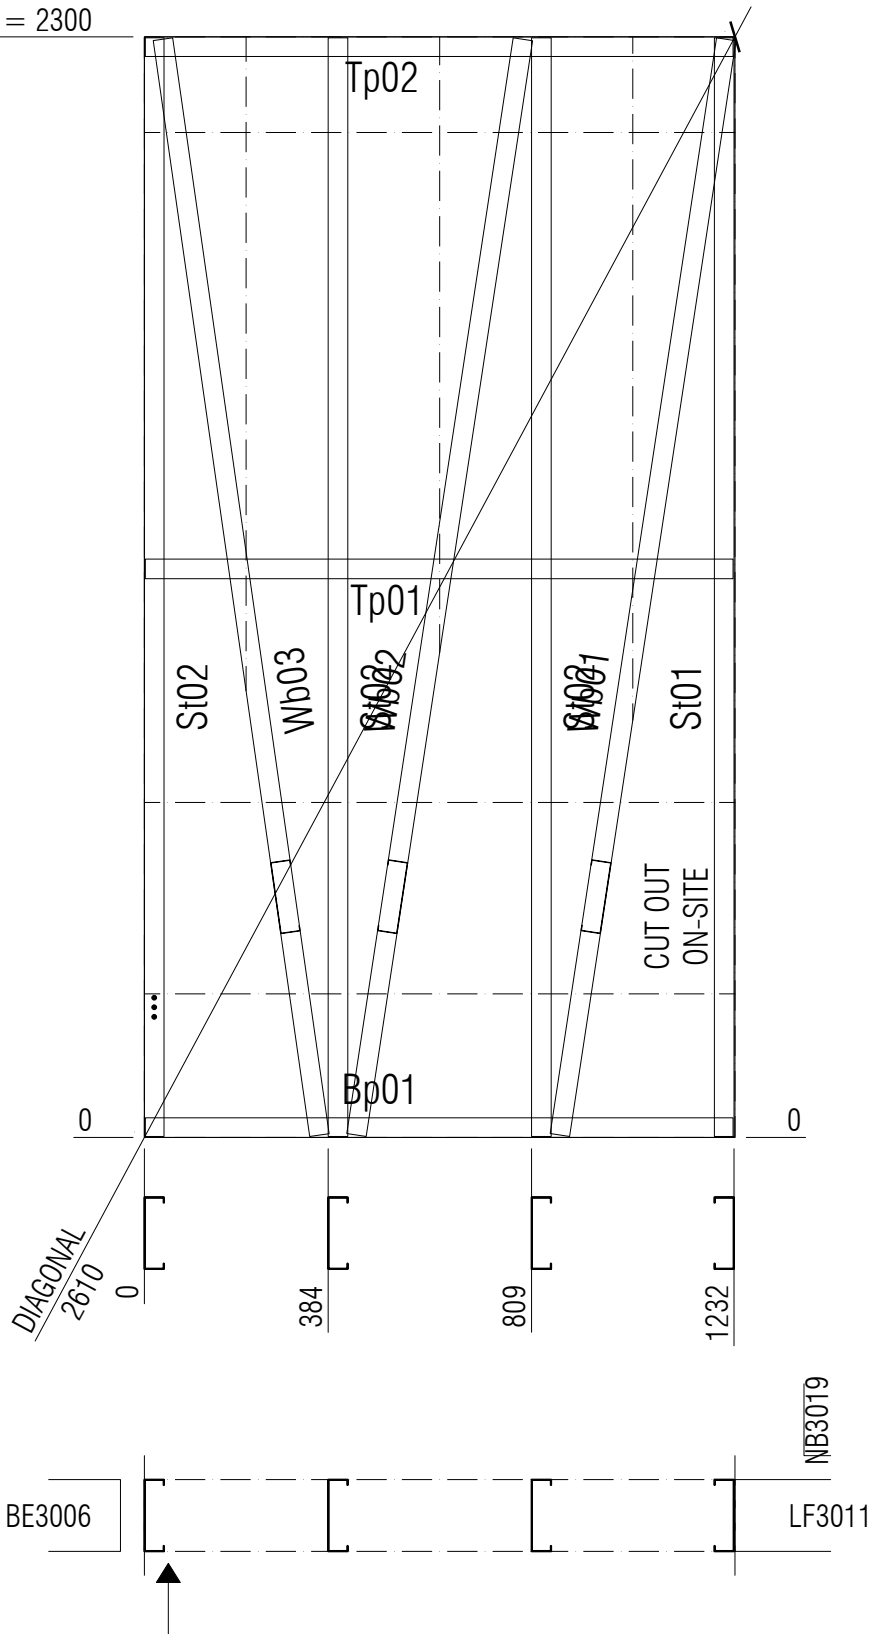


FRAME STICKS NAME	LENGTH	WT	QTY	PROFILE
Tp01	1228	2.3	1	150S41-950-500
Tp02	1228	2.3	1	150S41-950-500
Bp01	1228	2.3	1	150S41-950-500
St01	2296	4.2	1	150S41-950-500
St02	2296	4.2	3	150S41-950-500
Wb01	2316	4.3	1	150S41-950-500
Wb02	2316	4.3	1	150S41-950-500
Wb03	2313	4.3	1	150S41-950-500
TOTAL	19813	36.5	10	

BE3007

AUSTRUSS DELIVERING SINCE 2003		
DRAWN: N.N		PH: 02 4860 1416 OFFICE: 02 4860 1400
REV	DATE	REASON
A	15/09/26	IFC — Issued for construction
AUSTRUSS PROJECT NAME CALDERWOOD		
AUSTRUSS ZONE NUMBER A3		
CLIENT NAME ADCO		
PROJECT ADDRESS 179 CALDERWOOD ROAD CALDERWOOD NSW 2527		
AUSTRUSS PROJECT NUMBER 25363		
DRAWING NAME 150 - PANELS		
DRAWING NUMBER LGS-A3-200		REV A



SCAN FOR 3D

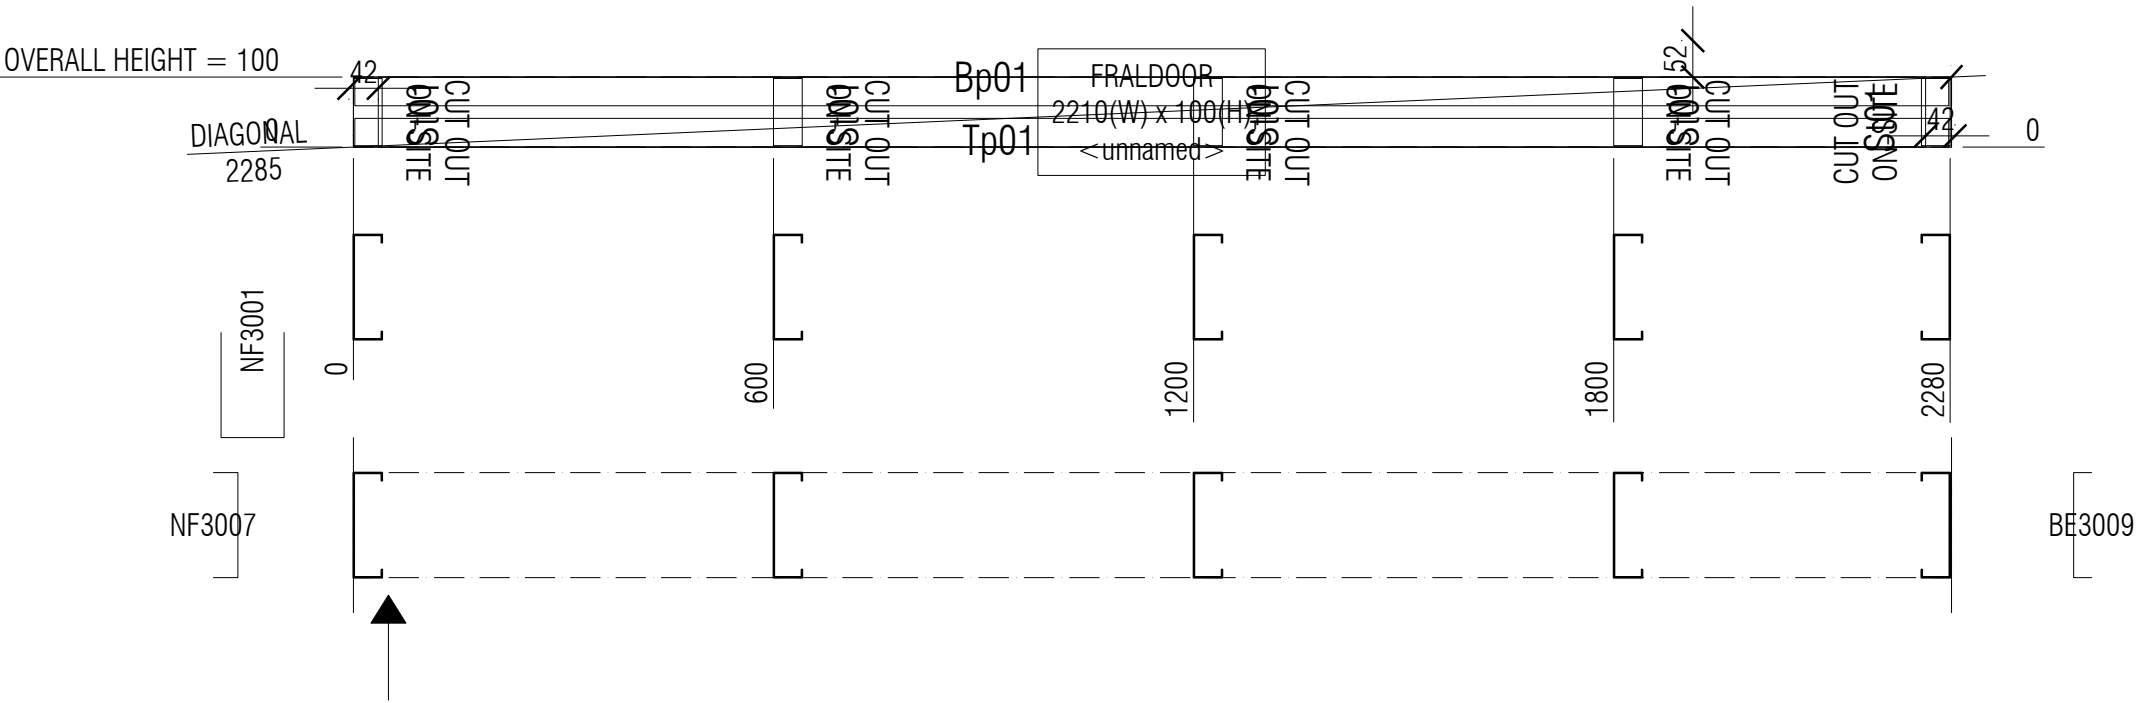

FRAME STICKS				
NAME	LENGTH	WT	QTY	PROFILE
Tp01	2276	4.2	1	150S41-950-500
Bp01	2276	4.2	1	150S41-950-500
St01	96	0.2	5	150S41-950-500
TOTAL	5033	9.3	7	

BE3008



DELIVERING SINCE 2003

DRAWN: N.N

PH: 02 4860 1416
OFFICE: 02 4860 1400

REV	DATE	REASON
A	15/09/26	IFC — Issued for construction

AUSTRUSS PROJECT NAME

CALDERWOOD

AUSTRUSS ZONE NUMBER

A3

CLIENT NAME

ADCO

PROJECT ADDRESS

179 CALDERWOOD ROAD
CALDERWOOD NSW 2527

AUSTRUSS PROJECT NUMBER

25363

DRAWING NAME

150 - PANELS

DRAWING NUMBER


LGS-A3-200

REV

A

SCAN FOR 3D



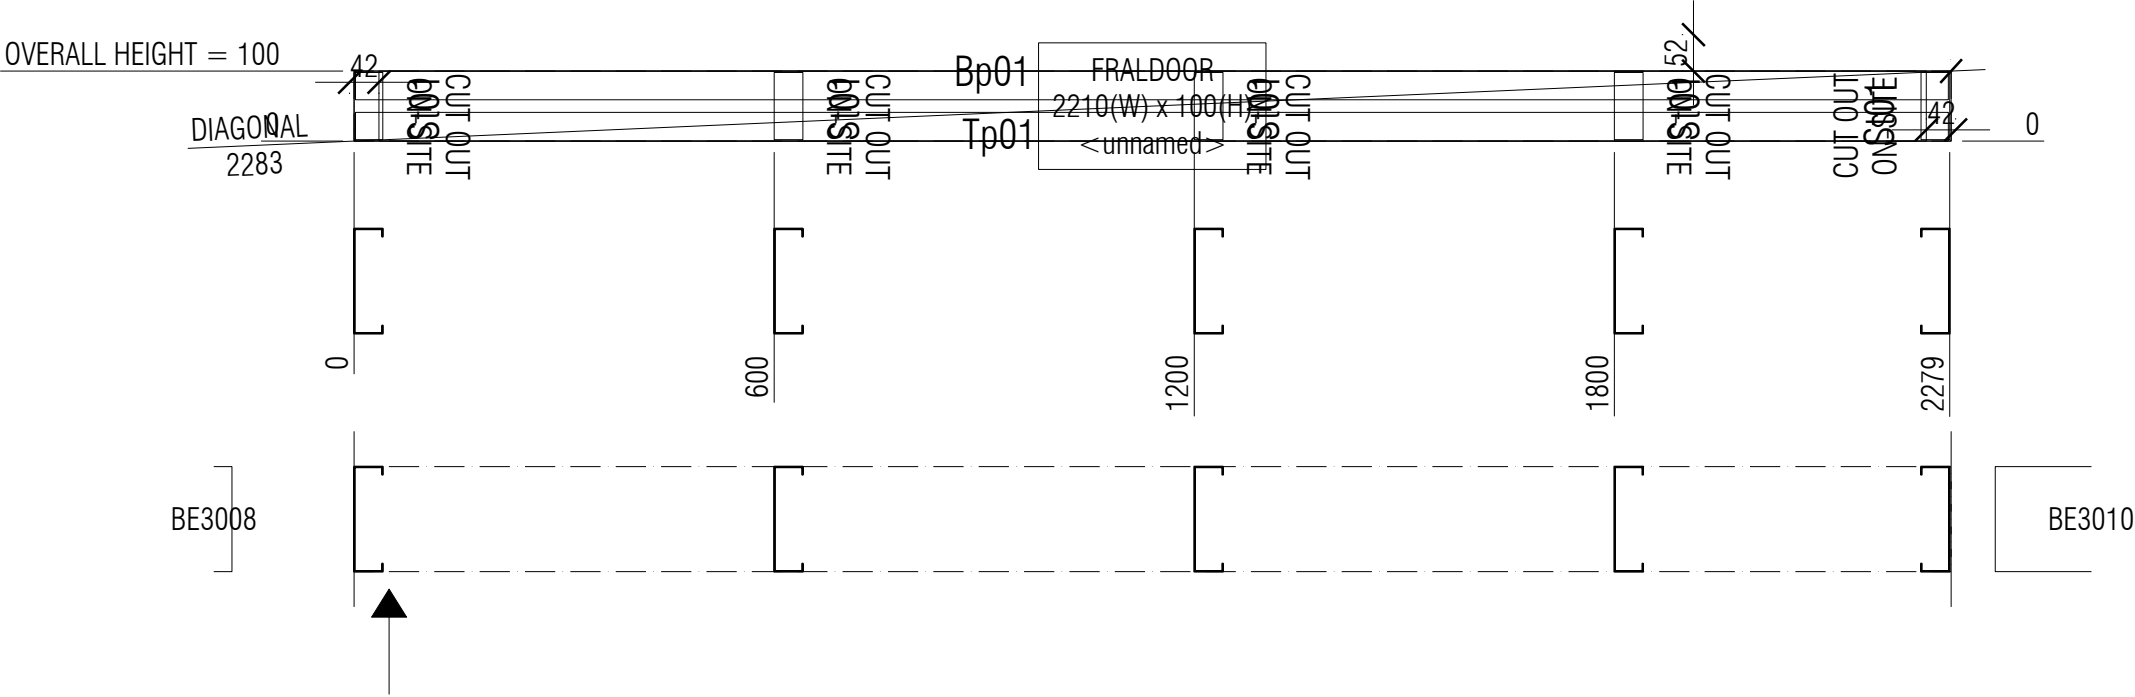

FRAME STICKS				
NAME	LENGTH	WT	QTY	PROFILE
Tp01	2275	4.2	1	150S41-950-500
Bp01	2275	4.2	1	150S41-950-500
St01	96	0.2	5	150S41-950-500
TOTAL	5030	9.3	7	

BE3009



DELIVERING SINCE 2003

DRAWN: N.N

PH: 02 4860 1416
OFFICE: 02 4860 1400

REV	DATE	REASON
A	15/09/26	IFC — Issued for construction

AUSTRUSS PROJECT NAME
CALDERWOOD

AUSTRUSS ZONE NUMBER
A3

CLIENT NAME
ADCO

PROJECT ADDRESS
179 CALDERWOOD ROAD
CALDERWOOD NSW 2527

AUSTRUSS PROJECT NUMBER
25363

DRAWING NAME
150 - PANELS

DRAWING NUMBER
LGS-A3-200

REV
A


SCAN FOR 3D



WELD ALL

GUSSET

OVERALL HEIGHT = 2300

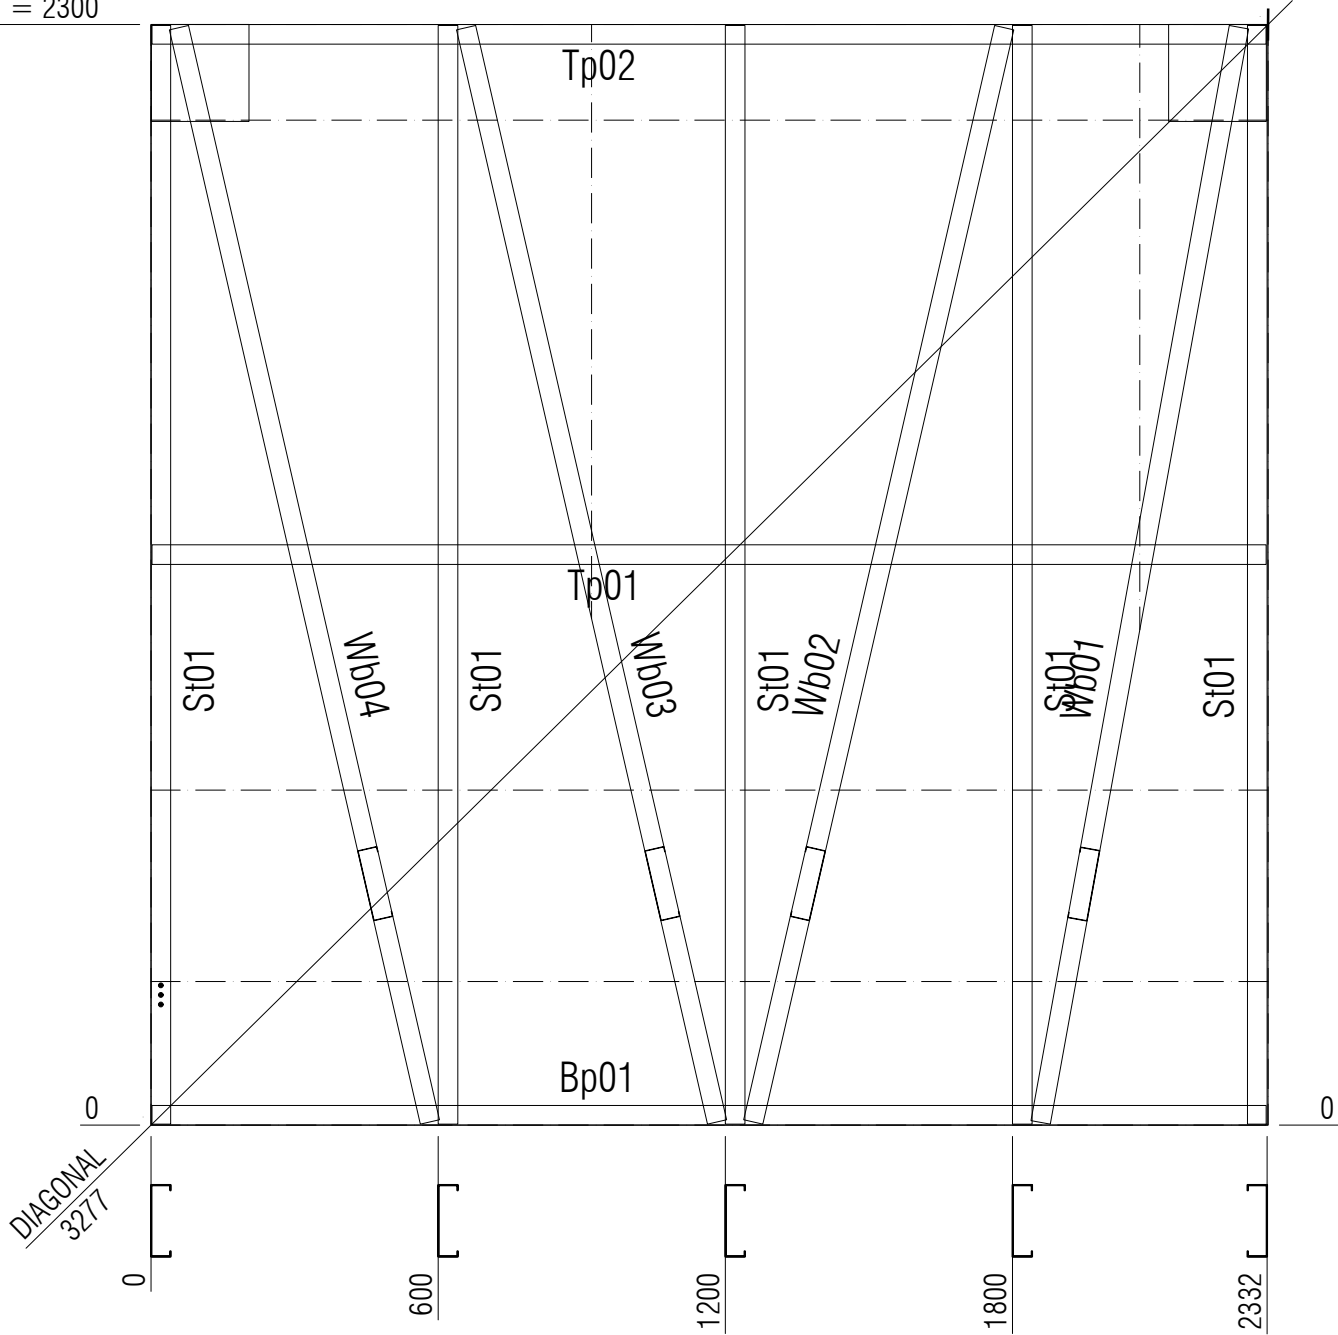

FRAME STICKS NAME	LENGTH	WT	QTY	PROFILE
Tp01	2328	4.3	1	150S41-950-500
Tp02	2328	4.3	1	150S41-950-500
Bp01	2328	4.3	1	150S41-950-500
St01	2296	4.2	5	150S41-950-500
Wb01	2326	4.3	1	150S41-950-500
Wb02	2346	4.3	1	150S41-950-500
Wb03	2346	4.3	1	150S41-950-500
Wb04	2346	4.3	1	150S41-950-500
TOTAL	27827	51.2	12	

BE3011



DELIVERING SINCE 2003

DRAWN: N.N PH: 02 4860 1416
OFFICE: 02 4860 1400

REV	DATE	REASON
A	15/09/26	IFC — Issued for construction

AUSTRUSS PROJECT NAME
CALDERWOOD
AUSTRUSS ZONE NUMBER
A3
CLIENT NAME
ADCO
PROJECT ADDRESS
**179 CALDERWOOD ROAD
CALDERWOOD NSW 2527**

AUSTRUSS PROJECT NUMBER
25363
DRAWING NAME
150 - PANELS
DRAWING NUMBER
LGS-A3-200
REV
A




SCAN FOR 3D

WELD ALL

GUSSET

OVERALL HEIGHT = 2300

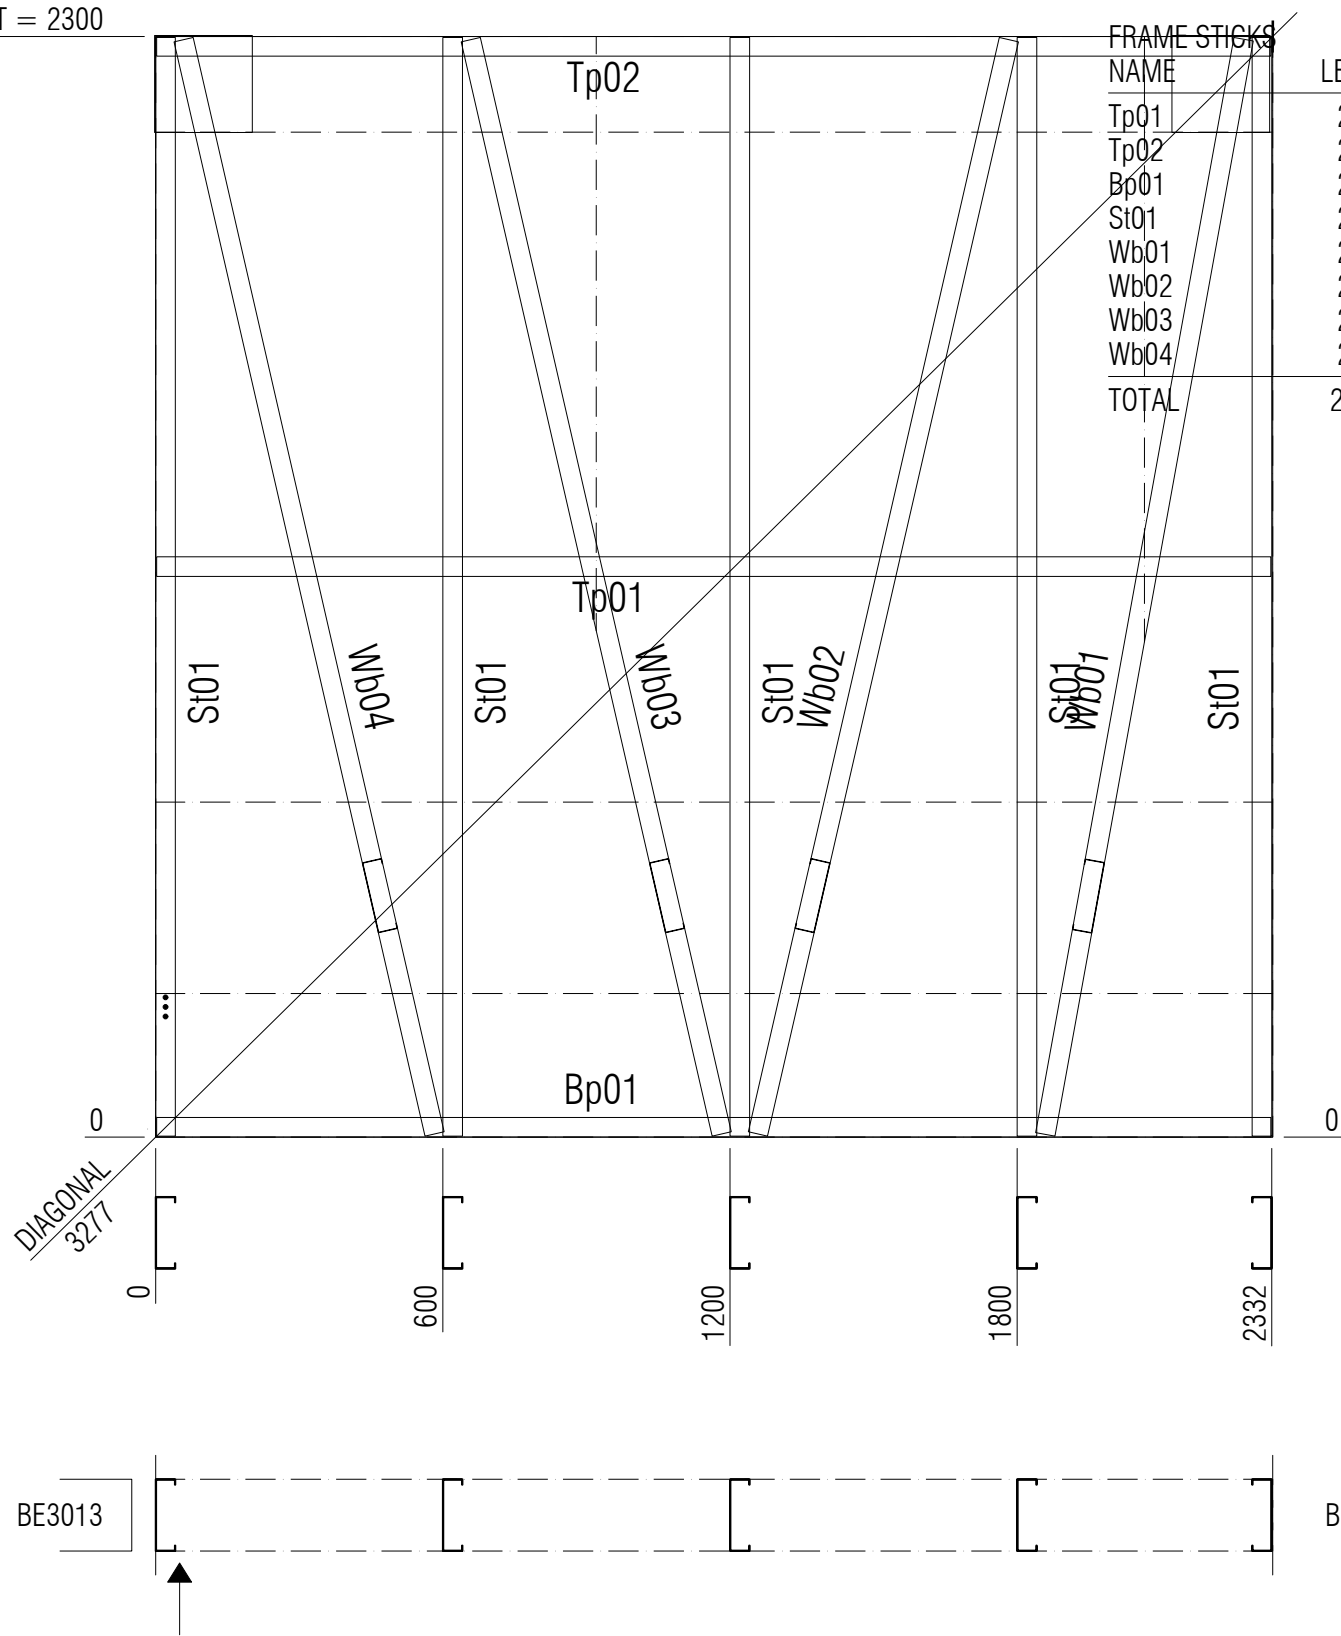

FRAME STICKS				
NAME	LENGTH	WT	QTY	PROFILE
Tp01	2328	4.3	1	150S41-950-500
Tp02	2328	4.3	1	150S41-950-500
Bp01	2328	4.3	1	150S41-950-500
St01	2296	4.2	5	150S41-950-500
Wb01	2326	4.3	1	150S41-950-500
Wb02	2346	4.3	1	150S41-950-500
Wb03	2346	4.3	1	150S41-950-500
Wb04	2346	4.3	1	150S41-950-500
TOTAL	27827	51.2	12	

BE3012



DELIVERING SINCE 2003

DRAWN: N.N

PH: 02 4860 1416
OFFICE: 02 4860 1400

REV	DATE	REASON
A	15/09/26	IFC — Issued for construction

AUSTRUSS PROJECT NAME

CALDERWOOD

AUSTRUSS ZONE NUMBER

A3

CLIENT NAME

ADCO

PROJECT ADDRESS

179 CALDERWOOD ROAD
CALDERWOOD NSW 2527

AUSTRUSS PROJECT NUMBER

25363

DRAWING NAME

150 - PANELS

DRAWING NUMBER

LGS-A3-200

REV


A



SCAN FOR 3D

WELD ALL

OVERALL HEIGHT = 2300

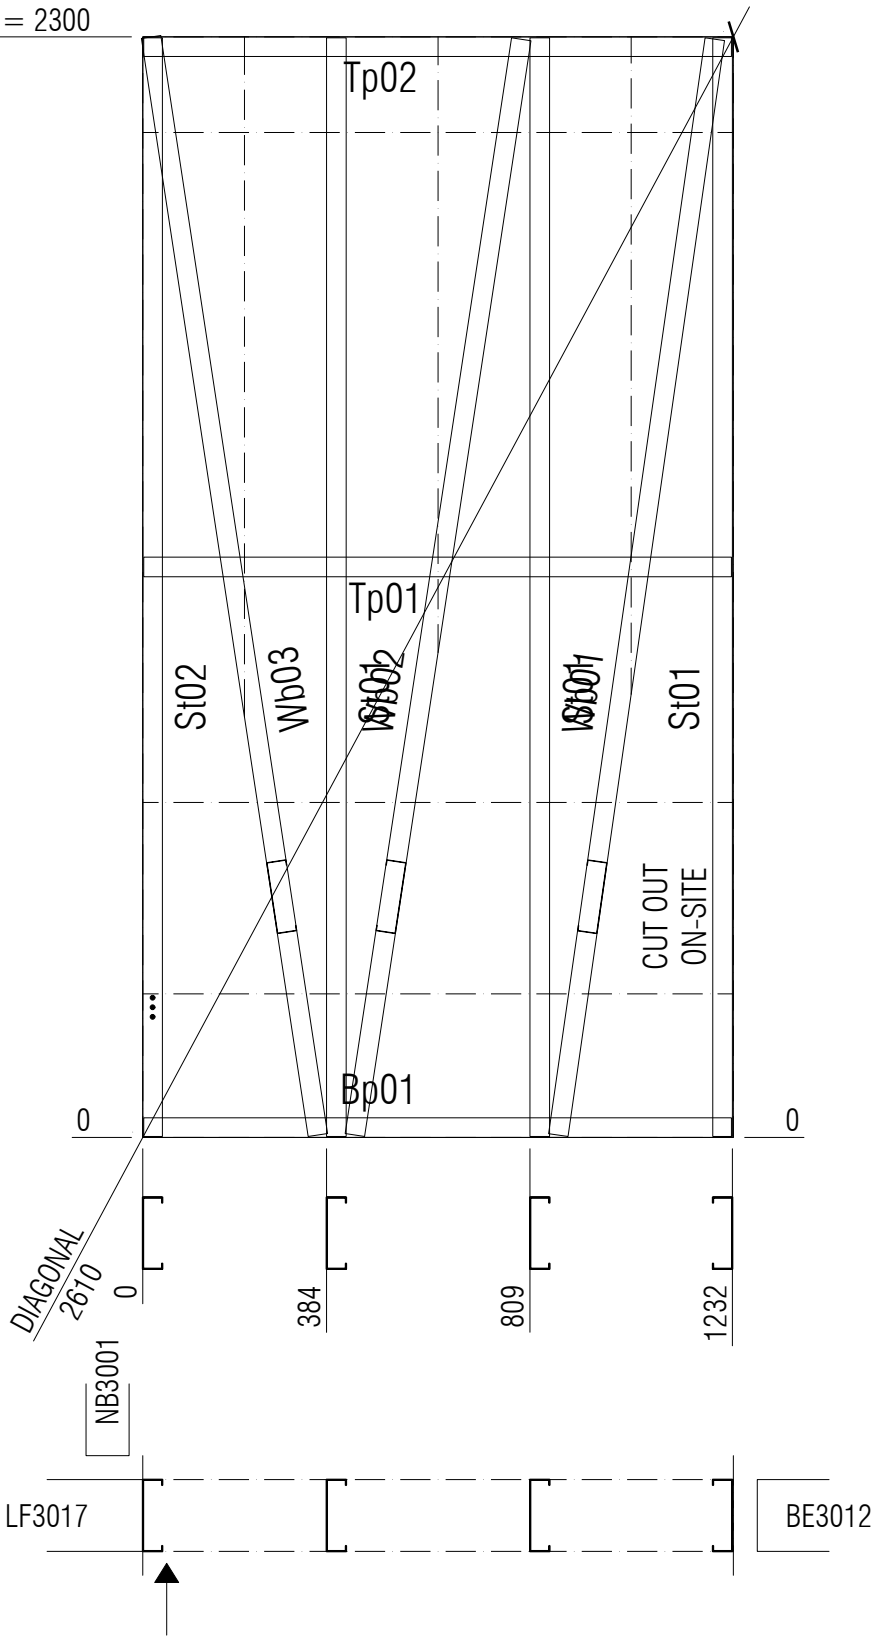

FRAME STICKS				
NAME	LENGTH	WT	QTY	PROFILE
Tp01	1228	2.3	1	150S41-950-500
Tp02	1228	2.3	1	150S41-950-500
Bp01	1228	2.3	1	150S41-950-500
St01	2296	4.2	3	150S41-950-500
St02	2296	4.2	1	150S41-950-500
Wb01	2313	4.3	1	150S41-950-500
Wb02	2316	4.3	1	150S41-950-500
Wb03	2321	4.3	1	150S41-950-500
TOTAL	19817	36.5	10	

BE3013



DELIVERING SINCE 2003

DRAWN: N.N PH: 02 4860 1416
OFFICE: 02 4860 1400

REV	DATE	REASON
A	15/09/26	IFC — Issued for construction

AUSTRUSS PROJECT NAME
CALDERWOOD

AUSTRUSS ZONE NUMBER
A3

CLIENT NAME
ADCO

PROJECT ADDRESS
179 CALDERWOOD ROAD
CALDERWOOD NSW 2527

AUSTRUSS PROJECT NUMBER
25363

DRAWING NAME
150 - PANELS

DRAWING NUMBER
LGS-A3-200


REV
A



SCAN FOR 3D

WELD ALL

OVERALL HEIGHT = 1480

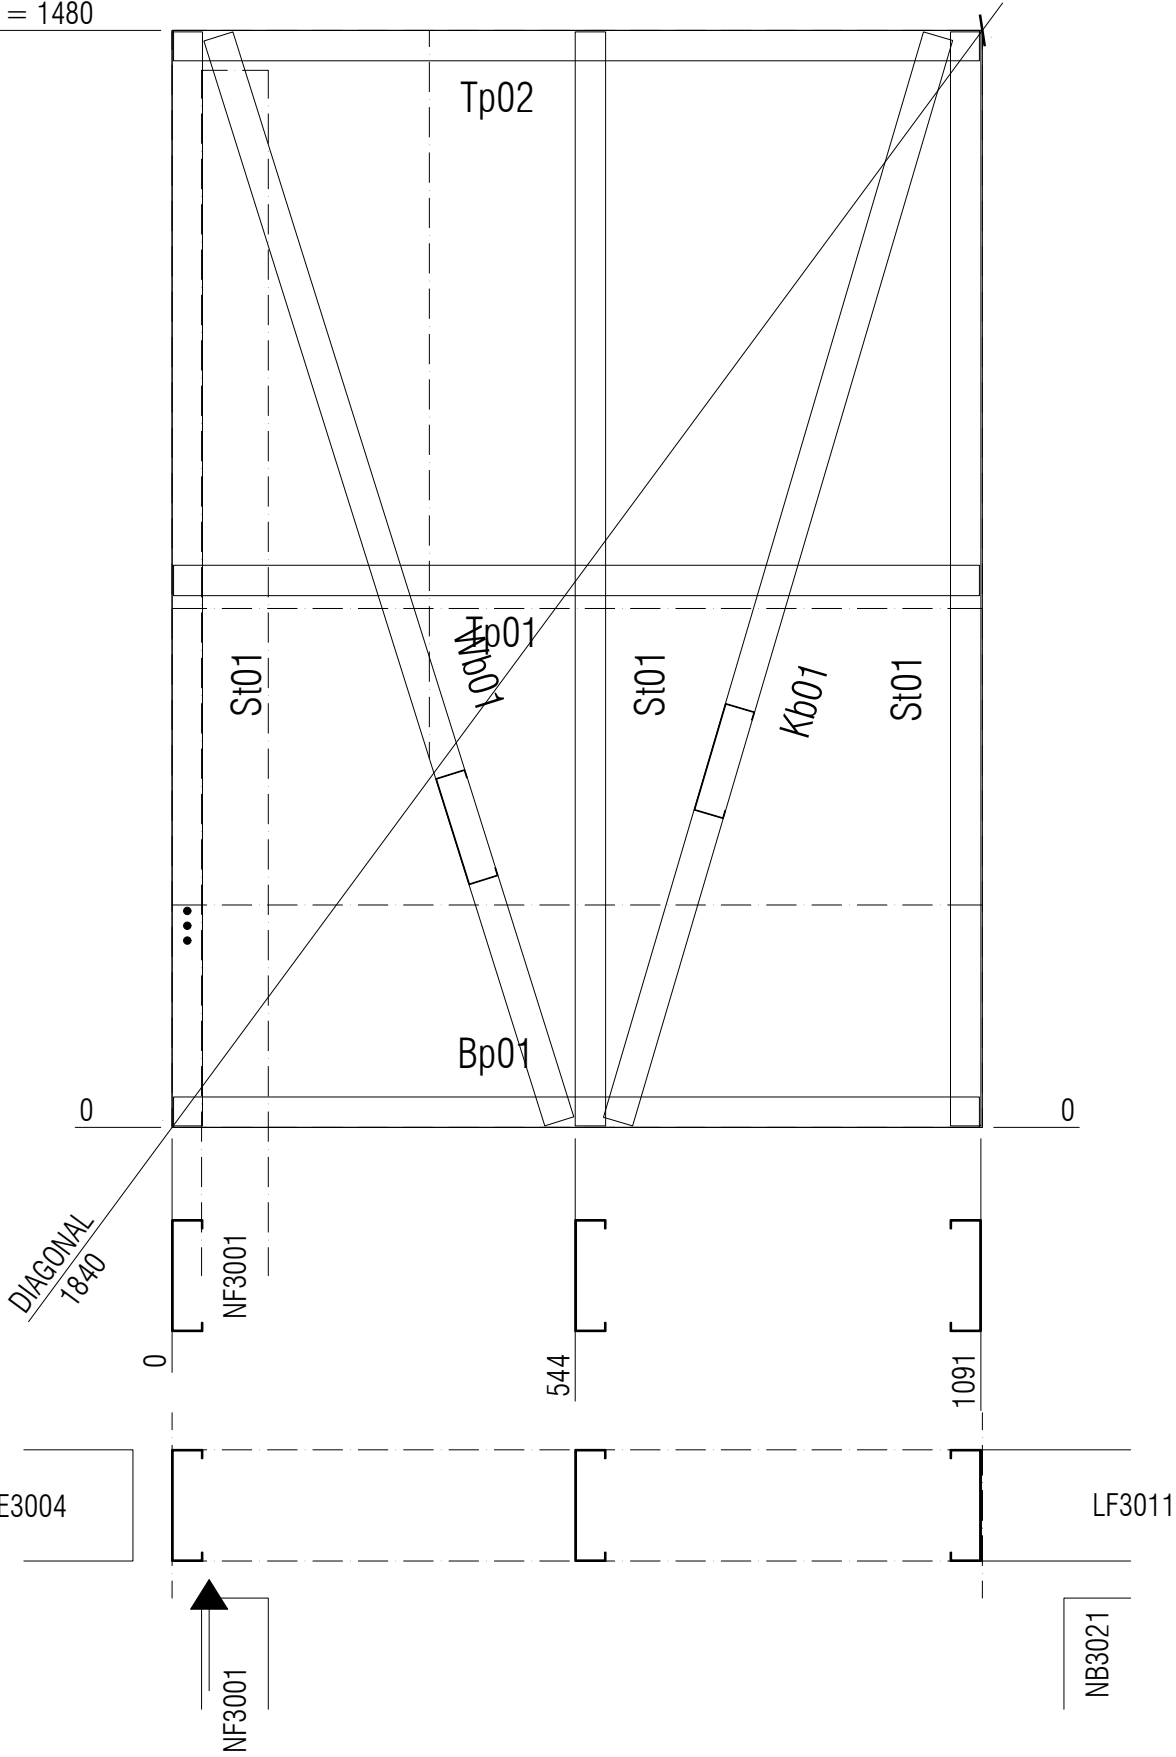

FRAME STICKS				
NAME	LENGTH	WT	QTY	PROFILE
Tp01	1087	2.0	1	150S41-950-500
Tp02	1087	2.0	1	150S41-950-500
Bp01	1087	2.0	1	150S41-950-500
St01	1476	2.7	3	150S41-950-500
Kb01	1527	2.8	1	150S41-950-500
Wb01	1534	2.8	1	150S41-950-500
TOTAL	10749	19.8	8	

BE3014



DELIVERING SINCE 2003

DRAWN: N.N

PH: 02 4860 1416
OFFICE: 02 4860 1400

REV	DATE	REASON
A	15/09/26	IFC — Issued for construction

AUSTRUSS PROJECT NAME

CALDERWOOD

AUSTRUSS ZONE NUMBER
A3

CLIENT NAME
ADCO

PROJECT ADDRESS

179 CALDERWOOD ROAD
CALDERWOOD NSW 2527



SCAN FOR 3D

AUSTRUSS PROJECT NUMBER

25363

DRAWING NAME
150 - PANELS

DRAWING NUMBER
LGS-A3-200

REV
A

WELD ALL


GUSSET

QTY	PROFILE
1	150S41-950-500
1	150S41-950-500
1	150S41-950-500
5	150S41-950-500
1	150S41-950-500
1	150S41-950-500
1	150S41-950-500
1	150S41-950-500
1	150S41-950-500


12

OVERALL HEIGHT = 1031

212x2.4mm PURLIN COIL WELDED TO FRONT SIDE

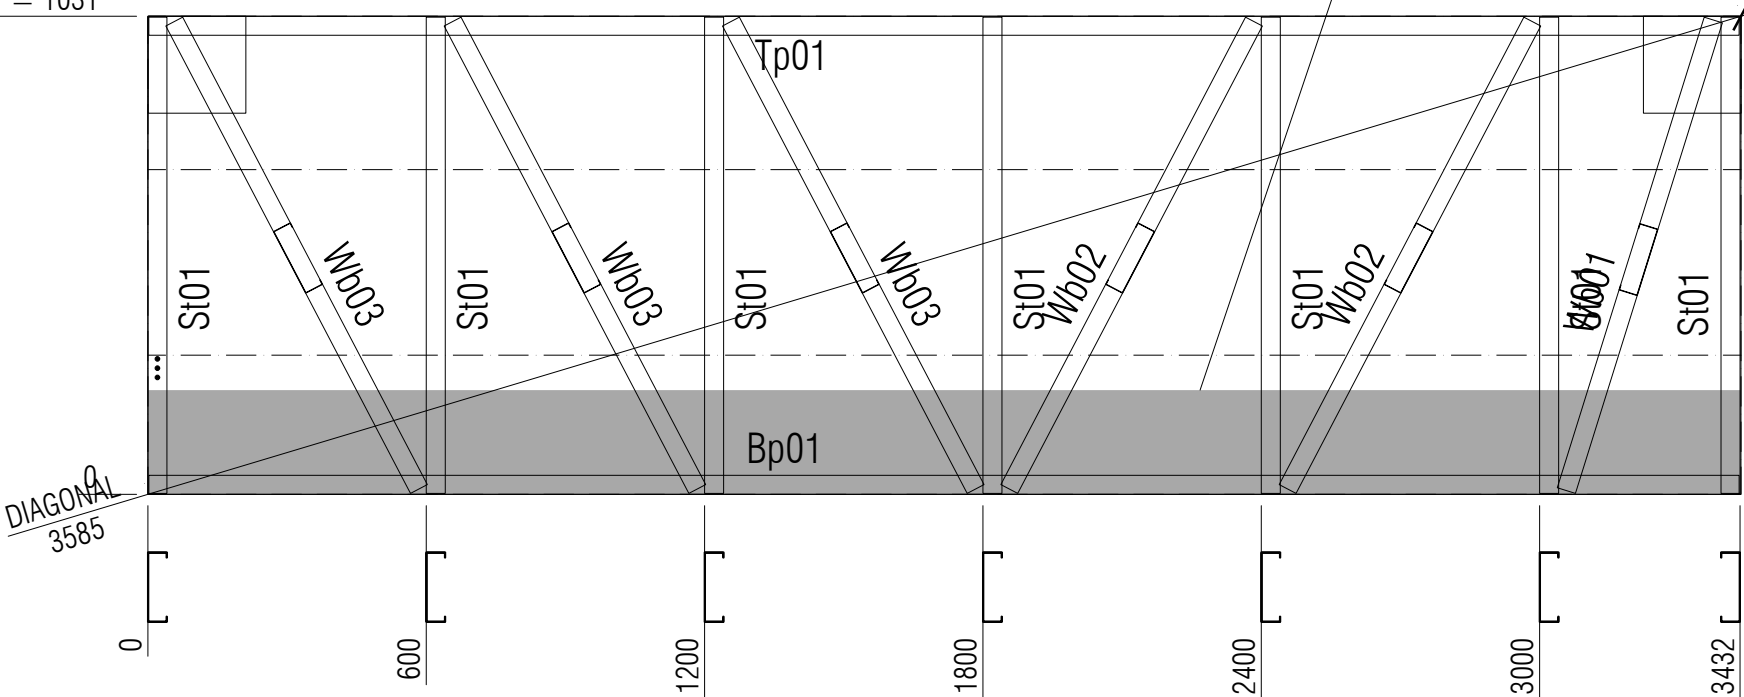

FRAME STICKS				
NAME	LENGTH	WT	QTY	
Tp01	3428	6.3	1	150S41
Bp01	3428	6.3	1	150S41
St01	1027	1.9	7	150S41
Wb01	1063	2.0	1	150S41
Wb02	1137	2.1	2	150S41
Wb03	1137	2.1	3	150S41
TOTAL	20792	38.3	15	

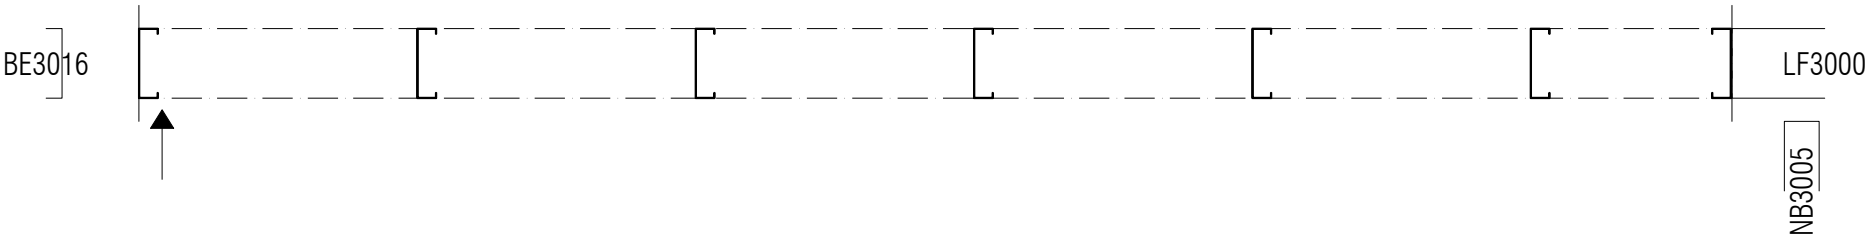

BE3015

AUSTRUSS		
DELIVERING SINCE 2003		
DRAWN: N.N		PH: 02 4860 1416
		OFFICE: 02 4860 1400
REV	DATE	REASON
A	15/09/26	IFC — Issued for construction
AUSTRUSS PROJECT NAME		
CALDERWOOD		
AUSTRUSS ZONE NUMBER		
A3		
CLIENT NAME		
ADCO		
PROJECT ADDRESS		
179 CALDERWOOD ROAD		
CALDERWOOD NSW 2527		
AUSTRUSS PROJECT NUMBER		
25363		
DRAWING NAME		
150 - PANELS		
DRAWING NUMBER		REV
LGS-A3-200		A




SCAN FOR 3D

WELD ALL


GUSSET

212x2.4mm PURLIN COIL WELDED TO FRONT SIDE

OVERALL HEIGHT = 956

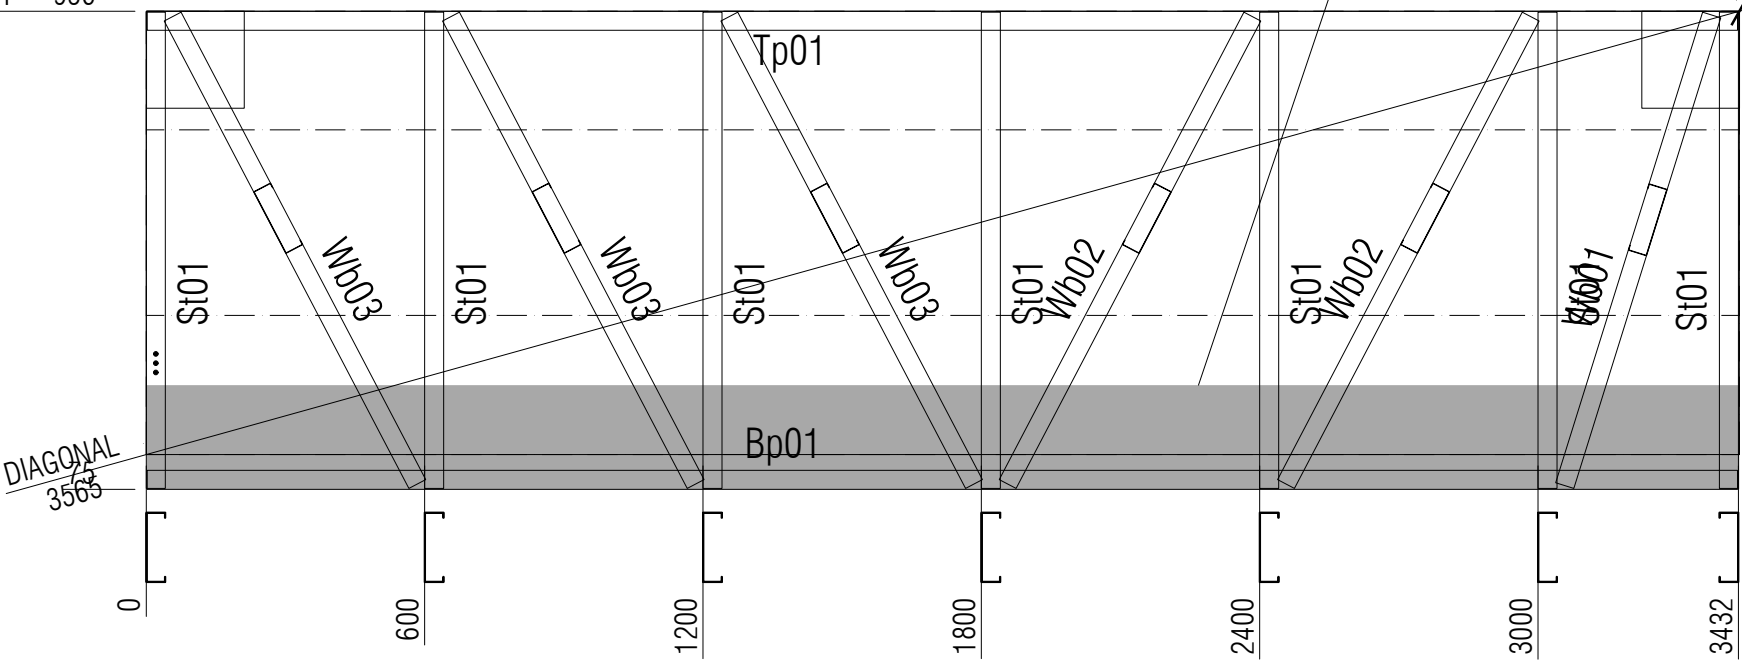

FRAME STICKS NAME	LENGTH	WT	QTY	PROFILE
Tp01	3428	6.3	1	150S41-950-500
Bp01	3428	6.3	1	150S41-950-500
St01	1027	1.9	7	150S41-950-500
Wb01	1063	2.0	1	150S41-950-500
Wb02	1137	2.1	2	150S41-950-500
Wb03	1137	2.1	3	150S41-950-500
TOTAL	20792	38.3	15	

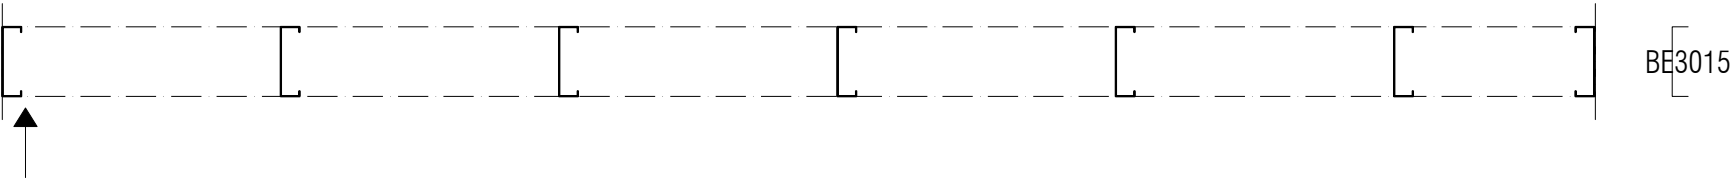

BE3016



DELIVERING SINCE 2003

DRAWN: N.N

PH: 02 4860 1416
OFFICE: 02 4860 1400

REV	DATE	REASON
A	15/09/26	IFC — Issued for construction

AUSTRUSS PROJECT NAME

CALDERWOOD

AUSTRUSS ZONE NUMBER

A3

CLIENT NAME

ADCO

PROJECT ADDRESS

179 CALDERWOOD ROAD
CALDERWOOD NSW 2527

AUSTRUSS PROJECT NUMBER

25363

DRAWING NAME

150 - PANELS

DRAWING NUMBER

LGS-A3-200

REV

A




SCAN FOR 3D

WELD ALL


GUSSET

212x2.4mm PURLIN COIL WELDED TO FRONT SIDE

OVERALL HEIGHT = 956

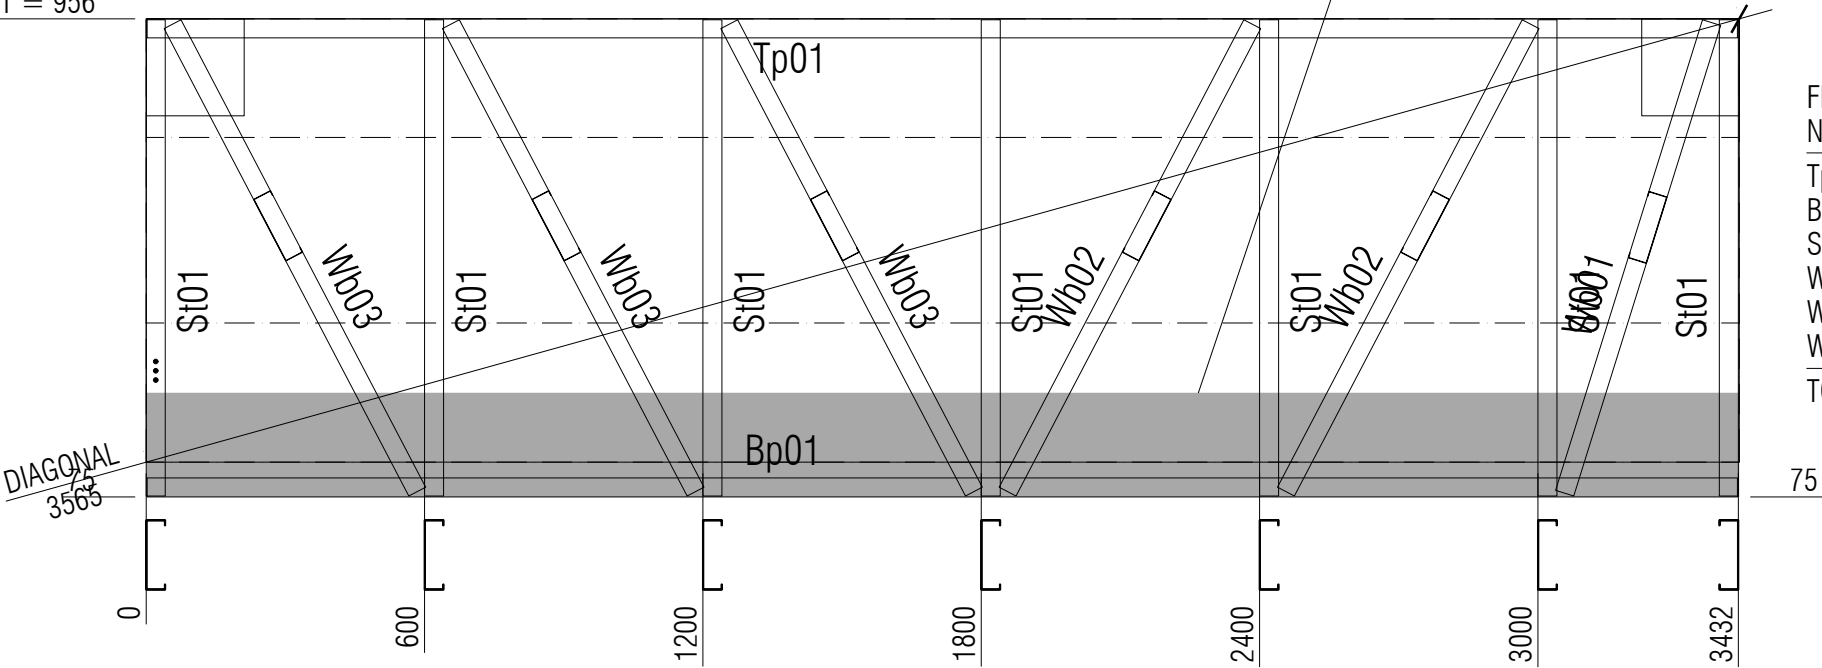

FRAME STICKS NAME	LENGTH	WT	QTY	PROFILE
Tp01	3428	6.3	1	150S41-950-500
Bp01	3428	6.3	1	150S41-950-500
St01	1027	1.9	7	150S41-950-500
Wb01	1063	2.0	1	150S41-950-500
Wb02	1137	2.1	2	150S41-950-500
Wb03	1137	2.1	3	150S41-950-500
TOTAL	20792	38.3	15	

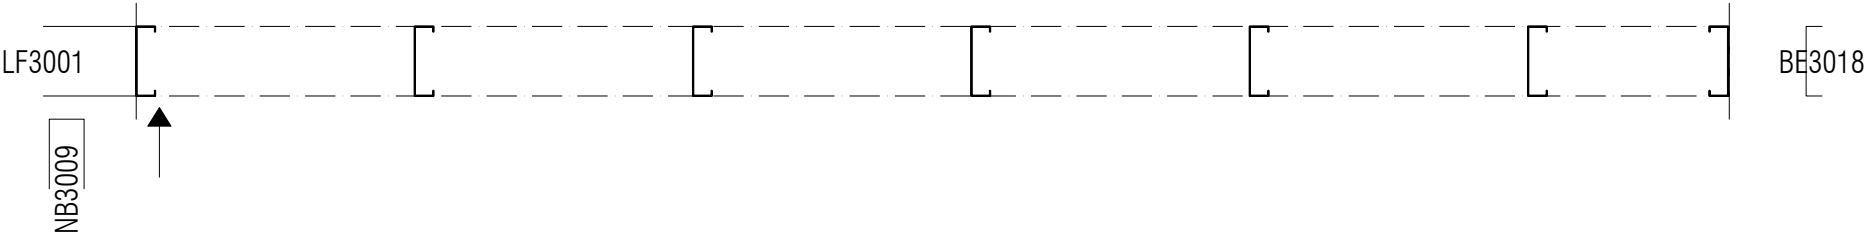

BE3017



DELIVERING SINCE 2003

DRAWN: N.N

PH: 02 4860 1416
OFFICE: 02 4860 1400

REV	DATE	REASON
A	15/09/26	IFC — Issued for construction

AUSTRUSS PROJECT NAME

CALDERWOOD

AUSTRUSS ZONE NUMBER

A3

CLIENT NAME

ADCO

PROJECT ADDRESS

179 CALDERWOOD ROAD
CALDERWOOD NSW 2527

AUSTRUSS PROJECT NUMBER

25363

DRAWING NAME

150 - PANELS

DRAWING NUMBER

LGS-A3-200

REV

A




SCAN FOR 3D

WELD ALL

GUSSET

FRAME STICKS NAME	LENGTH	WT	QTY	PROFILE
Tp01	3428	6.3	1	150S41-950-500
Bp01	3428	6.3	1	150S41-950-500
St01	1027	1.9	7	150S41-950-500
Wb01	1063	2.0	1	150S41-950-500
Wb02	1137	2.1	2	150S41-950-500
Wb03	1137	2.1	3	150S41-950-500
TOTAL	20792	38.3	15	

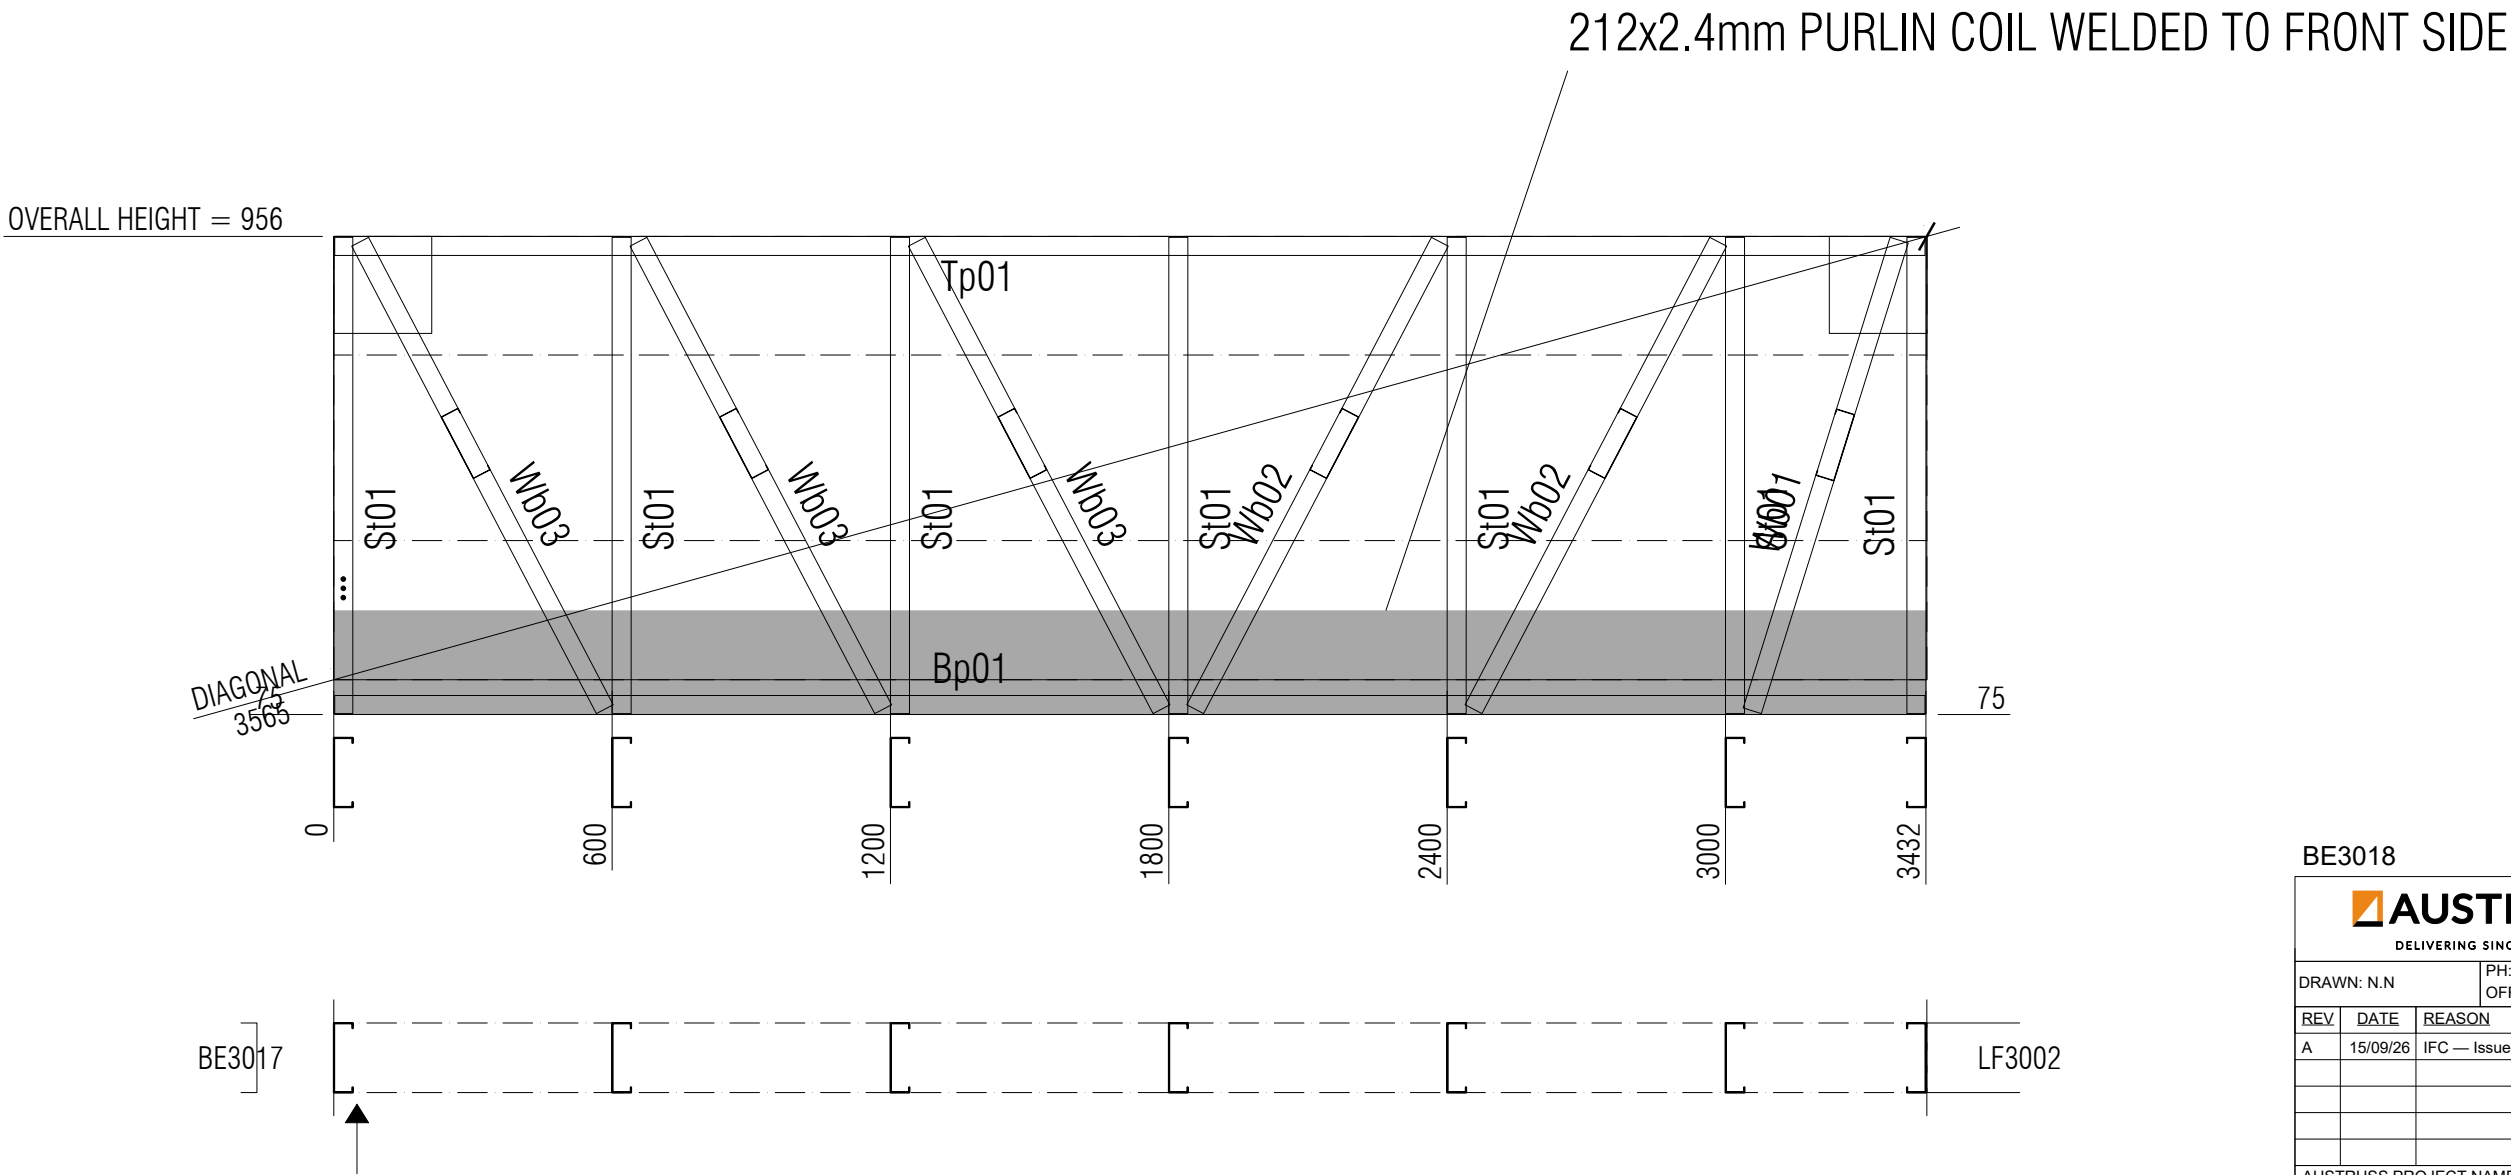

BE3018

**AUSTRUSS**
DELIVERING SINCE 2003

DRAWN: N.N

PH: 02 4860 1416
OFFICE: 02 4860 1400

REV	DATE	REASON
A	15/09/26	IFC — Issued for construction

AUSTRUSS PROJECT NAME
CALDERWOOD

AUSTRUSS ZONE NUMBER
A3

CLIENT NAME
ADCO

PROJECT ADDRESS
**179 CALDERWOOD ROAD
CALDERWOOD NSW 2527**

AUSTRUSS PROJECT NUMBER
25363


DRAWING NAME
150 - PANELS

DRAWING NUMBER
LGS-A3-200

REV
A



SCAN FOR 3D

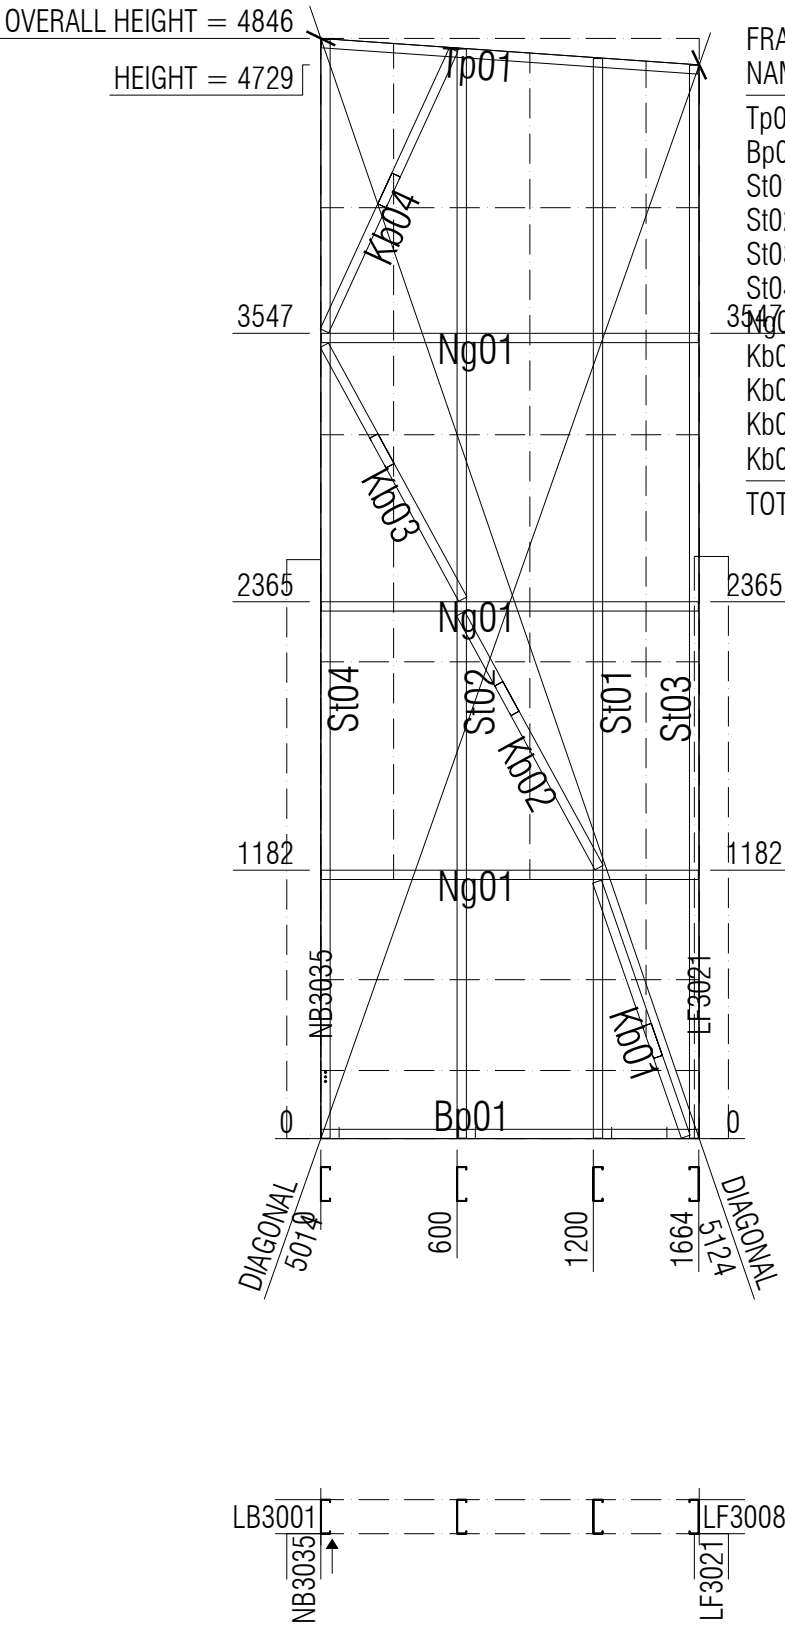

FRAME STICKS				
NAME	LENGTH	WT	QTY	PROFILE
Tp01	1662	3.1	1	150S41-950-500
Bp01	1660	3.1	1	150S41-950-500
St01	4755	8.7	1	150S41-950-500
St02	4797	8.8	1	150S41-950-500
St03	4725	8.7	1	150S41-950-500
St04	4839	8.9	1	150S41-950-500
Ng01	1660	3.1	3	150S41-950-500
Kb01	1189	2.2	1	150S41-950-500
Kb02	1274	2.3	1	150S41-950-500
Kb03	1274	2.3	1	150S41-950-500
Kb04	1362	2.5	1	150S41-950-500
TOTAL	32517	59.8	13	

LB3000



DELIVERING SINCE 2003

DRAWN: N.N

PH: 02 4860 1416
OFFICE: 02 4860 1400

REV	DATE	REASON
A	15/09/26	IFC — Issued for construction

AUSTRUSS PROJECT NAME

CALDERWOOD

AUSTRUSS ZONE NUMBER

A3

CLIENT NAME

ADCO

PROJECT ADDRESS

179 CALDERWOOD ROAD
CALDERWOOD NSW 2527

AUSTRUSS PROJECT NUMBER

25363

DRAWING NAME

150 - PANELS

DRAWING NUMBER


LGS-A3-200

REV

A



SCAN FOR 3D

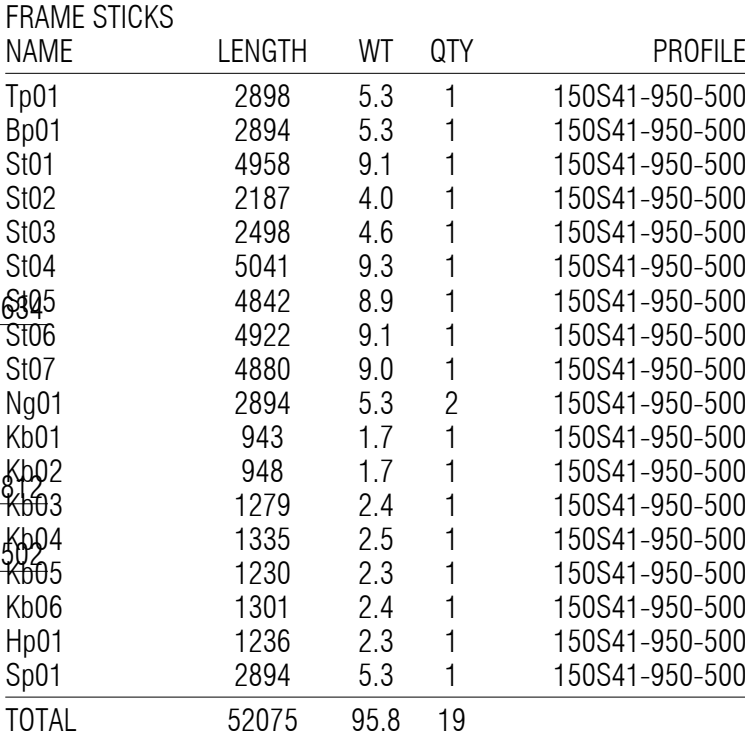

AUSTRUSS
DELIVERING SINCE 2003

DRAWN: N.N

REV	DATE	REASON
A	15/09/26	IFC — Issued for construction

AUSTRUSS PROJECT NAME

CALDERWOOD

AUSTRUSS ZONE NUMBER

CLIENT NAME
ADCO

PROJECT ADDRESS

179 CALDERWOOD ROAD
CALDERWOOD NSW 2527

AUSTRUSS PROJECT NUMBER

25363


DRAWING NAME
150 - PANELS

DRAWING NUMBER
LGS-A3-200

REV
A


SCAN FOR 3D

OVERALL HEIGHT = 3783

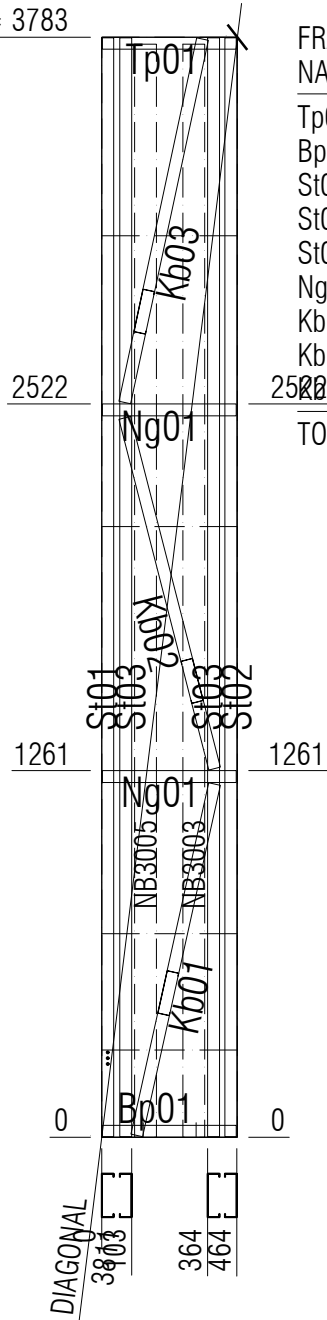

FRAME STICKS

NAME	LENGTH	WT	QTY	PROFILE
Tp01	460	0.8	1	150S41-950-500
Bp01	460	0.8	1	150S41-950-500
St01	3779	7.0	1	150S41-950-500
St02	3779	7.0	1	150S41-950-500
St03	3779	7.0	2	150S41-950-500
Ng01	460	0.8	2	150S41-950-500
Kb01	1237	2.3	1	150S41-950-500
Kb02	1245	2.3	1	150S41-950-500
Kb03	1278	2.4	1	150S41-950-500
TOTAL	20717	38.1	11	

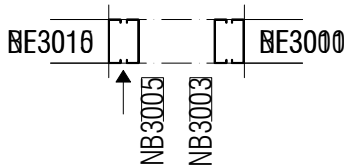

LF3000



DELIVERING SINCE 2003

DRAWN: N.N PH: 02 4860 1416
OFFICE: 02 4860 1400

REV	DATE	REASON
A	15/09/26	IFC — Issued for construction

AUSTRUSS PROJECT NAME
CALDERWOOD

AUSTRUSS ZONE NUMBER
A3

CLIENT NAME
ADCO

PROJECT ADDRESS
**179 CALDERWOOD ROAD
CALDERWOOD NSW 2527**

AUSTRUSS PROJECT NUMBER
25363

DRAWING NAME
150 - PANELS



DRAWING NUMBER
LGS-A3-200

REV
A



SCAN FOR 3D

OVERALL HEIGHT = 3783

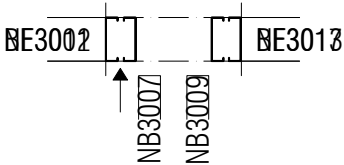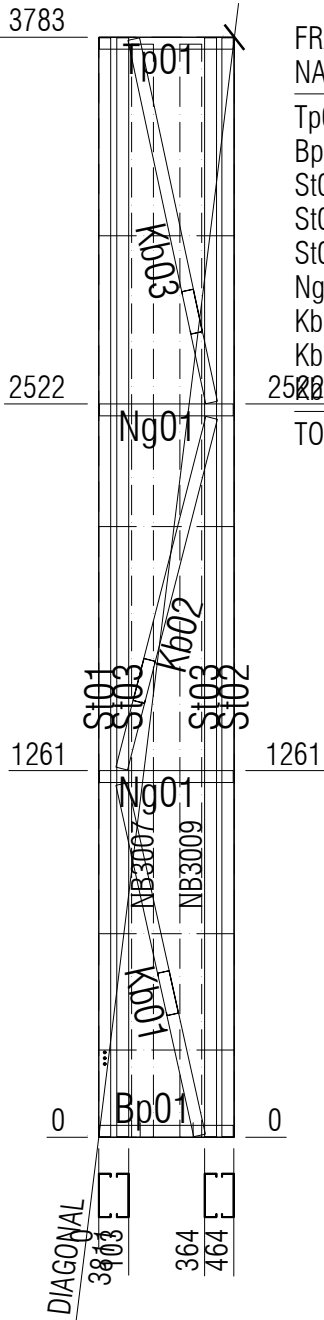

FRAME STICKS

NAME	LENGTH	WT	QTY	PROFILE
Tp01	460	0.8	1	150S41-950-500
Bp01	460	0.8	1	150S41-950-500
St01	3779	7.0	1	150S41-950-500
St02	3779	7.0	1	150S41-950-500
St03	3779	7.0	2	150S41-950-500
Ng01	460	0.8	2	150S41-950-500
Kb01	1237	2.3	1	150S41-950-500
Kb02	1245	2.3	1	150S41-950-500
St03	1278	2.4	1	150S41-950-500
TOTAL	20716	38.1	11	

LF3001



DRAWN: N.N PH: 02 4860 1416
OFFICE: 02 4860 1400

REV	DATE	REASON
A	15/09/26	IFC — Issued for construction

AUSTRUSS PROJECT NAME
CALDERWOOD

AUSTRUSS ZONE NUMBER
A3

CLIENT NAME
ADCO

PROJECT ADDRESS
**179 CALDERWOOD ROAD
CALDERWOOD NSW 2527**

AUSTRUSS PROJECT NUMBER
25363

DRAWING NAME
150 - PANELS


DRAWING NUMBER
LGS-A3-200

REV
A




SCAN FOR 3D

OVERALL HEIGHT = 3783

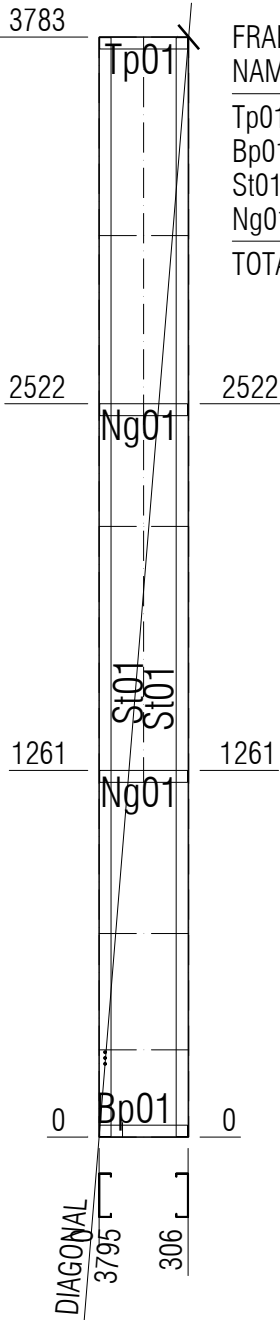

FRAME STICKS				
NAME	LENGTH	WT	QTY	PROFILE
Tp01	302	0.6	1	150S41-950-500
Bp01	302	0.6	1	150S41-950-500
St01	3779	7.0	2	150S41-950-500
Ng01	302	0.6	2	150S41-950-500
TOTAL	8765	16.1	6	

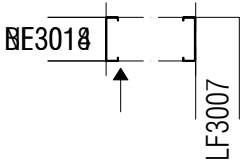

LF3002



DELIVERING SINCE 2003

DRAWN: N.N

PH: 02 4860 1416
OFFICE: 02 4860 1400

REV	DATE	REASON
A	15/09/26	IFC — Issued for construction

AUSTRUSS PROJECT NAME

CALDERWOOD

AUSTRUSS ZONE NUMBER

A3

CLIENT NAME

ADCO

PROJECT ADDRESS

179 CALDERWOOD ROAD
CALDERWOOD NSW 2527

AUSTRUSS PROJECT NUMBER

25363

DRAWING NAME

150 - PANELS

DRAWING NUMBER

LGS-A3-200


REV

A

SCAN FOR 3D



OVERALL HEIGHT = 3783

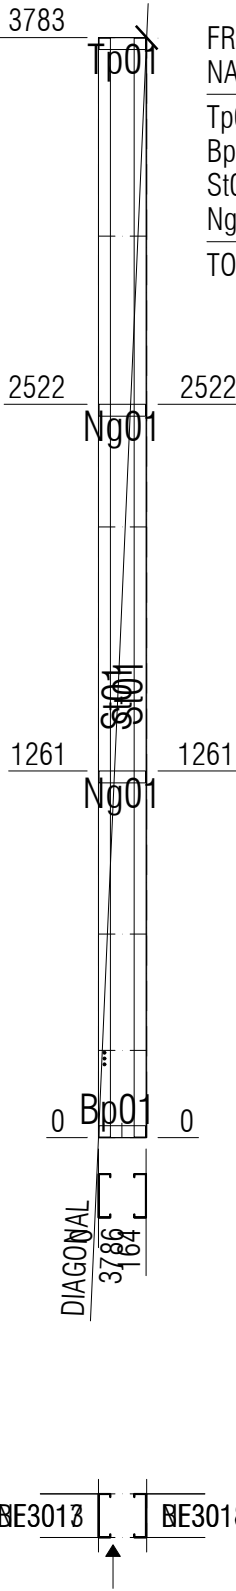

FRAME STICKS					
NAME	LENGTH	WT	QTY	PROFILE	
Tp01	160	0.3	1	150S41-950-500	
Bp01	160	0.3	1	150S41-950-500	
St01	3779	7.0	2	150S41-950-500	
Ng01	160	0.3	2	150S41-950-500	
TOTAL	8196	15.1	6		

LF3003

AUSTRUSS

DELIVERING SINCE 2003

DRAWN: N.N

PH: 02 4860 1416
OFFICE: 02 4860 1400

REV	DATE	REASON
A	15/09/26	IFC — Issued for construction

AUSTRUSS PROJECT NAME

CALDERWOOD

AUSTRUSS ZONE NUMBER

A3

CLIENT NAME

ADCO

PROJECT ADDRESS

179 CALDERWOOD ROAD
CALDERWOOD NSW 2527

AUSTRUSS PROJECT NUMBER

25363

DRAWING NAME

150 - PANELS

DRAWING NUMBER


LGS-A3-200

REV

A

SCAN FOR 3D

OVERALL HEIGHT = 3783

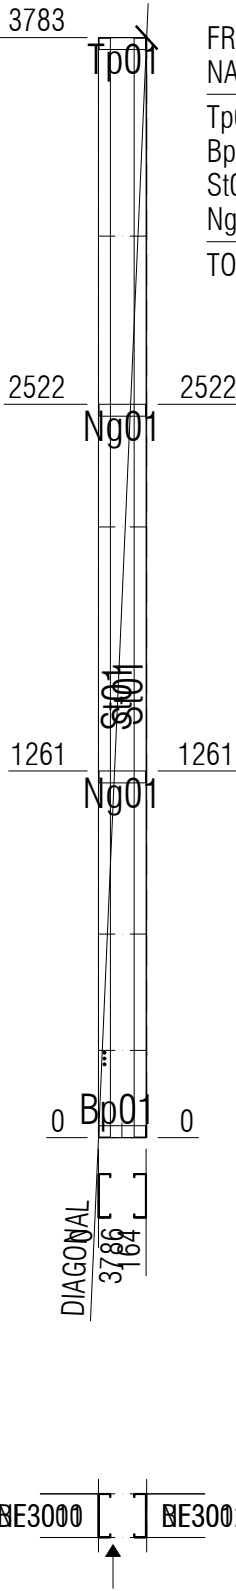

FRAME STICKS					
NAME	LENGTH	WT	QTY	PROFILE	
Tp01	160	0.3	1	150S41-950-500	
Bp01	160	0.3	1	150S41-950-500	
St01	3779	7.0	2	150S41-950-500	
Ng01	160	0.3	2	150S41-950-500	
TOTAL	8196	15.1	6		

LF3004



DELIVERING SINCE 2003

DRAWN: N.N

PH: 02 4860 1416
OFFICE: 02 4860 1400

REV	DATE	REASON
A	15/09/26	IFC — Issued for construction

AUSTRUSS PROJECT NAME

CALDERWOOD

AUSTRUSS ZONE NUMBER

A3

CLIENT NAME

ADCO

PROJECT ADDRESS

179 CALDERWOOD ROAD
CALDERWOOD NSW 2527

AUSTRUSS PROJECT NUMBER

25363

DRAWING NAME

150 - PANELS

DRAWING NUMBER

LGS-A3-200


REV

A

SCAN FOR 3D



OVERALL HEIGHT = 3783

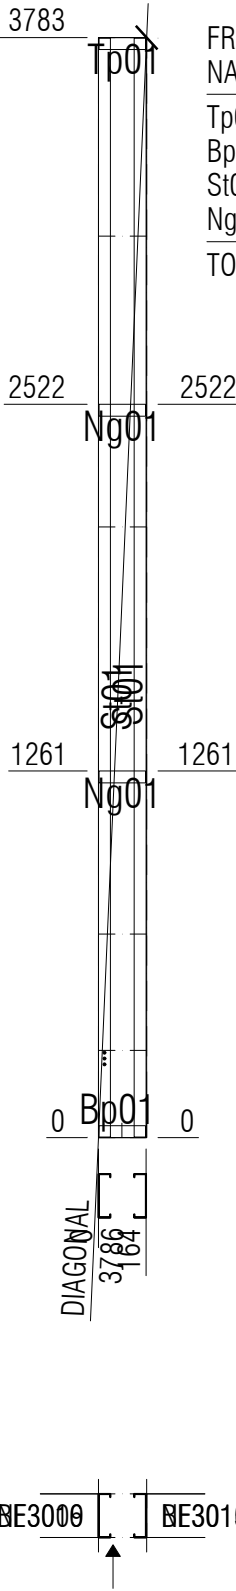

FRAME STICKS					
NAME	LENGTH	WT	QTY	PROFILE	
Tp01	160	0.3	1	150S41-950-500	
Bp01	160	0.3	1	150S41-950-500	
St01	3779	7.0	2	150S41-950-500	
Ng01	160	0.3	2	150S41-950-500	
TOTAL	8196	15.1	6		

LF3005

AUSTRUSS

DELIVERING SINCE 2003

DRAWN: N.N

PH: 02 4860 1416
OFFICE: 02 4860 1400

REV	DATE	REASON
A	15/09/26	IFC — Issued for construction

AUSTRUSS PROJECT NAME

CALDERWOOD

AUSTRUSS ZONE NUMBER

A3

CLIENT NAME

ADCO

PROJECT ADDRESS

179 CALDERWOOD ROAD
CALDERWOOD NSW 2527

AUSTRUSS PROJECT NUMBER

25363

DRAWING NAME

150 - PANELS

DRAWING NUMBER


LGS-A3-200

REV

A

SCAN FOR 3D

OVERALL HEIGHT = 3485

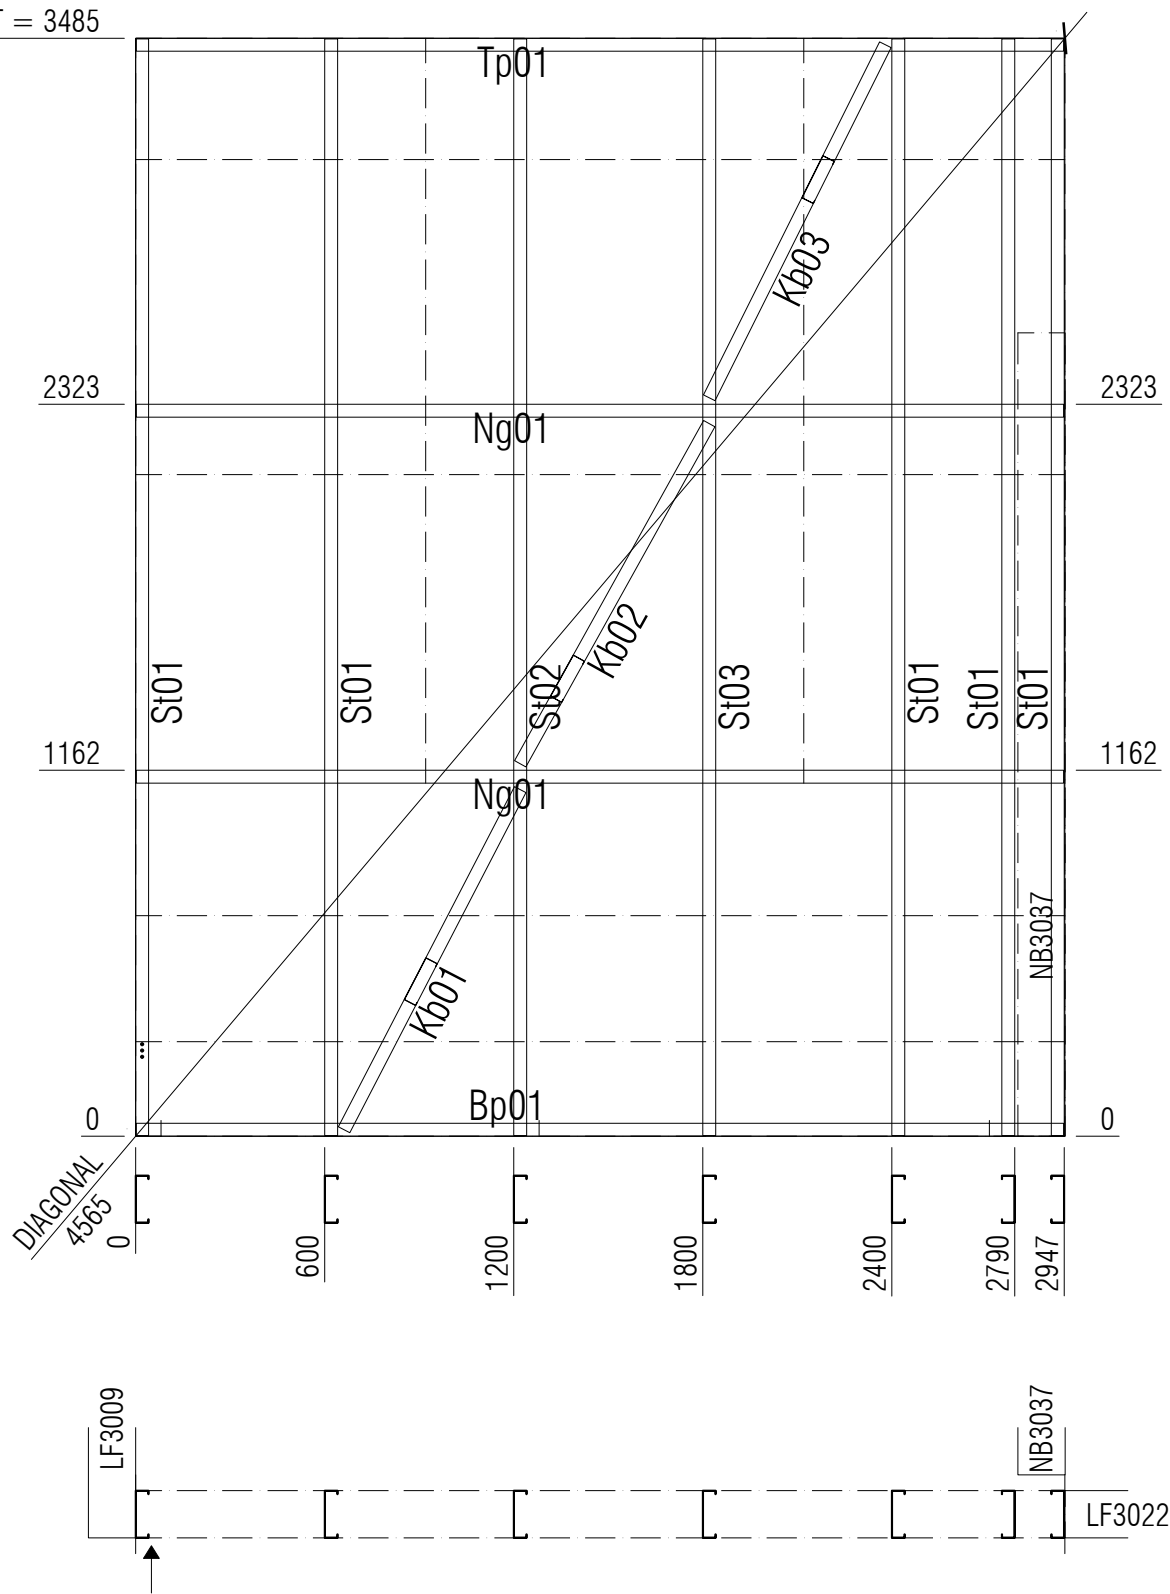

FRAME STICKS NAME	LENGTH	WT	QTY	PROFILE
Tp01	2943	5.4	1	150S41-950-500
Bp01	2943	5.4	1	150S41-950-500
St01	3481	6.4	5	150S41-950-500
St02	3481	6.4	1	150S41-950-500
St03	3481	6.4	1	150S41-950-500
Ng01	2943	5.4	2	150S41-950-500
Kb01	1216	2.2	1	150S41-950-500
Kb02	1235	2.3	1	150S41-950-500
Kb03	1252	2.3	1	150S41-950-500
TOTAL	39843	73.3	14	

LF3006

AUSTRUSS

DELIVERING SINCE 2003

DRAWN: N.N

PH: 02 4860 1416
OFFICE: 02 4860 1400

REV	DATE	REASON
A	15/09/26	IFC — Issued for construction

AUSTRUSS PROJECT NAME

CALDERWOOD

AUSTRUSS ZONE NUMBER

A3

CLIENT NAME

ADCO

PROJECT ADDRESS

179 CALDERWOOD ROAD
CALDERWOOD NSW 2527

AUSTRUSS PROJECT NUMBER

25363

DRAWING NAME

150 - PANELS


DRAWING NUMBER

LGS-A3-200

REV

A

SCAN FOR 3D

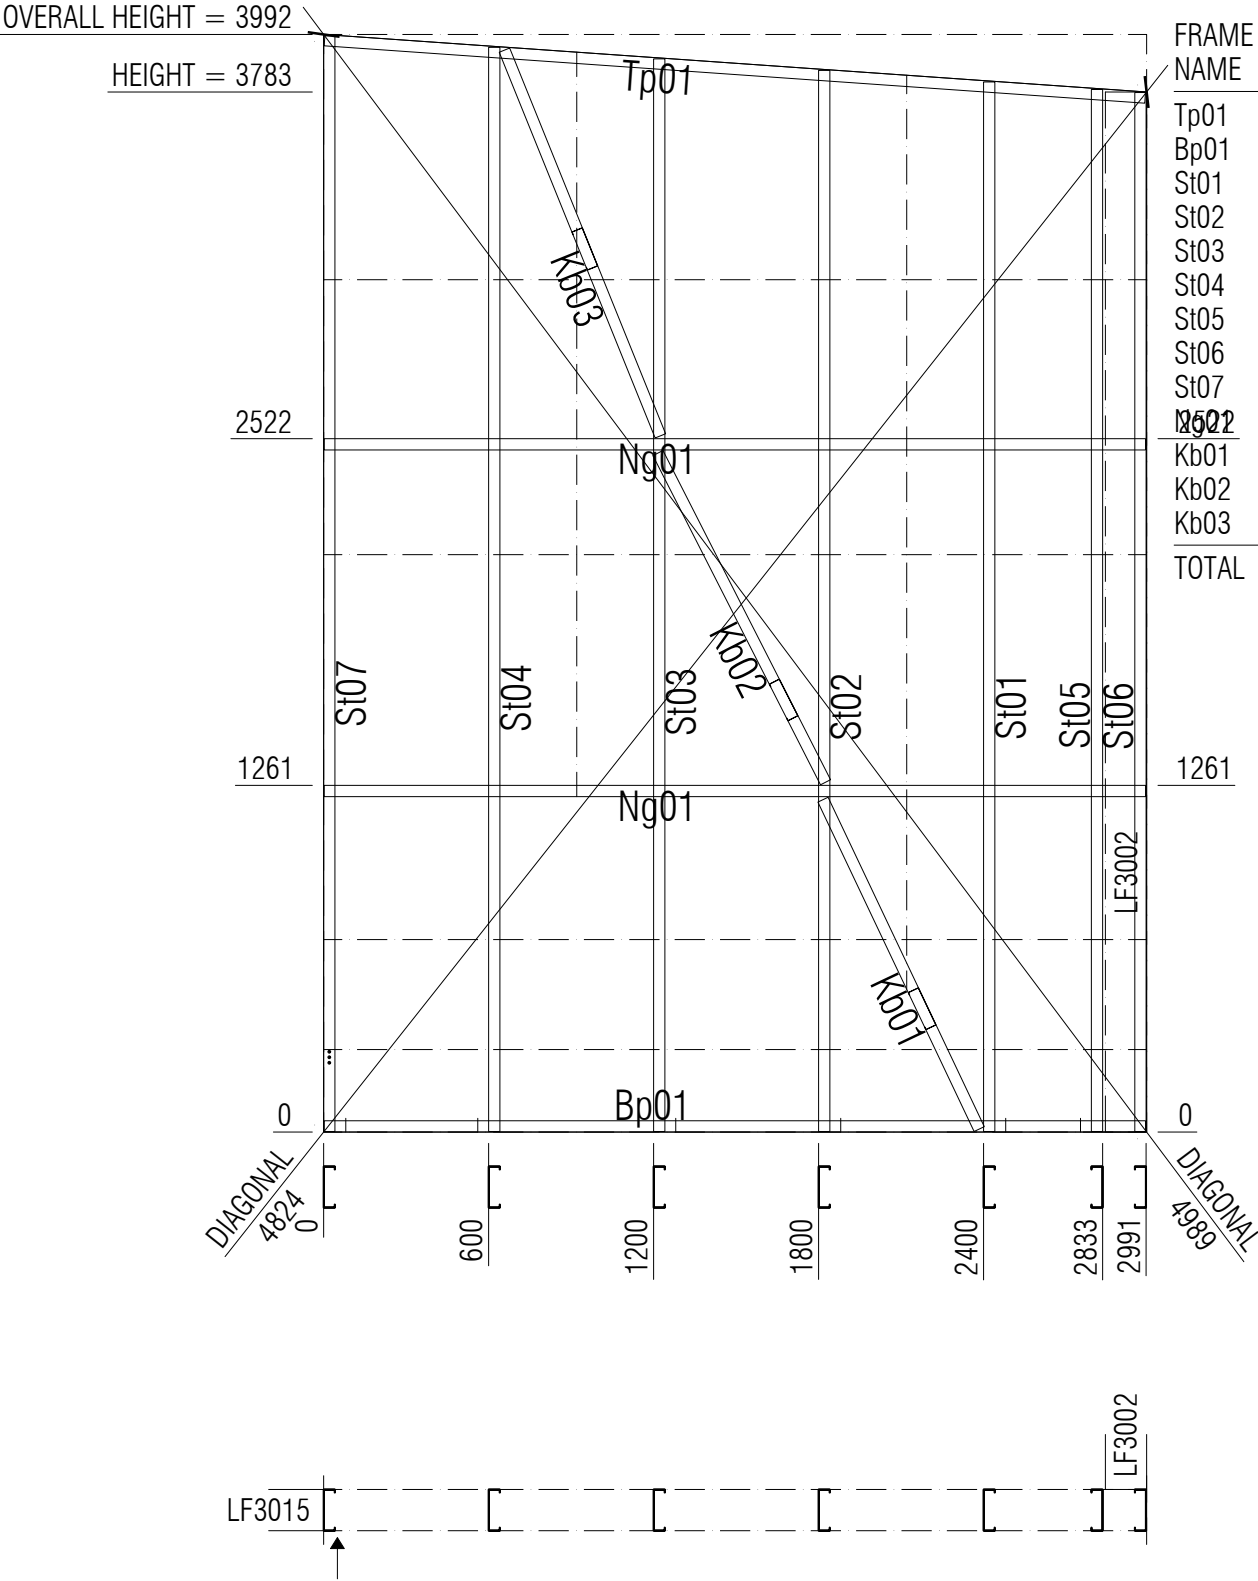

FRAME STICKS				
NAME	LENGTH	WT	QTY	PROFILE
Tp01	2991	5.5	1	150S41-950-500
Bp01	2987	5.5	1	150S41-950-500
St01	3817	7.0	1	150S41-950-500
St02	3859	7.1	1	150S41-950-500
St03	3901	7.2	1	150S41-950-500
St04	3943	7.3	1	150S41-950-500
St05	3790	7.0	1	150S41-950-500
St06	3779	7.0	1	150S41-950-500
St07	3985	7.3	1	150S41-950-500
Ng01	2987	5.5	2	150S41-950-500
Kb01	1326	2.4	1	150S41-950-500
Kb02	1343	2.5	1	150S41-950-500
Kb03	1513	2.8	1	150S41-950-500
TOTAL	43210	79.5	14	

LF3007



DELIVERING SINCE 2003

DRAWN: N.N

PH: 02 4860 1416
OFFICE: 02 4860 1400

REV	DATE	REASON
A	15/09/26	IFC — Issued for construction

AUSTRUSS PROJECT NAME

CALDERWOOD

AUSTRUSS ZONE NUMBER

A3

CLIENT NAME

ADCO

PROJECT ADDRESS

179 CALDERWOOD ROAD
CALDERWOOD NSW 2527

AUSTRUSS PROJECT NUMBER

25363

DRAWING NAME

150 - PANELS

DRAWING NUMBER


LGS-A3-200

REV

A



SCAN FOR 3D

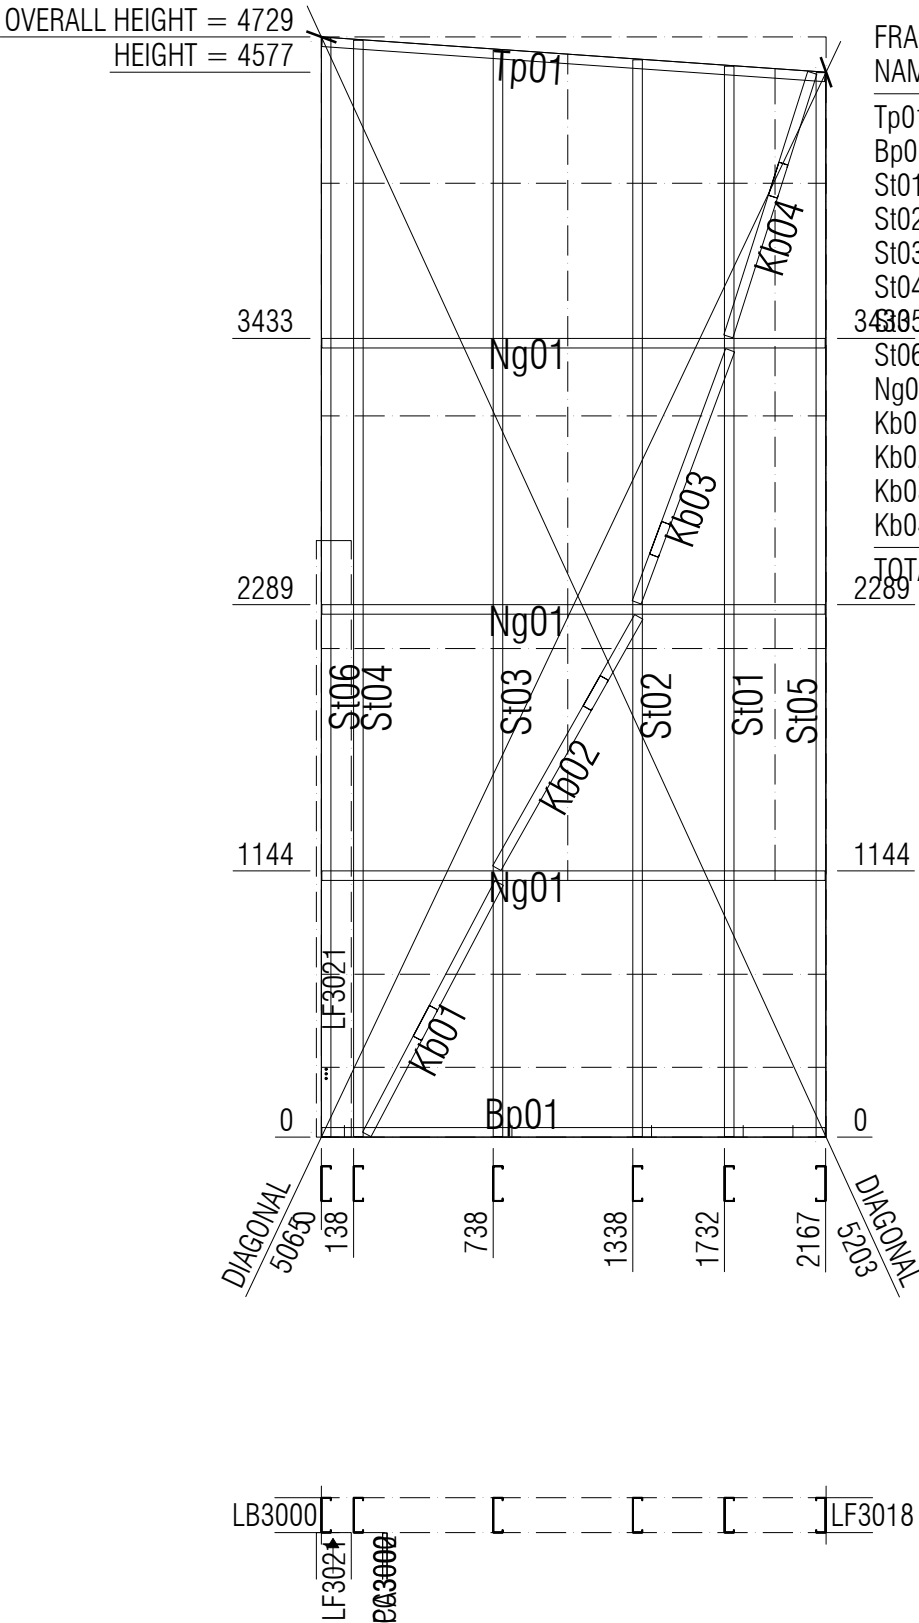

FRAME STICKS				
NAME	LENGTH	WT	QTY	PROFILE
Tp01	2166	4.0	1	150S41-950-500
Bp01	2163	4.0	1	150S41-950-500
St01	4601	8.5	1	150S41-950-500
St02	4629	8.5	1	150S41-950-500
St03	4671	8.6	1	150S41-950-500
St04	4712	8.7	1	150S41-950-500
St05	4573	8.4	1	150S41-950-500
St06	4722	8.7	1	150S41-950-500
Ng01	2163	4.0	3	150S41-950-500
Kb01	1221	2.2	1	150S41-950-500
Kb02	1240	2.3	1	150S41-950-500
Kb03	1156	2.1	1	150S41-950-500
Kb04	1189	2.2	1	150S41-950-500
TOTAL	43533	80.1	15	

LF3008



DELIVERING SINCE 2003

DRAWN: N.N

PH: 02 4860 1416
OFFICE: 02 4860 1400

REV	DATE	REASON
A	15/09/26	IFC — Issued for construction

AUSTRUSS PROJECT NAME

CALDERWOOD

AUSTRUSS ZONE NUMBER

A3

CLIENT NAME

ADCO

PROJECT ADDRESS

179 CALDERWOOD ROAD
CALDERWOOD NSW 2527

AUSTRUSS PROJECT NUMBER

25363

DRAWING NAME

WALL LAYOUT

DRAWING NUMBER

LGS-A3-110


REV

A

SCAN FOR 3D



DOUBLE SCREW

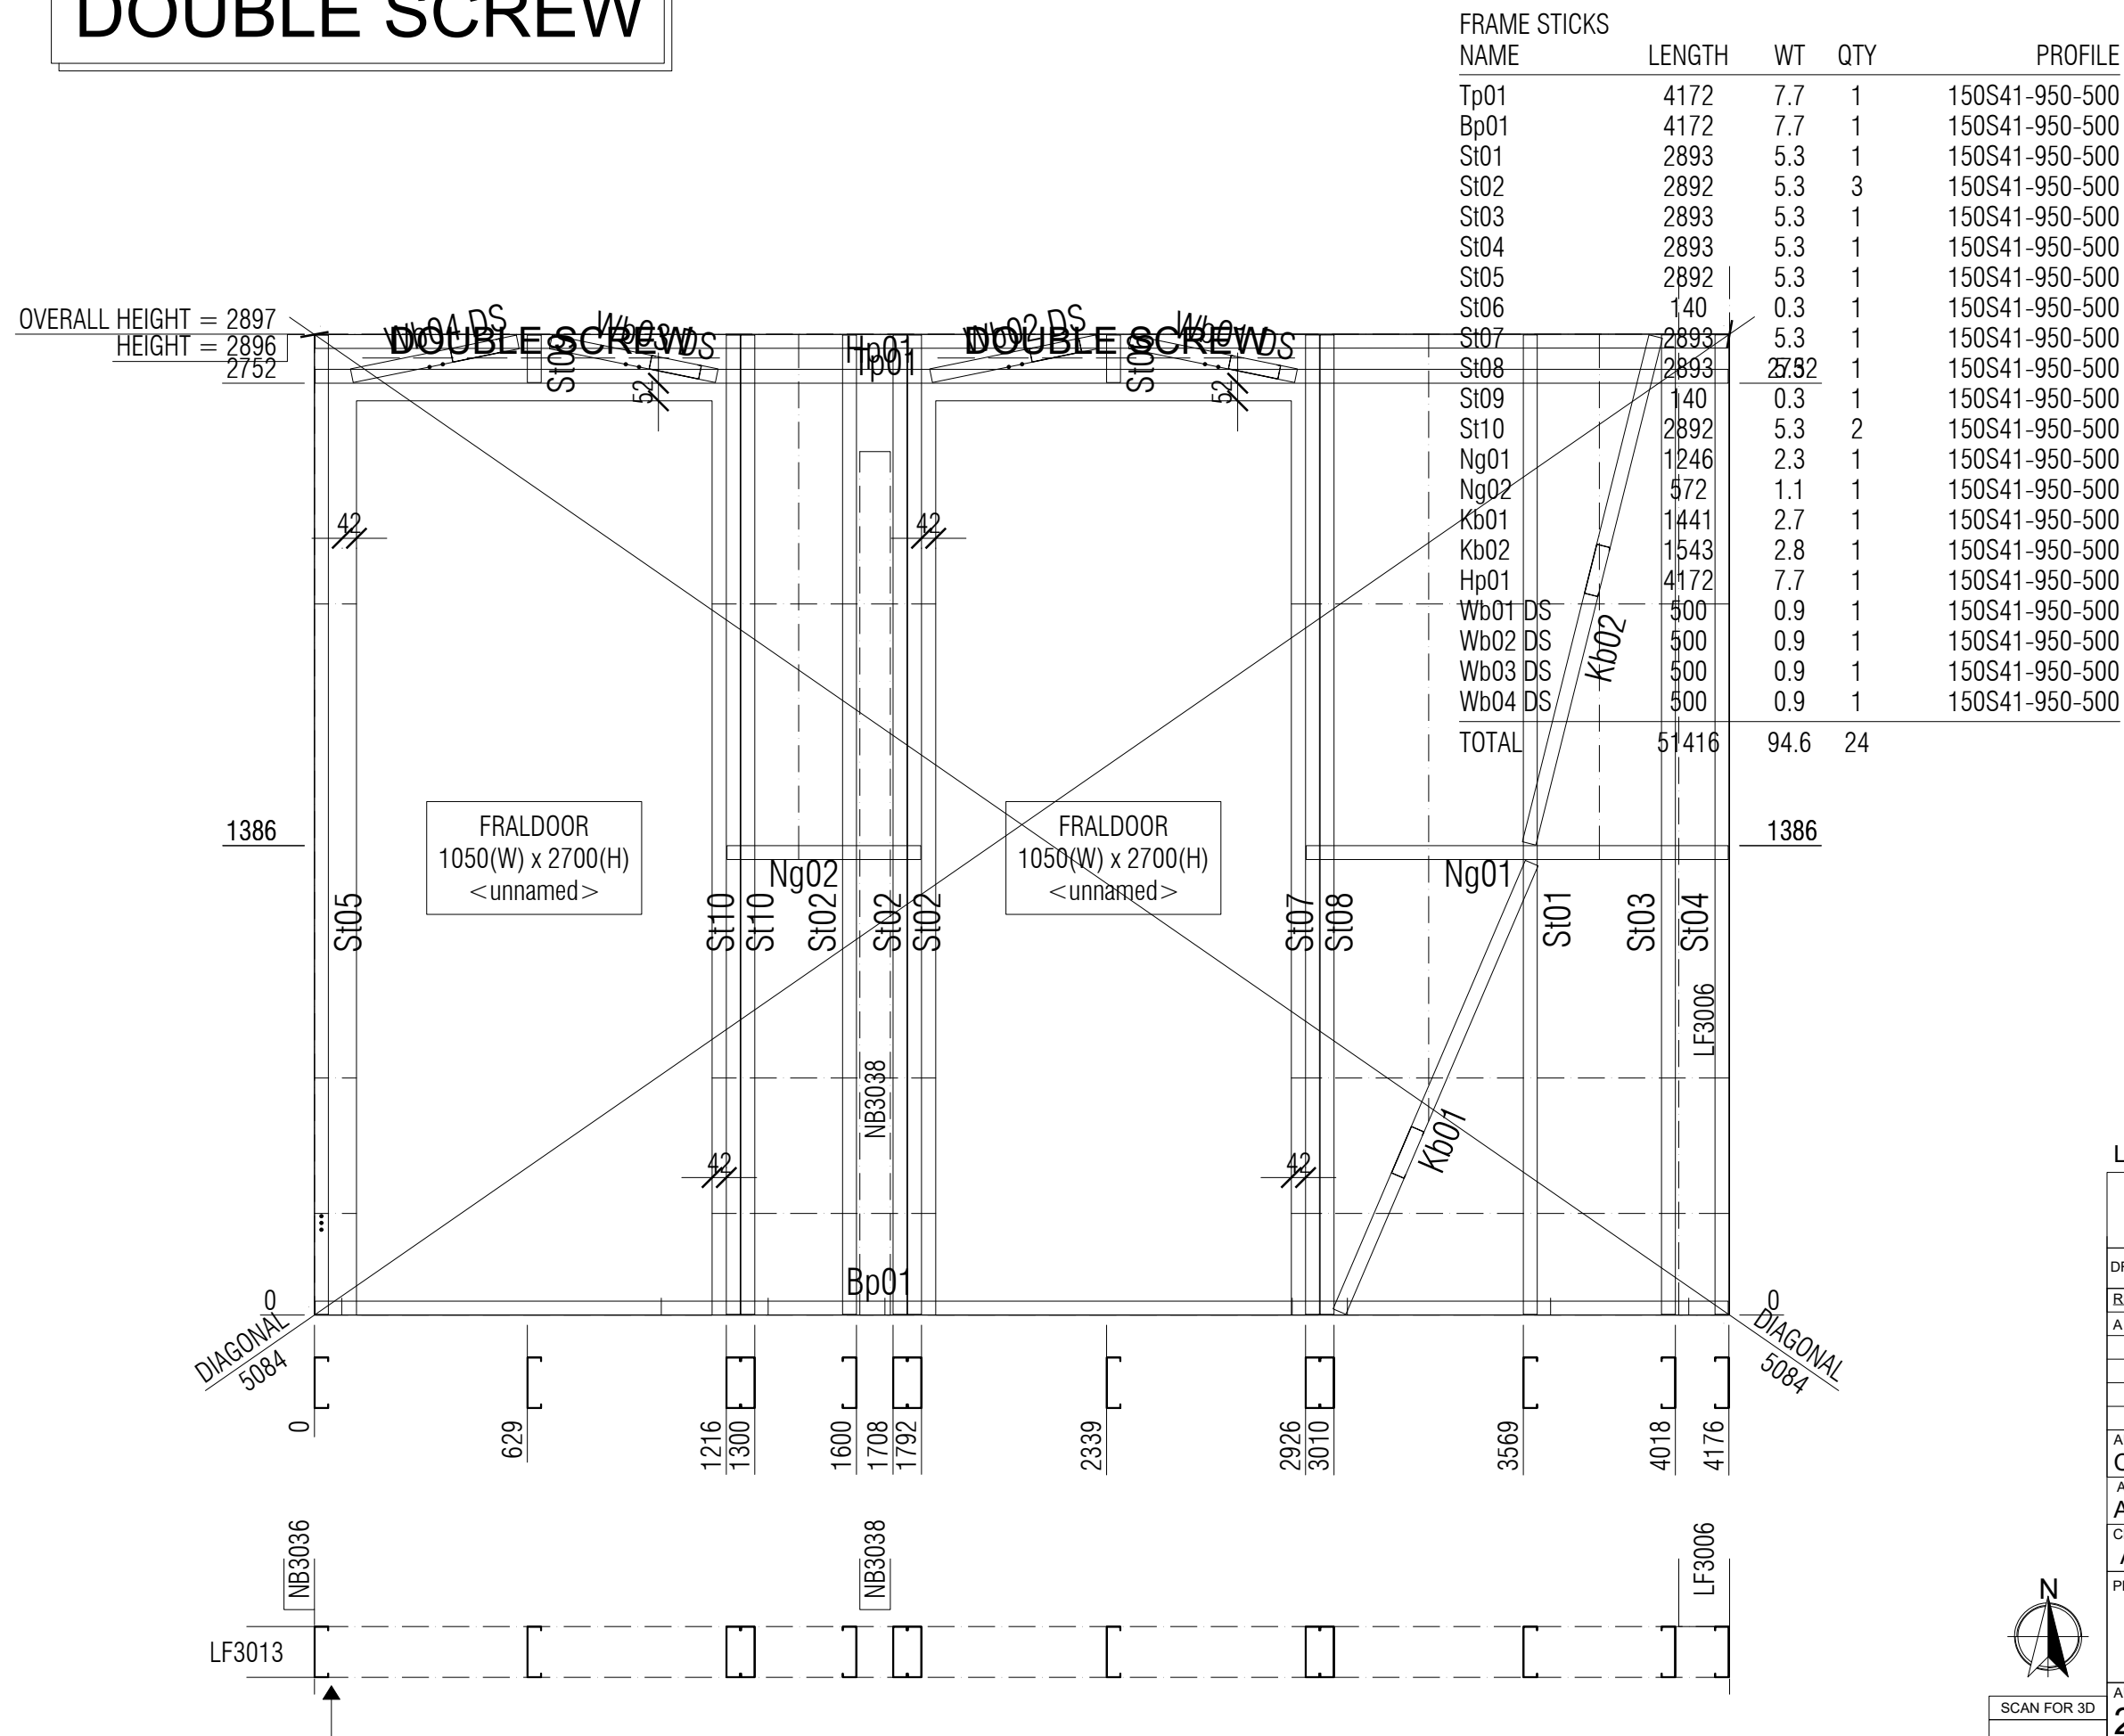

LF3009



DELIVERING SINCE 2003

DRAWN: N.N

PH: 02 4860 1416
OFFICE: 02 4860 1400

REV	DATE	REASON
A	15/09/26	IFC — Issued for construction

AUSTRUSS PROJECT NAME

CALDERWOOD

AUSTRUSS ZONE NUMBER

A3

CLIENT NAME

ADCO

PROJECT ADDRESS

179 CALDERWOOD ROAD
CALDERWOOD NSW 2527

AUSTRUSS PROJECT NUMBER

25363

DRAWING NAME

150 - PANELS

DRAWING NUMBER


LGS-A3-200

REV

A



SCAN FOR 3D

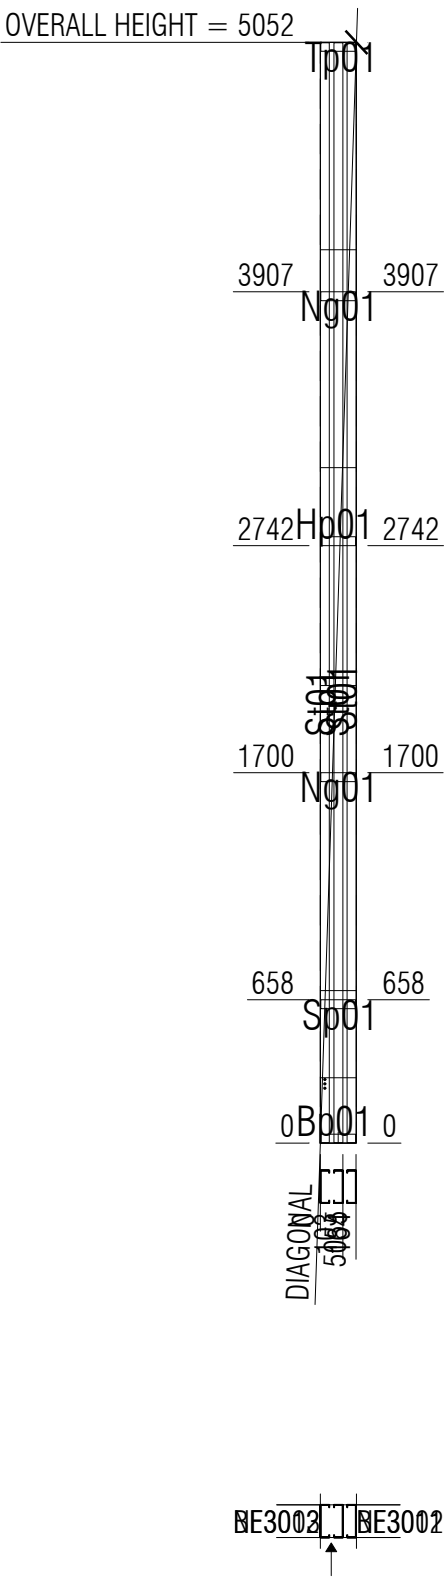

FRAME STICKS NAME	LENGTH	WT	QTY	PROFILE
Tp01	160	0.3	1	150S41-950-500
Bp01	160	0.3	1	150S41-950-500
St01	5048	9.3	3	150S41-950-500
Ng01	160	0.3	2	150S41-950-500
Hp01	160	0.3	1	150S41-950-500
Sp01	160	0.3	1	150S41-950-500
TOTAL	16102	29.6	9	

LF3010



AUSTRUSS

DELIVERING SINCE 2003

DRAWN: N.N

PH: 02 4860 1416
OFFICE: 02 4860 1400

REV	DATE	REASON
A	15/09/26	IFC — Issued for construction

AUSTRUSS PROJECT NAME

CALDERWOOD

AUSTRUSS ZONE NUMBER

A3

CLIENT NAME

ADCO

PROJECT ADDRESS

179 CALDERWOOD ROAD
CALDERWOOD NSW 2527

AUSTRUSS PROJECT NUMBER

25363

DRAWING NAME

150 - PANELS

DRAWING NUMBER


LGS-A3-200

REV

A

SCAN FOR 3D



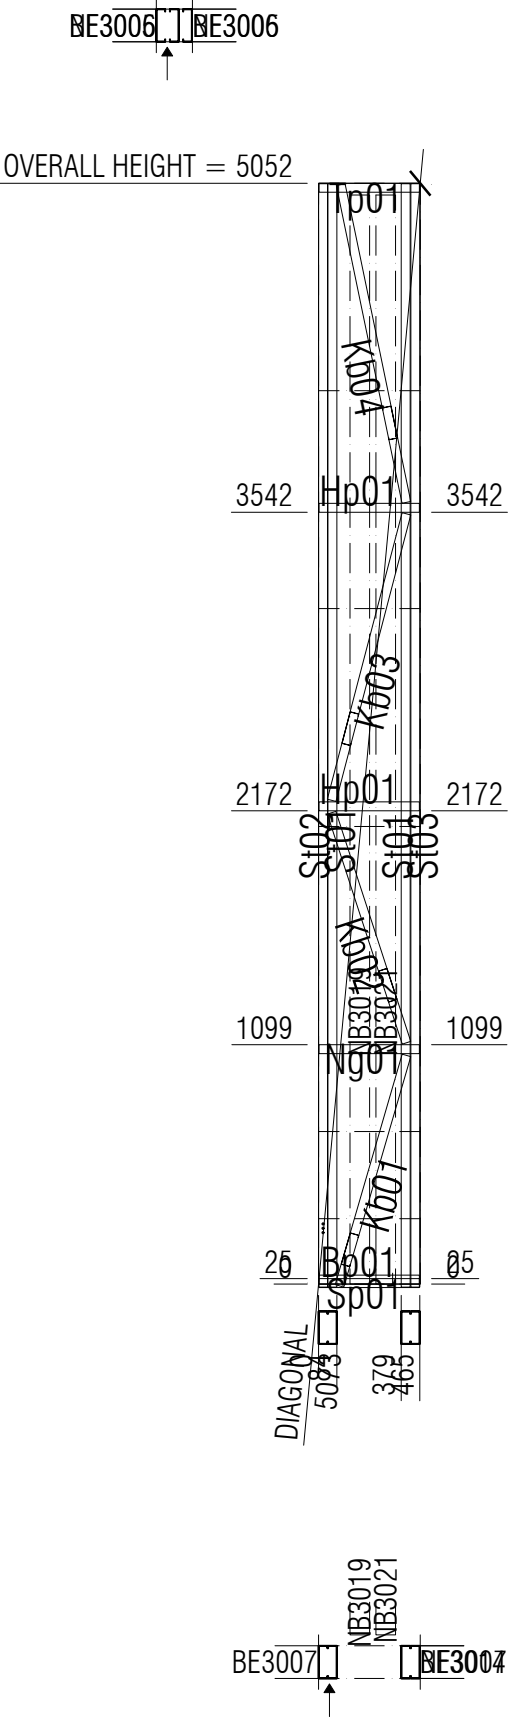

FRAME STICKS				
NAME	LENGTH	WT	QTY	PROFILE
Tp01	461	0.8	1	150S41-950-500
Bp01	461	0.8	1	150S41-950-500
St01	5064	9.3	2	150S41-950-500
St02	5064	9.3	1	150S41-950-500
St03	5064	9.3	1	150S41-950-500
Ng01	461	0.8	1	150S41-950-500
Kb01	1101	2.0	1	150S41-950-500
Kb02	1110	2.0	1	150S41-950-500
Kb03	1359	2.5	1	150S41-950-500
Kb04	1489	2.7	1	150S41-950-500
Hp01	461	0.8	2	150S41-950-500
Sp01	461	0.8	1	150S41-950-500
TOTAL	28078	51.7	14	

SCAN FOR 3D


DELIVERING SINCE 2003

DRAWN: N.N 600 PH: 02 4888 1416 OFFICE: 02 4860 1400


REV	DATE	REASON
A	15/09/26	IFC — Issued for construction

AUSTRUSS PROJECT NAME	CALDERWOOD
AUSTRUSS ZONE NUMBER	A3
CLIENT NAME	ADCO
PROJECT ADDRESS	179 CALDERWOOD ROAD CALDERWOOD NSW 2527
AUSTRUSS PROJECT NUMBER	25363
DRAWING NAME	150 - PANELS
DRAWING NUMBER	LGS-A3-200
REV	A

OVERALL HEIGHT = 5052

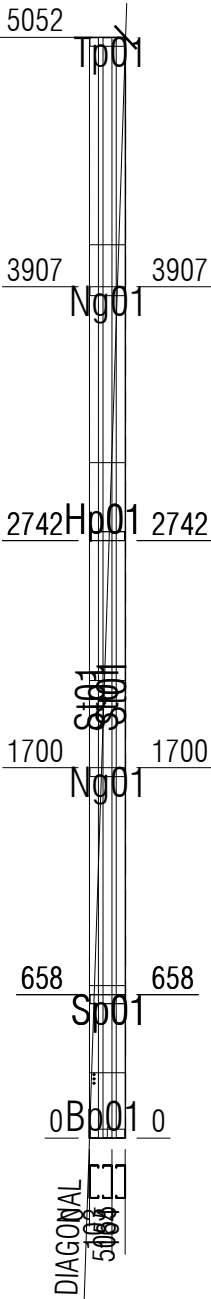


OVERALL HEIGHT = 5052

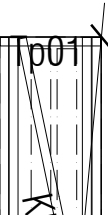

FRAME STICKS				
NAME	LENGTH	WT	QTY	PROFILE
Tp01	160	0.3	1	150S41-950-500
Bp01	160	0.3	1	150S41-950-500
St01	5048	9.3	3	150S41-950-500
Ng01	160	0.3	2	150S41-950-500
Hp01	160	0.3	2	150S41-950-500
Sp01	160	0.3	2	150S41-950-500
TOTAL	16421	30.2	11	

FRAME STICKS				
NAME	LENGTH	WT	QTY	PROFILE
Tp01	461	0.8	1	150S41-950-500
Bp01	461	0.8	1	150S41-950-500
St01	5048	9.3	3	150S41-950-500
Ng01	160	0.3	2	150S41-950-500
Hp01	160	0.3	2	150S41-950-500
Sp01	160	0.3	2	150S41-950-500
TOTAL	16421	30.2	11	

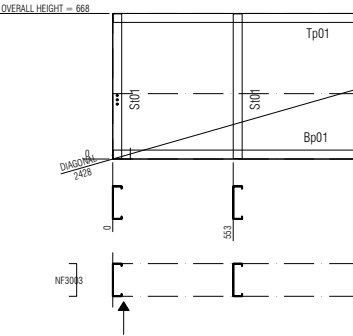

OVERALL HEIGHT = 3993

HEIGHT = 3759



SCAN FOR 3D



DELIVERING SINCE 2003

DRAWN: N.N

PH: 02 4860 5566

OFFICE: 02 4860 1400

REV	DATE	REASON
A	15/09/26	IFC — Issued for construction

AUSTRUSS PROJECT NAME

CALDERWOOD

AUSTRUSS ZONE NUMBER

A3

CLIENT NAME

ADCO

PROJECT ADDRESS

179 CALDERWOOD ROAD

CALDERWOOD NSW 2527

AUSTRUSS PROJECT NUMBER

25363

DRAWING NAME

150 - PANELS

DRAWING NUMBER


LGS-A3-200

REV

A

DOUBLE SCREW

FRAME STICKS				
NAME	LENGTH	WT	QTY	PROFILE
Tp01	3100	5.7	1	150S41-950-500
Bp01	3100	5.7	1	150S41-950-500
St01	2892	5.3	11	150S41-950-500
St02	140	0.3	2	150S41-950-500
Ng01	433	0.8	1	150S41-950-500
Ng02	242	0.4	1	150S41-950-500
Ng03	449	0.8	1	150S41-950-500
Hp01	3100	5.7	1	150S41-950-500
Wb01 DS	430	0.8	2	150S41-950-500
Wb02 DS	430	0.8	2	150S41-950-500
TOTAL	44233	81.4	23	

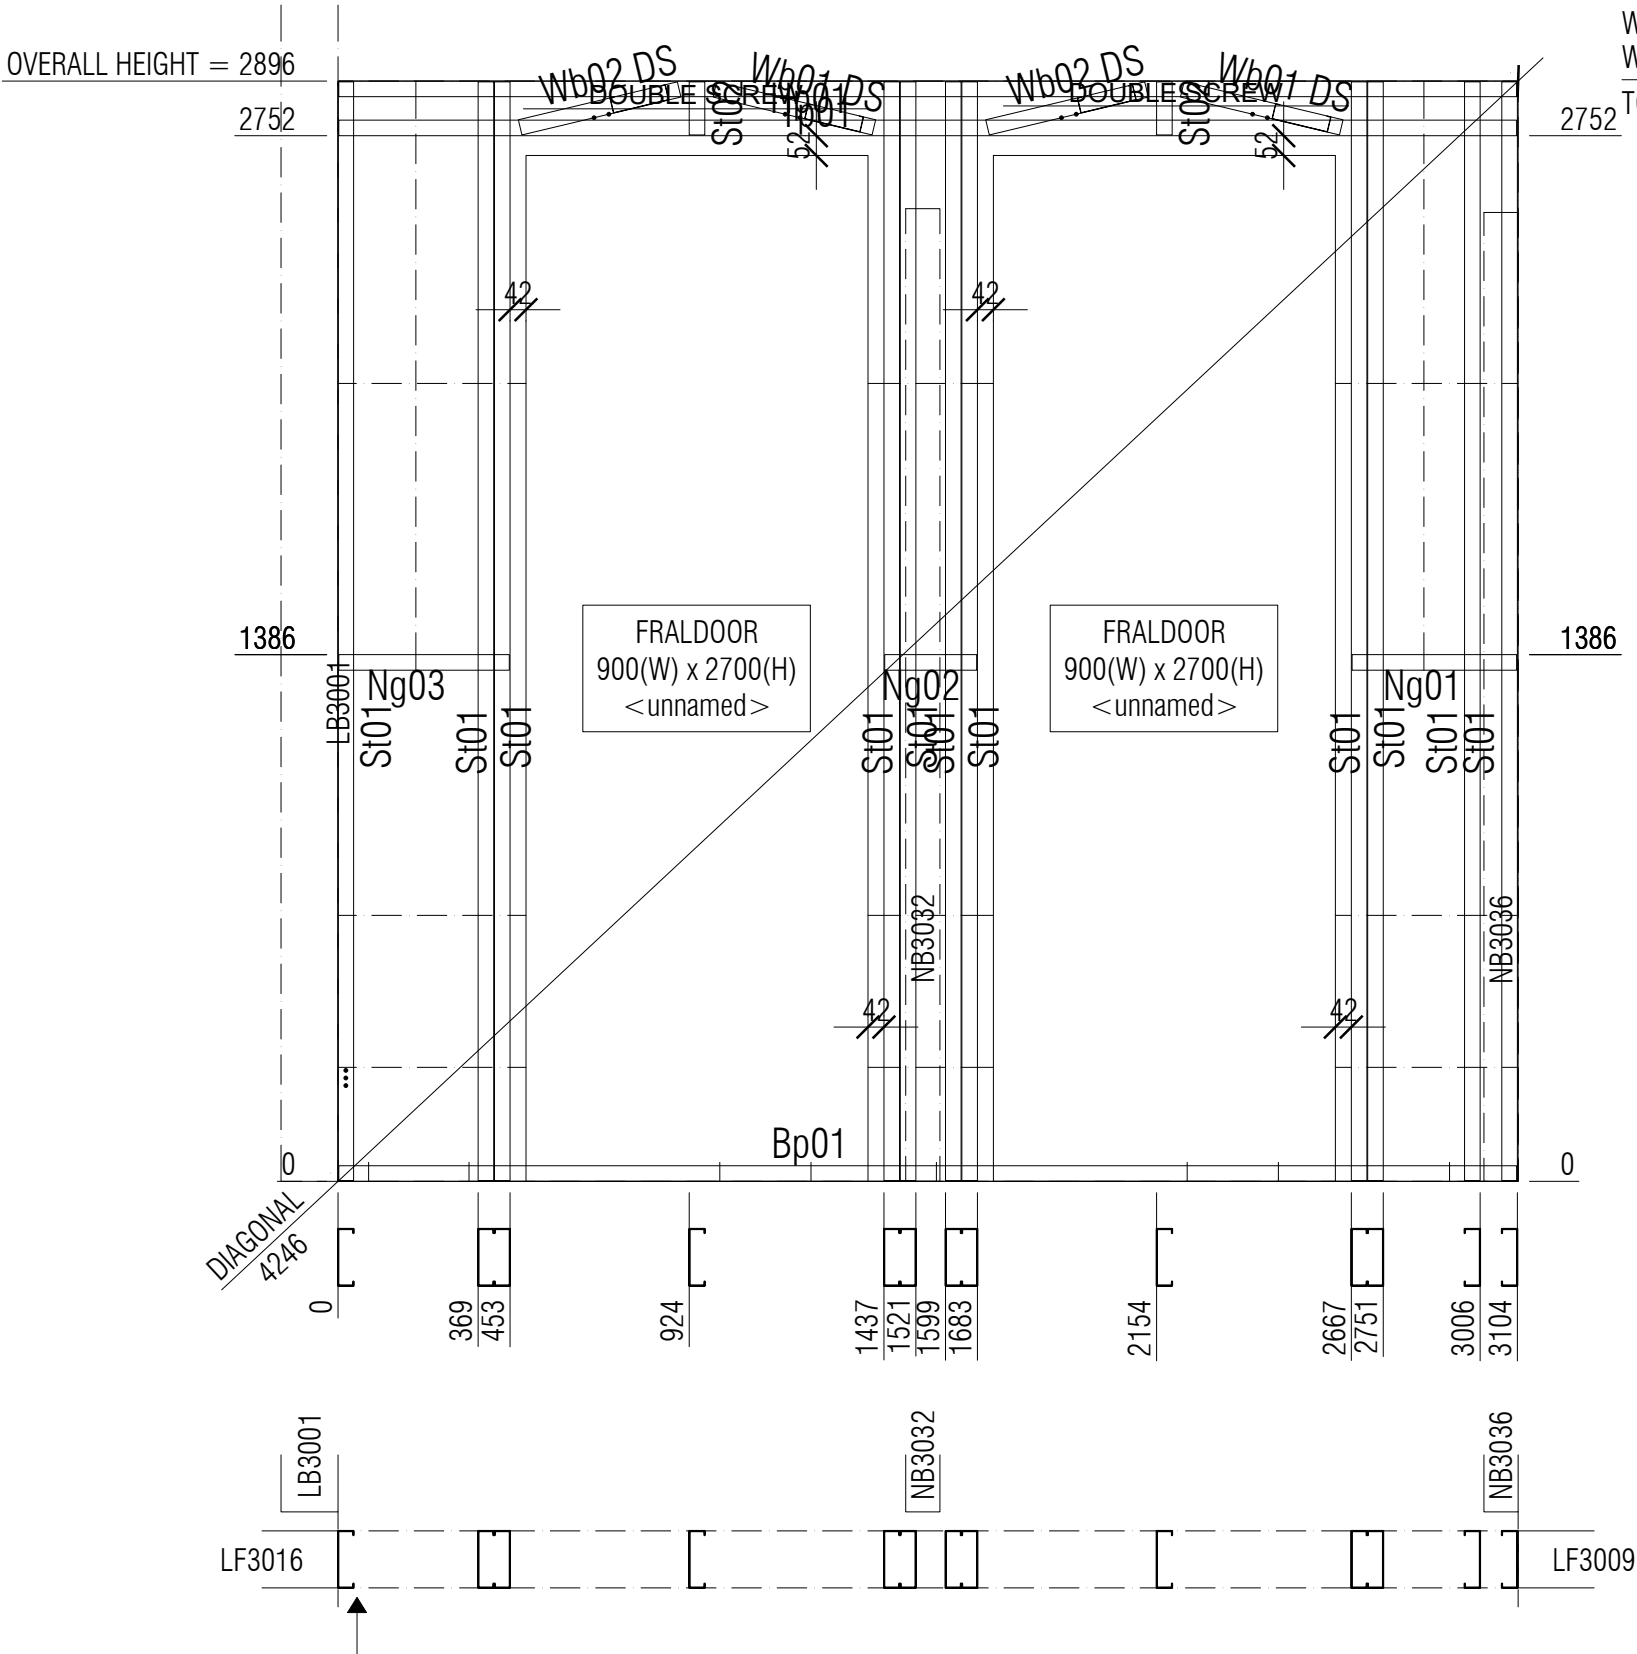

LF3013



DELIVERING SINCE 2003

DRAWN: N.N

PH: 02 4860 1416
OFFICE: 02 4860 1400

REV	DATE	REASON
A	15/09/26	IFC — Issued for construction

AUSTRUSS PROJECT NAME

CALDERWOOD

AUSTRUSS ZONE NUMBER

A3

CLIENT NAME

ADCO

PROJECT ADDRESS

179 CALDERWOOD ROAD
CALDERWOOD NSW 2527

AUSTRUSS PROJECT NUMBER

25363

DRAWING NAME

150 - PANELS

DRAWING NUMBER

LGS-A3-200


REV

A





SCAN FOR 3D

OVERALL HEIGHT = 5052

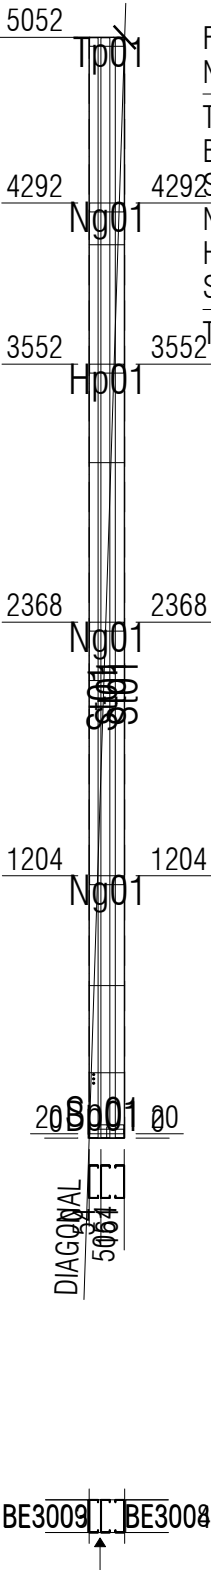

FRAME STICKS					
NAME	LENGTH	WT	QTY	PROFILE	
Tp01	157	0.3	1	150S41-950-500	
Bp01	157	0.3	1	150S41-950-500	
St01	5048	9.3	3	150S41-950-500	
Ng01	157	0.3	3	150S41-950-500	
Hp01	157	0.3	1	150S41-950-500	
Sp01	157	0.3	1	150S41-950-500	
TOTAL	16242	29.9	10		

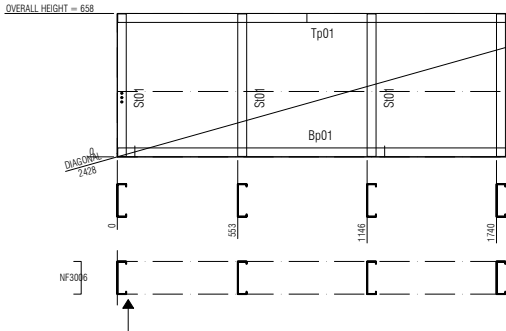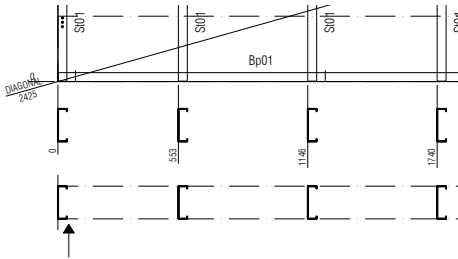

LF3014



DELIVERING SINCE 2003

DRAWN: N.N PH: 02 4860 1416
OFFICE: 02 4860 1400

REV	DATE	REASON
A	15/09/26	IFC — Issued for construction

AUSTRUSS PROJECT NAME
CALDERWOOD
AUSTRUSS ZONE NUMBER
A3

CLIENT NAME
ADCO OVERALL HEIGHT =

PROJECT ADDRESS
**179 CALDERWOOD ROAD
CALDERWOOD NSW 2527**

AUSTRUSS PROJECT NUMBER
25363

DRAWING NAME
150 - PANELS

DRAWING NUMBER
LGS-A3-200

REV
A



SCAN FOR 3D

LF3007
LF3015

FRAME STICKS					
NAME	LENGTH	WT	QTY	PROFILE	
Tp01	3055	5.6	1	150S41-950-500	
Bp01	3050	5.6	1	150S41-950-500	
Sp01	4017	7.4	1	150S41-950-500	
St01	4157	7.6	1	150S41-950-500	
St02	3988	7.3	1	150S41-950-500	
St03	4199	7.7	1	150S41-950-500	
St04	3671	6.8	1	150S41-950-500	
St05	149	0.3	1	150S41-950-500	
St06	4047	7.4	1	150S41-950-500	
St07	4120	7.6	1	150S41-950-500	
St08	3050	5.6	2	150S41-950-500	
Ng01	1257	2.3	1	150S41-950-500	
Kb01	1359	2.5	1	150S41-950-500	
Kb02	1205	2.2	1	150S41-950-500	
Kb03	755	1.4	1	150S41-950-500	
Kb04	1088	2.0	1	150S41-950-500	
Hp01	3050	5.6	1	150S41-950-500	
Sp01	49269	90.7	18	TOTAL	

OVERALL HEIGHT = 4206

HEIGHT = 3992

3675

2530

1218

0

DIAGONAL
5028

600

1163

1647

2173

2593

3054

DIAGONAL
5199

LF3019

LF3007

OVERALL HEIGHT =

LF3015



DELIVERING SINCE 2003

DRAWN: N.N PH: 02 4860 1416
OFFICE: 02 4860 1400

REV	DATE	REASON
A	15/09/26	IFC — Issued for construction

AUSTRUSS PROJECT NAME

CALDERWOOD

AUSTRUSS ZONE NUMBER

A3

CLIENT NAME

ADCO

PROJECT ADDRESS

179 CALDERWOOD ROAD
CALDERWOOD NSW 2527

AUSTRUSS PROJECT NUMBER

25363

DRAWING NAME

150 - PANELS

DRAWING NUMBER

LGS-A3-200


REV

A



SCAN FOR 3D

OVERALL HEIGHT = 5052

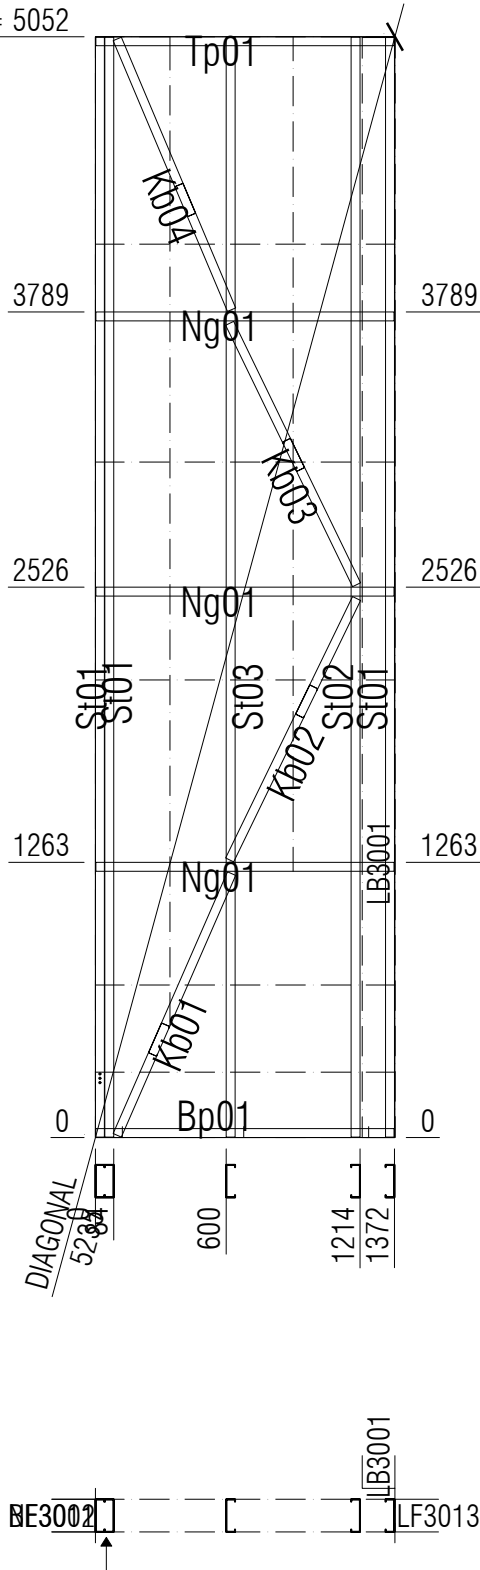

FRAME STICKS				
NAME	LENGTH	WT	QTY	PROFILE
Tp01	1368	2.5	1	150S41-950-500
Bp01	1368	2.5	1	150S41-950-500
St01	5048	9.3	3	150S41-950-500
St02	5048	9.3	1	150S41-950-500
St03	5048	9.3	1	150S41-950-500
Ng01	1368	2.5	3	150S41-950-500
Kb01	1311	2.4	1	150S41-950-500
Kb02	1334	2.5	1	150S41-950-500
Kb03	1334	2.5	1	150S41-950-500
Kb04	1349	2.5	1	150S41-950-500
TOTAL	37407	68.8	14	

LF3016



DELIVERING SINCE 2003

DRAWN: N.N PH: 02 4860 1416
OFFICE: 02 4860 1400

REV	DATE	REASON
A	15/09/26	IFC — Issued for construction

AUSTRUSS PROJECT NAME
CALDERWOOD

AUSTRUSS ZONE NUMBER
A3

CLIENT NAME
ADCO

PROJECT ADDRESS
179 CALDERWOOD ROAD
CALDERWOOD NSW 2527

AUSTRUSS PROJECT NUMBER
25363

DRAWING NAME
150 - PANELS

DRAWING NUMBER
LGS-A3-200

REV
A




SCAN FOR 3D

FRAME STICKS				
NAME	LENGTH	WT	QTY	PROFILE
Tp01	3055	5.6	1	150S41-950-500
Bp01	3050	5.6	1	150S41-950-500
St01	4017	7.4	1	150S41-950-500

OVERALL HEIGHT = 4206

HEIGHT = 3992

OVERALL HEIGHT = 5052

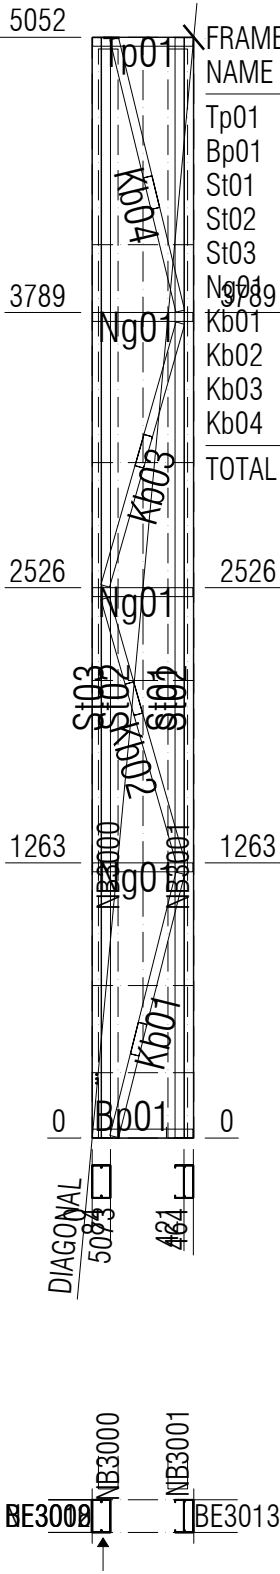

FRAME STICKS

NAME	LENGTH	WT	QTY	PROFILE
Tp01	460	0.8	1	150S41-950-500
Bp01	460	0.8	1	150S41-950-500
St01	5048	9.3	1	150S41-950-500
St02	5048	9.3	2	150S41-950-500
St03	5048	9.3	1	150S41-950-500
Ng01	460	0.8	3	150S41-950-500
Kb01	1246	2.3	1	150S41-950-500
Kb02	1254	2.3	1	150S41-950-500
Kb03	1254	2.3	1	150S41-950-500
Kb04	1286	2.4	1	150S41-950-500
TOTAL	27534	50.7	13	

LF3017



DELIVERING SINCE 2003

DRAWN: N.N PH: 02 4860 1416
OFFICE: 02 4860 1400

REV	DATE	REASON
A	15/09/26	IFC — Issued for construction

AUSTRUSS PROJECT NAME
CALDERWOOD

AUSTRUSS ZONE NUMBER
A3

CLIENT NAME
ADCO

PROJECT ADDRESS
179 CALDERWOOD ROAD
CALDERWOOD NSW 2527

AUSTRUSS PROJECT NUMBER
25363


DRAWING NAME
150 - PANELS

DRAWING NUMBER
LGS-A3-200

REV
A



SCAN FOR 3D

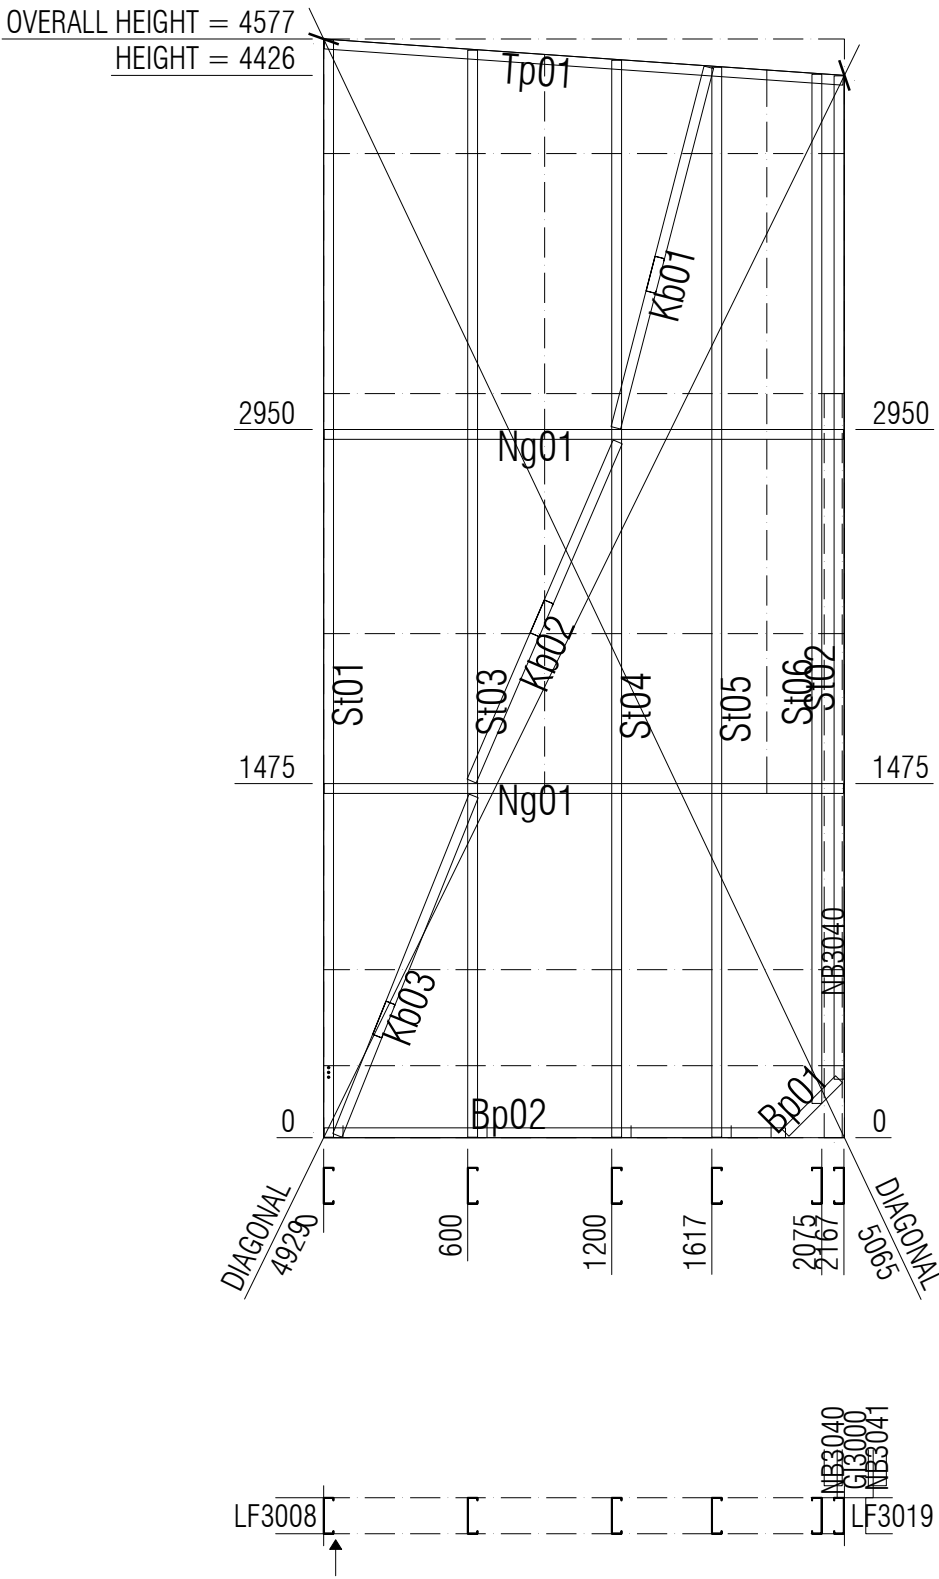

FRAME STICKS NAME	LENGTH	WT	QTY	PROFILE
Tp01	2166	4.0	1	150S41-950-500
Bp01	315	0.6	1	150S41-950-500
Bp02	1922	3.5	1	150S41-950-500
St01	4570	8.4	1	150S41-950-500
St02	4180	7.7	1	150S41-950-500
St03	4528	8.3	1	150S41-950-500
St04	4487	8.3	1	150S41-950-500
St05	4457	8.2	1	150S41-950-500
St06	4287	7.9	1	150S41-950-500
Ng01	2163	4.0	2	150S41-950-500
Kb01	1551	2.9	1	150S41-950-500
Kb02	1538	2.8	1	150S41-950-500
Kb03	1524	2.8	1	150S41-950-500
TOTAL	39854	73.3	14	

LF3018

AUSTRUSS

DELIVERING SINCE 2003

DRAWN: N.N

PH: 02 4860 1416
OFFICE: 02 4860 1400

REV	DATE	REASON
A	15/09/26	IFC — Issued for construction

AUSTRUSS PROJECT NAME

CALDERWOOD

AUSTRUSS ZONE NUMBER

A3

CLIENT NAME

ADCO

PROJECT ADDRESS

179 CALDERWOOD ROAD
CALDERWOOD NSW 2527

AUSTRUSS PROJECT NUMBER

25363

DRAWING NAME

150 - PANELS

DRAWING NUMBER

LGS-A3-200


REV

A

SCAN FOR 3D



DRAWING NUMBER		REVISION
LGS-A3-200		A

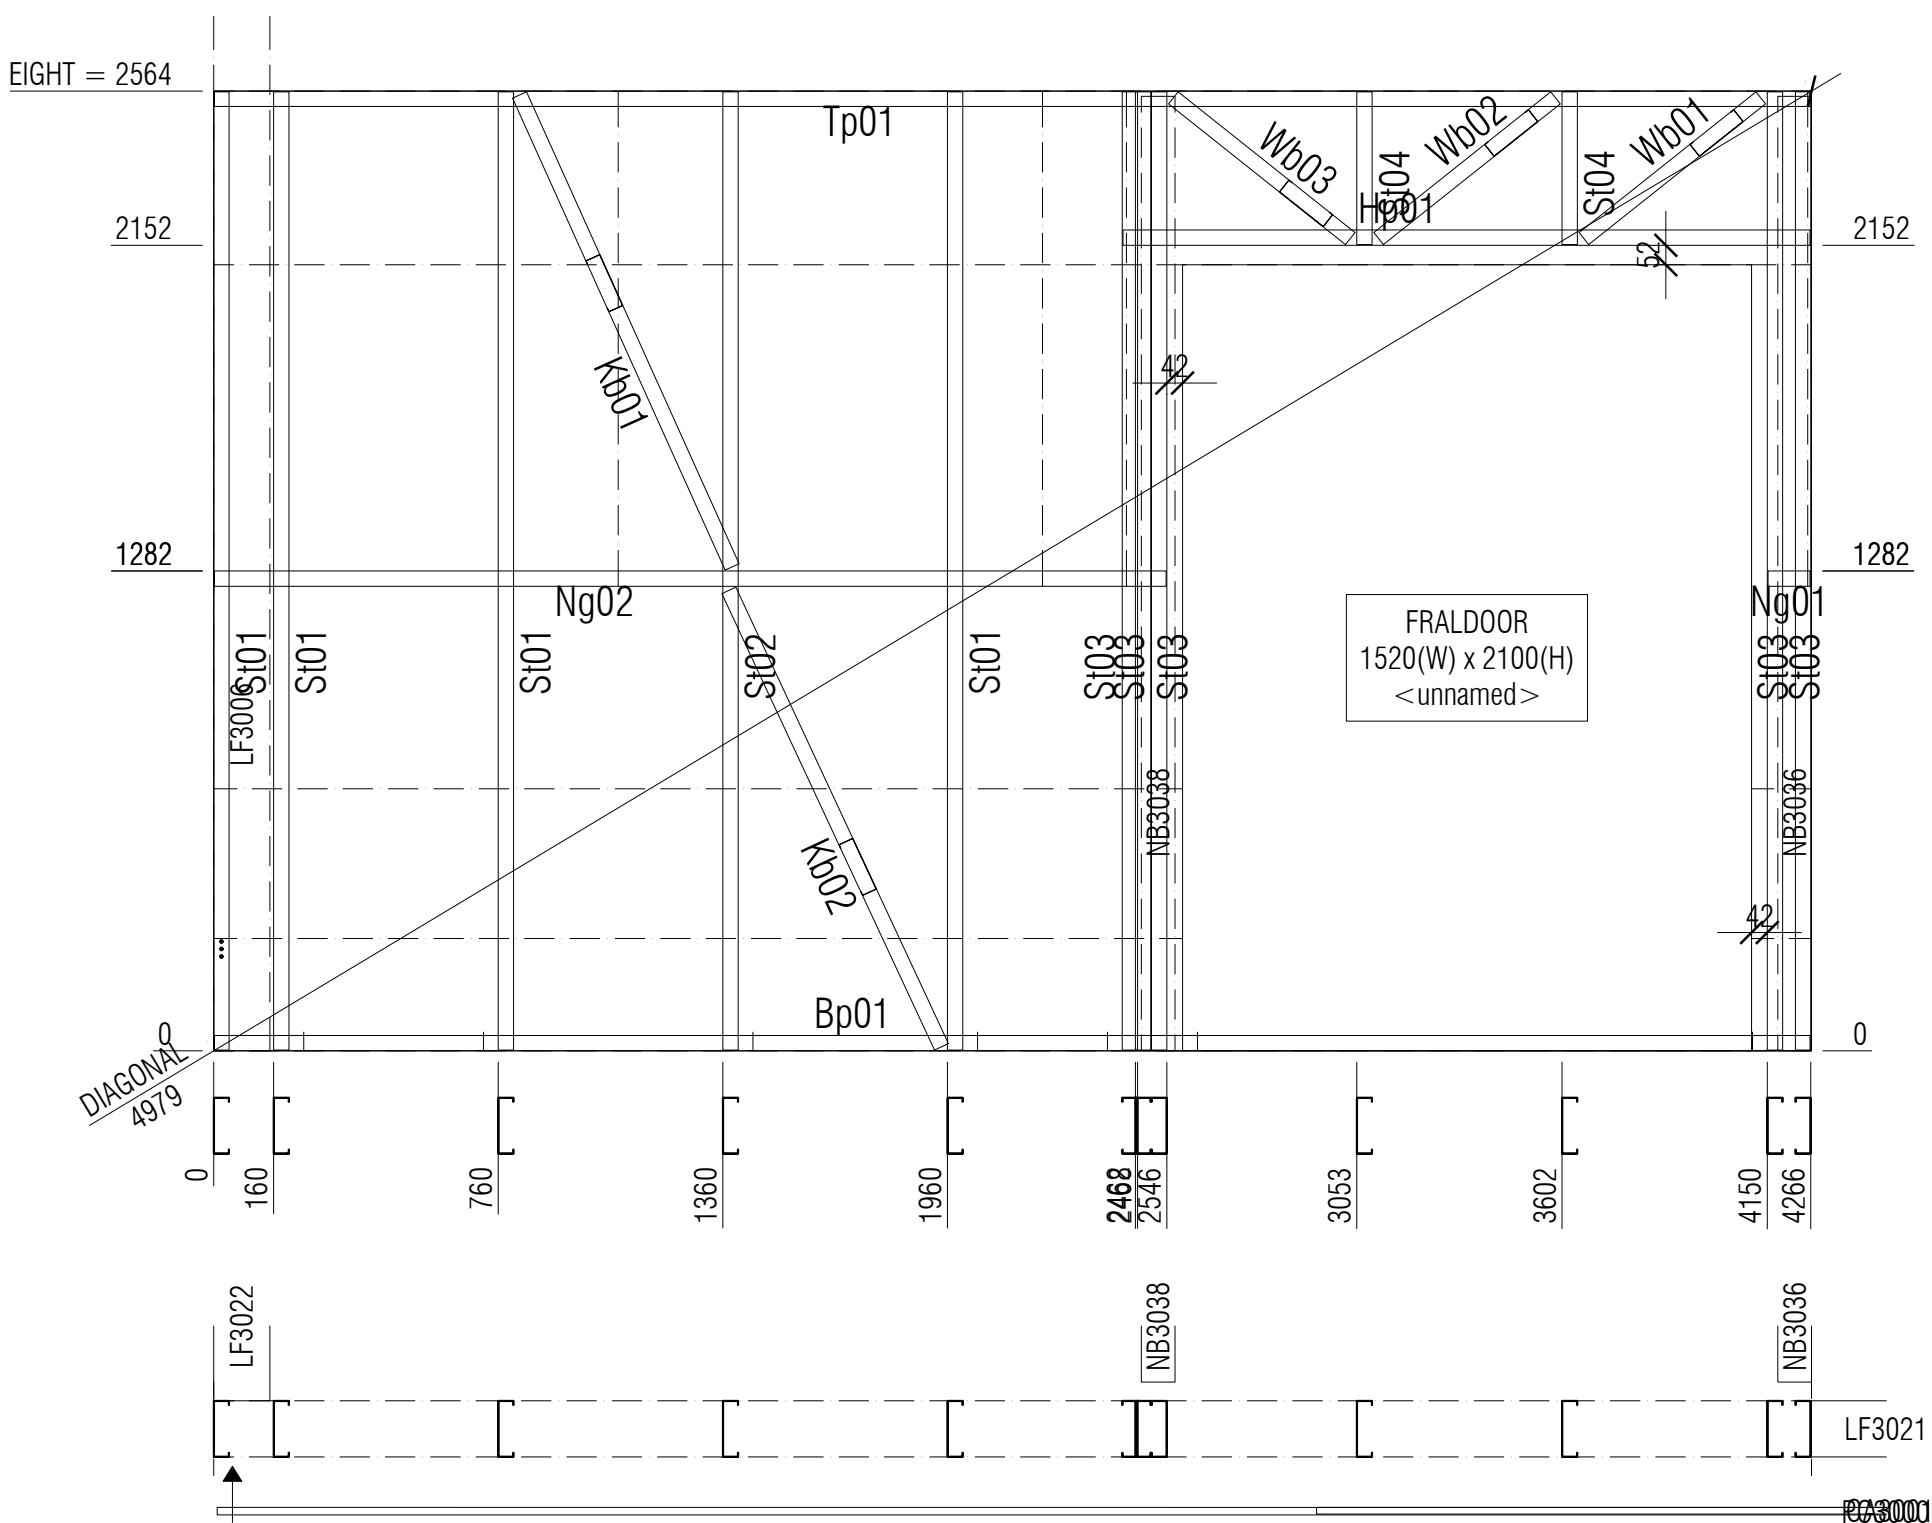

FRAME STICKS				
NAME	LENGTH	WT	QTY	
Tp01	4262	7.8	1	150S4
Bp01	4262	7.8	1	150S4
St01	2560	4.7	4	150S4
St02	2560	4.7	1	150S4
St03	2560	4.7	5	150S4
St04	408	0.8	2	150S4
Ng01	112	0.2	1	150S4
Ng02	2542	4.7	1	150S4
Kb01	1383	2.5	1	150S4
Kb02	1345	2.5	1	150S4
Hp01	1835	3.4	1	150S4
Wb01	604	1.1	1	150S4
Wb02	604	1.1	1	150S4
Wb03	604	1.1	1	150S4
TOTAL	43969	80.9	22	

LF3020

AUSTRUSS

DELIVERING SINCE 2003

DRAWN: N.N

PH: 02 4860 1416
OFFICE: 02 4860 1400

REV	DATE	REASON
A	15/09/26	IFC — Issued for construction

AUSTRUSS PROJECT NAME

CALDERWOOD

AUSTRUSS ZONE NUMBER

A3

CLIENT NAME

ADCO

PROJECT ADDRESS

179 CALDERWOOD ROAD
CALDERWOOD NSW 2527

AUSTRUSS PROJECT NUMBER

25363

DRAWING NAME

150 - PANELS

DRAWING NUMBER

LGS-A3-200


REV

A

SCAN FOR 3D

N

OVERALL HEIGHT = 2564

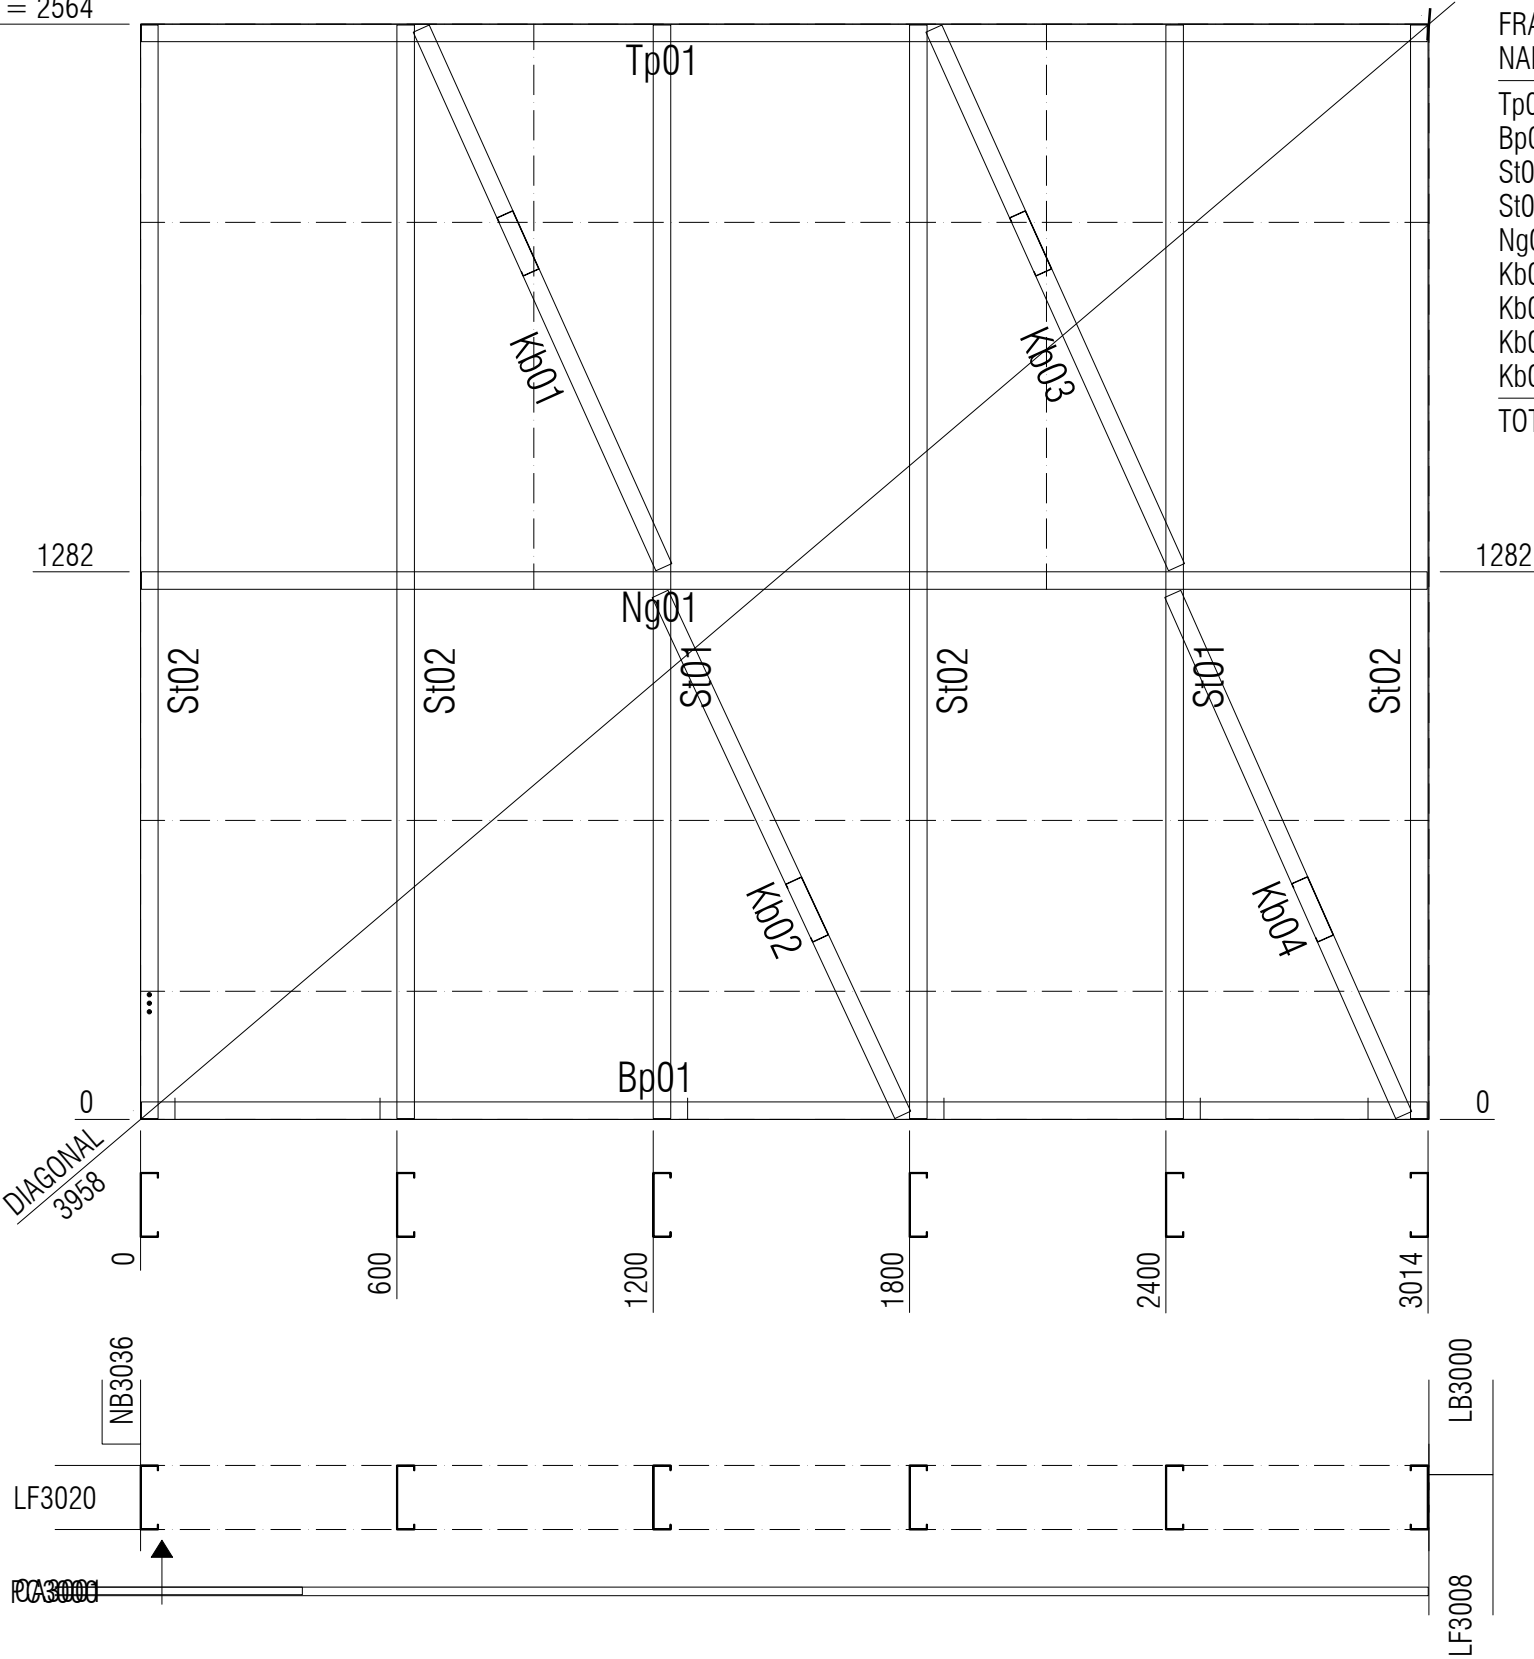

FRAME STICKS				
NAME	LENGTH	WT	QTY	PROFILE
Tp01	3010	5.5	1	150S41-950-500
Bp01	3010	5.5	1	150S41-950-500
St01	2560	4.7	2	150S41-950-500
St02	2560	4.7	4	150S41-950-500
Ng01	3010	5.5	1	150S41-950-500
Kb01	1383	2.5	1	150S41-950-500
Kb02	1345	2.5	1	150S41-950-500
Kb03	1383	2.5	1	150S41-950-500
Kb04	1334	2.5	1	150S41-950-500
TOTAL	29834	54.9	13	


LF3021

AUSTRUSS DELIVERING SINCE 2003		
DRAWN: N.N		PH: 02 4860 1416 OFFICE: 02 4860 1400
REV	DATE	REASON
A	15/09/26	IFC — Issued for construction
AUSTRUSS PROJECT NAME		
CALDERWOOD		
AUSTRUSS ZONE NUMBER		
A3		
CLIENT NAME		
ADCO		
PROJECT ADDRESS		
179 CALDERWOOD ROAD CALDERWOOD NSW 2527		
AUSTRUSS PROJECT NUMBER		
25363		
DRAWING NAME		
150 - PANELS		
DRAWING NUMBER		REV
LGS-A3-200		A



SCAN FOR 3D

OVERALL HEIGHT = 3485

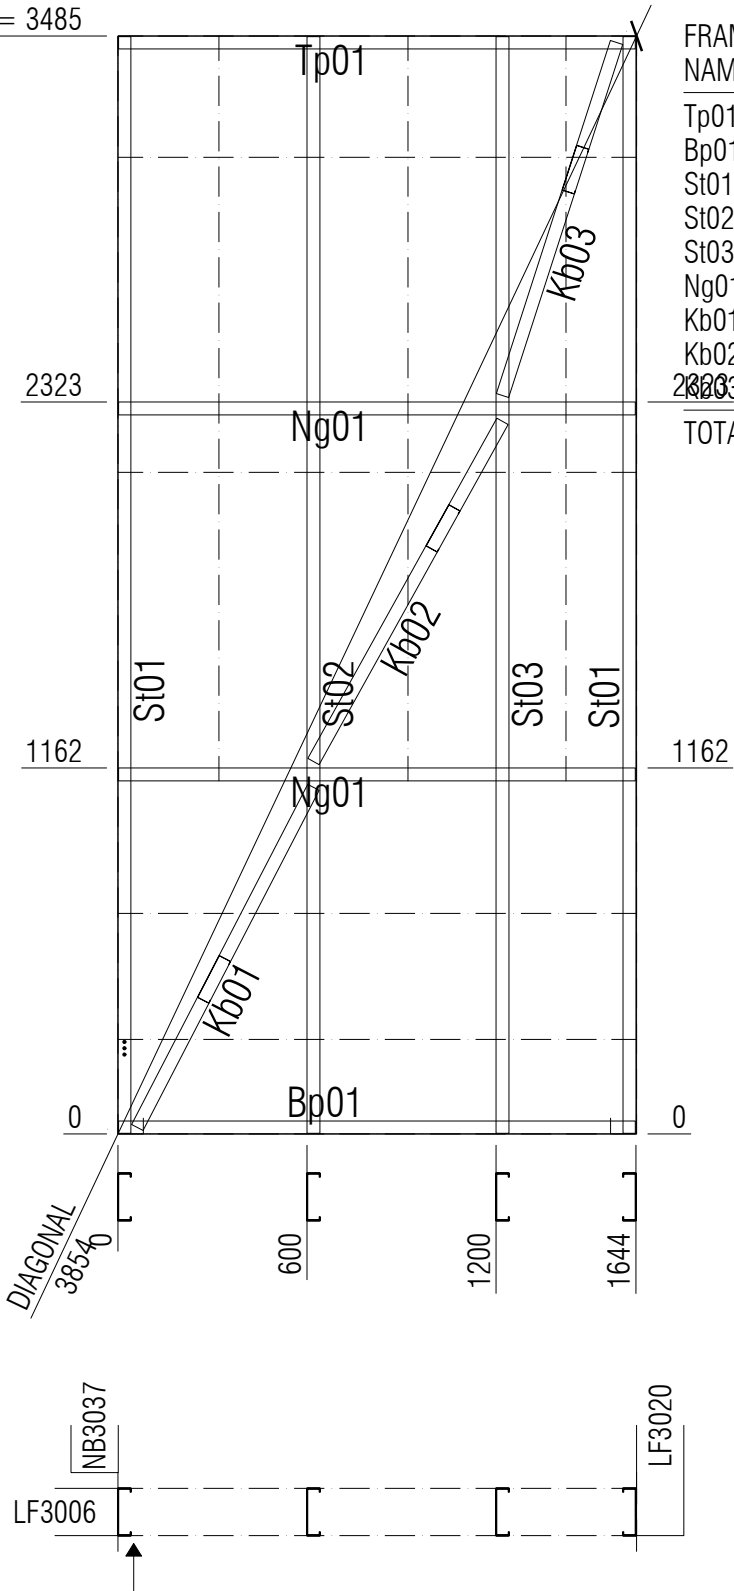

FRAME STICKS				
NAME	LENGTH	WT	QTY	PROFILE
Tp01	1640	3.0	1	150S41-950-500
Bp01	1640	3.0	1	150S41-950-500
St01	3481	6.4	2	150S41-950-500
St02	3481	6.4	1	150S41-950-500
St03	3481	6.4	1	150S41-950-500
Ng01	1640	3.0	2	150S41-950-500
Kb01	1216	2.2	1	150S41-950-500
Kb02	1235	2.3	1	150S41-950-500
Kb03	1178	2.2	1	150S41-950-500
TOTAL				
	24113	44.4	11	

OVERALL HEIGHT = 25

LF3022



DELIVERING SINCE 2003

DRAWN: N.N

PH: 02 4860 1400
OFFICE: 02 4860 1400

REV	DATE	REASON
A	15/09/26	IFC — Issued for construction

AUSTRUSS PROJECT NAME

CALDERWOOD

AUSTRUSS ZONE NUMBER

A3

CLIENT NAME

ADCO

PROJECT ADDRESS

179 CALDERWOOD ROAD
CALDERWOOD NSW 2527

AUSTRUSS PROJECT NUMBER

25363

DRAWING NAME

WALL LAYOUT

DRAWING NUMBER

LGS-A3-110


REV

A



SCAN FOR 3D

OVERALL HEIGHT = 668

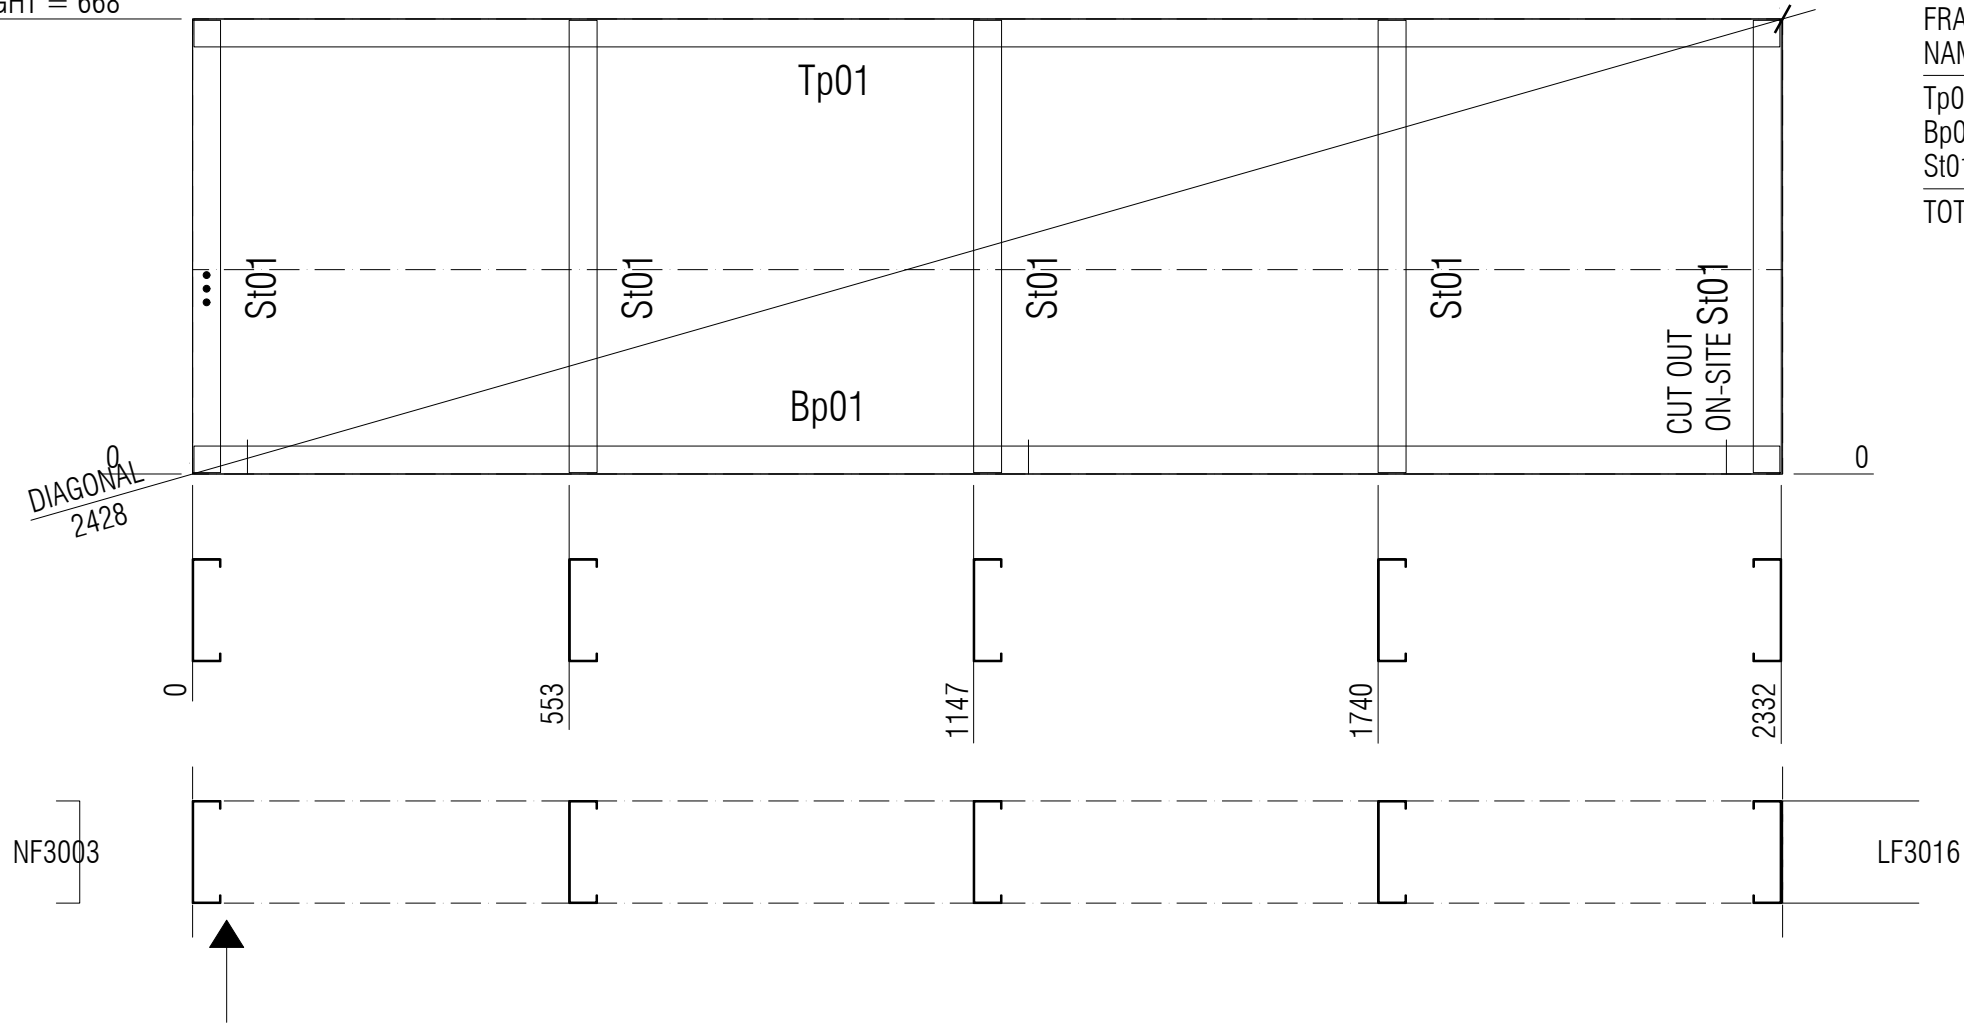

FRAME STICKS				
NAME	LENGTH	WT	QTY	PROFILE
Tp01	2328	4.3	1	150S41-950-500
Bp01	2328	4.3	1	150S41-950-500
St01	664	1.2	5	150S41-950-500
TOTAL	7976	14.7	7	

NF3002



DELIVERING SINCE 2003

DRAWN: N.N

PH: 02 4860 1416
OFFICE: 02 4860 1400

REV	DATE	REASON
A	15/09/26	IFC — Issued for construction

AUSTRUSS PROJECT NAME

CALDERWOOD

AUSTRUSS ZONE NUMBER

A3

CLIENT NAME

ADCO

PROJECT ADDRESS

179 CALDERWOOD ROAD
CALDERWOOD NSW 2527

AUSTRUSS PROJECT NUMBER

25363

DRAWING NAME

150 - PANELS

DRAWING NUMBER

LGS-A3-200


REV

A



SCAN FOR 3D

OVERALL HEIGHT = 668

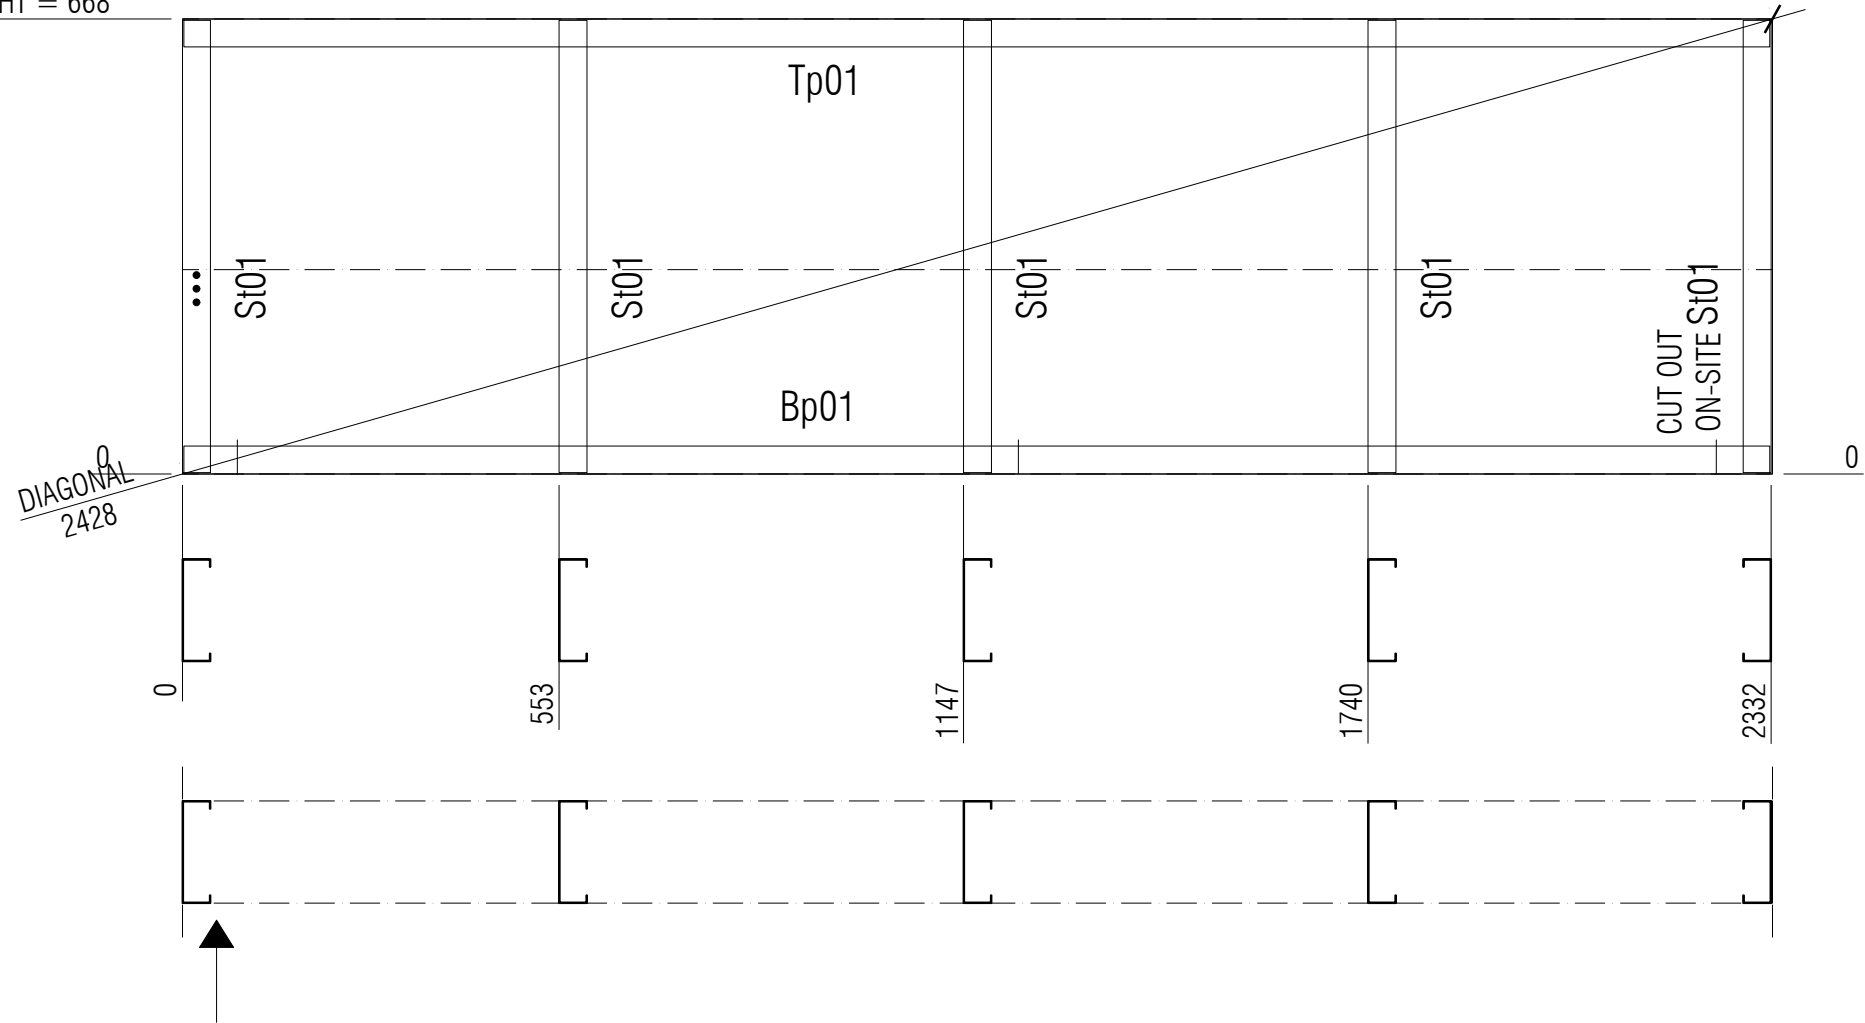

FRAME STICKS				
NAME	LENGTH	WT	QTY	PROFILE
Tp01	2328	4.3	1	150S41-950-500
Bp01	2328	4.3	1	150S41-950-500
St01	664	1.2	5	150S41-950-500
TOTAL	7976	14.7	7	

NF3002



SCAN FOR 3D

NF3003



DELIVERING SINCE 2003

DRAWN: N.N

PH: 02 4860 1416
OFFICE: 02 4860 1400

REV	DATE	REASON
A	15/09/26	IFC — Issued for construction

AUSTRUSS PROJECT NAME

CALDERWOOD

AUSTRUSS ZONE NUMBER

A3

CLIENT NAME

ADCO

PROJECT ADDRESS

179 CALDERWOOD ROAD
CALDERWOOD NSW 2527

AUSTRUSS PROJECT NUMBER

25363

DRAWING NAME


150 - PANELS

DRAWING NUMBER

LGS-A3-200

REV

A

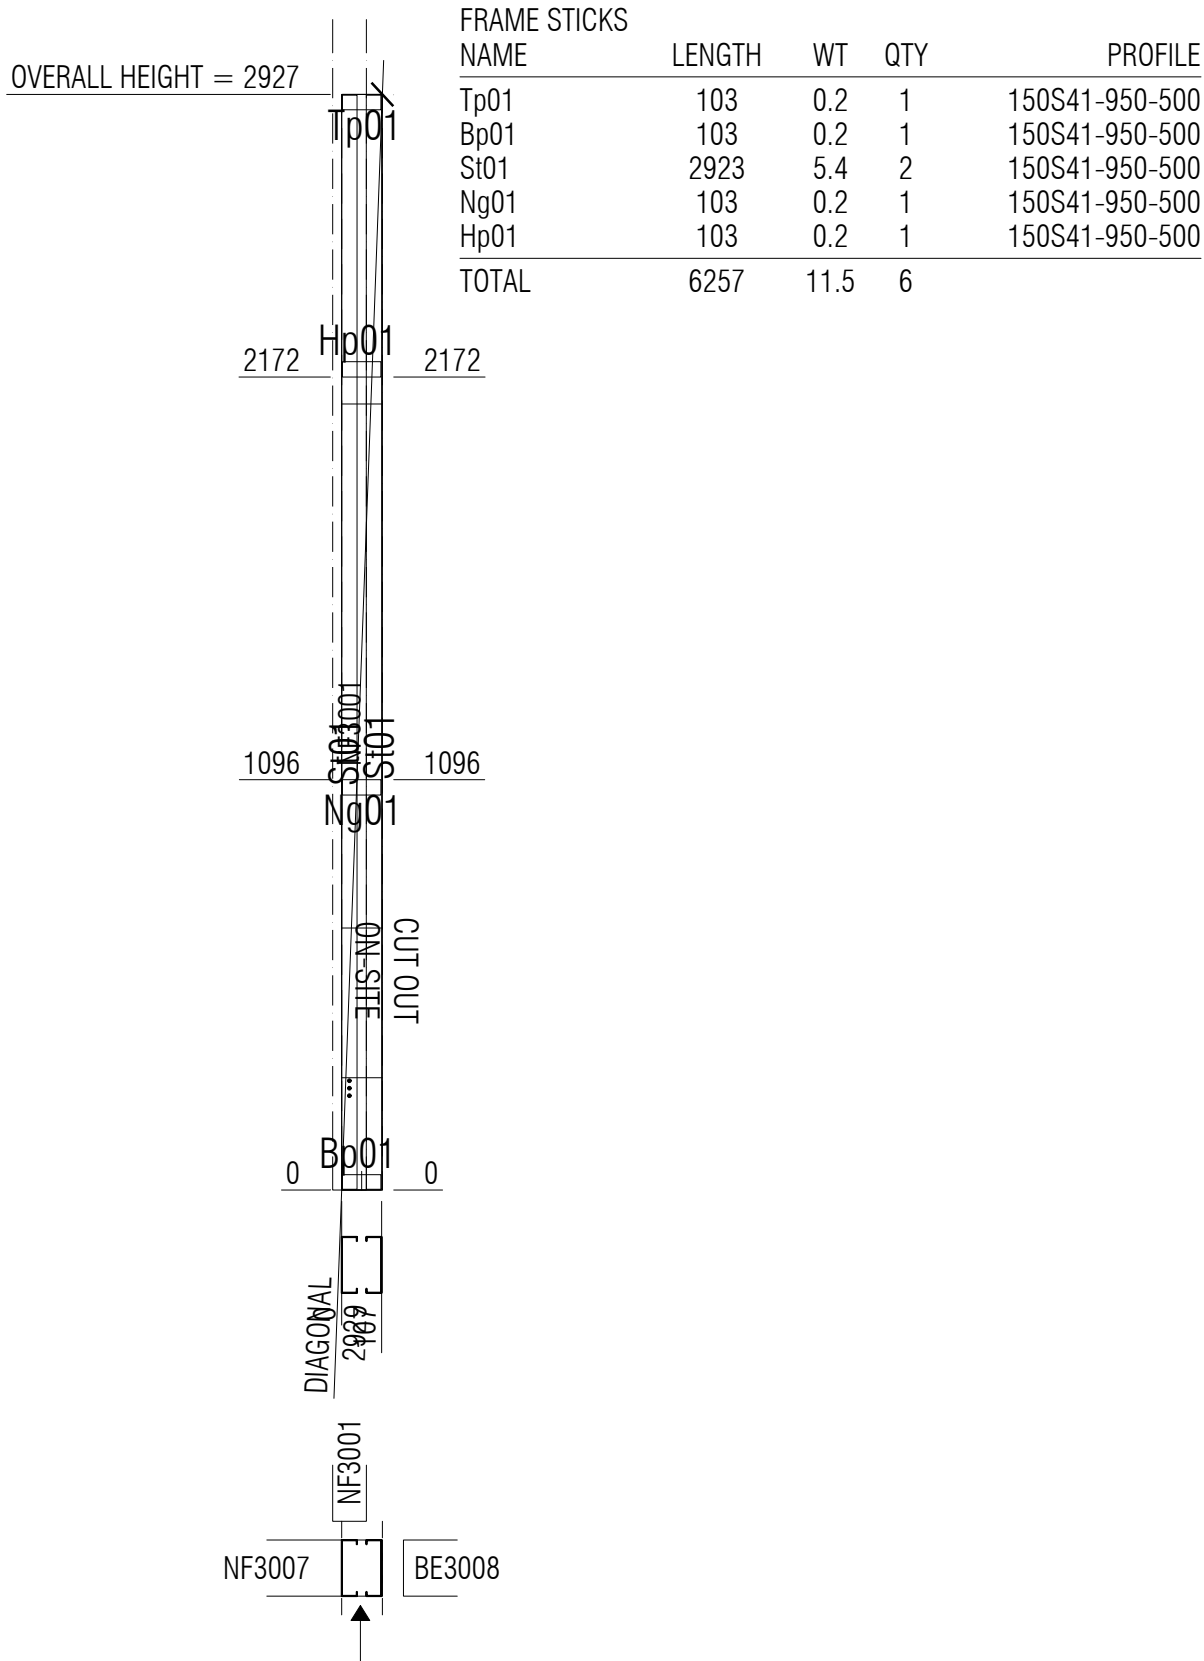

NF3004

**AUSTRUSS**
DELIVERING SINCE 2003

DRAWN: N.N

PH: 02 4860 1416
OFFICE: 02 4860 1400

REV	DATE	REASON
A	15/09/26	IFC — Issued for construction

AUSTRUSS PROJECT NAME

CALDERWOOD

AUSTRUSS ZONE NUMBER

A3

CLIENT NAME

ADCO

PROJECT ADDRESS

179 CALDERWOOD ROAD
CALDERWOOD NSW 2527

AUSTRUSS PROJECT NUMBER

25363

DRAWING NAME

150 - PANELS

DRAWING NUMBER

LGS-A3-200

REV

A

SCAN FOR 3D



Technical drawing of a building floor plan. The plan is rectangular with a diagonal line running from the bottom-left corner to the top-right corner. The diagonal is labeled "DIAGONAL 2425" with a dimension line. The plan is divided into several sections by vertical lines. The top section is labeled "Tp01" and the bottom section is labeled "Bp01". The vertical sections are labeled "St01" and "CUT OUT ON-SITE St01". The plan includes a north arrow pointing upwards. The dimensions of the plan are 0, 553, 1146, 1740, and 2332, indicating the width of the sections. The total width is 2332. The plan also shows a dashed line representing a boundary or a path.

NF3005

AUSTRUSS
DELIVERING SINCE 2003

<u>REV</u>	<u>DATE</u>	<u>REASON</u>
A	15/09/26	IFC — Issued for construction


REV
A

DRAWING NUMBER
LGS-A3-200




REV
A

OVERALL HEIGHT = 653

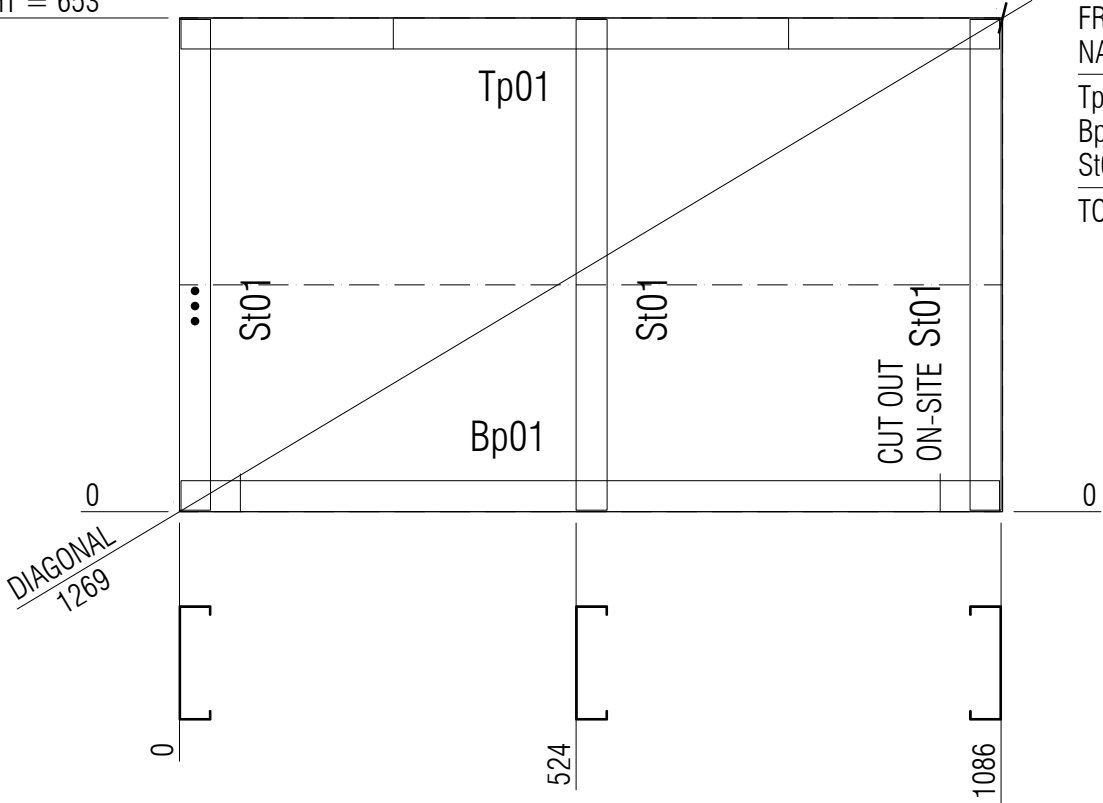

FRAME STICKS NAME	LENGTH	WT	QTY	PROFILE
Tp01	1082	2.0	1	150S41-950-500
Bp01	1082	2.0	1	150S41-950-500
St01	649	1.2	3	150S41-950-500
TOTAL	4112	7.6	5	

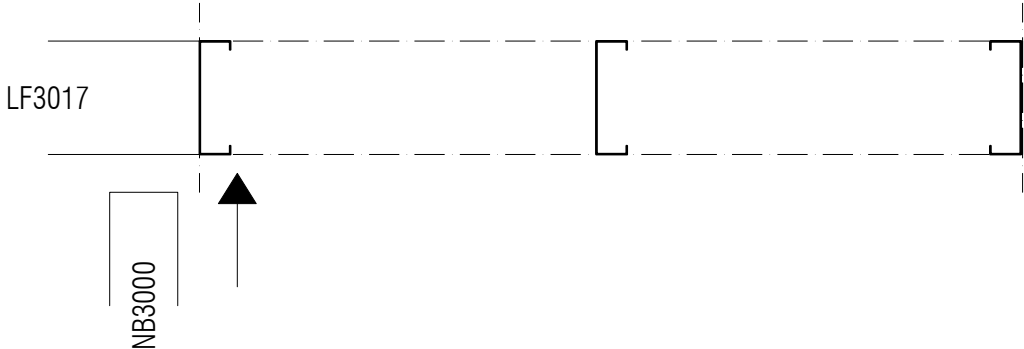

NF3008



DELIVERING SINCE 2003

DRAWN: N.N PH: 02 4860 1416
OFFICE: 02 4860 1400

REV	DATE	REASON
A	15/09/26	IFC — Issued for construction

AUSTRUSS PROJECT NAME

CALDERWOOD

AUSTRUSS ZONE NUMBER

A3

CLIENT NAME

ADCO

PROJECT ADDRESS

179 CALDERWOOD ROAD
CALDERWOOD NSW 2527

AUSTRUSS PROJECT NUMBER

25363

DRAWING NAME
150 - PANELS

DRAWING NUMBER
LGS-A3-200

REV
A




SCAN FOR 3D

WELD PART

212x2.4mm PURLIN COIL WELDED TO FRONT SIDE

OVERALL HEIGHT = 668

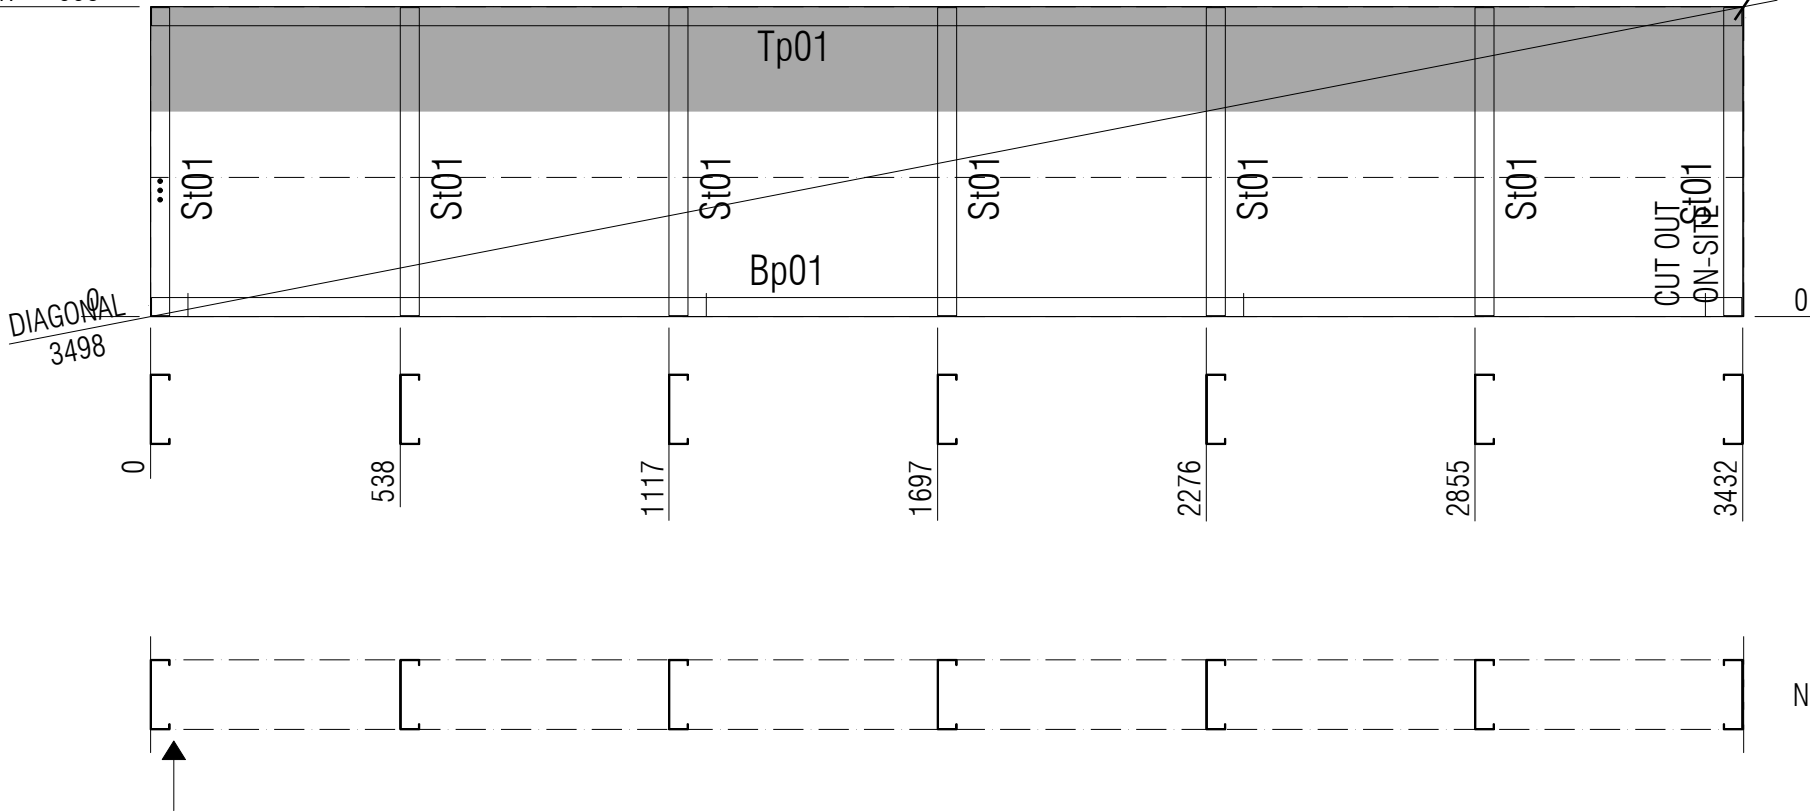

FRAME STICKS NAME	LENGTH	WT	QTY	PROFILE
Tp01	3428	6.3	1	150S41-950-500
Bp01	3428	6.3	1	150S41-950-500
St01	664	1.2	7	150S41-950-500
TOTAL	11504	21.2	9	

NF3010

NF3009



DELIVERING SINCE 2003

DRAWN: N.N

PH: 02 4860 1416
OFFICE: 02 4860 1400

REV	DATE	REASON
A	15/09/26	IFC — Issued for construction

AUSTRUSS PROJECT NAME

CALDERWOOD

AUSTRUSS ZONE NUMBER

A3

CLIENT NAME

ADCO

PROJECT ADDRESS

179 CALDERWOOD ROAD
CALDERWOOD NSW 2527

AUSTRUSS PROJECT NUMBER

25363

DRAWING NAME

150 - PANELS

DRAWING NUMBER

LGS-A3-200

REV

A




SCAN FOR 3D


WELD PART

212x2.4mm PURLIN COIL WELDED TO FRONT SIDE

OVERALL HEIGHT = 668

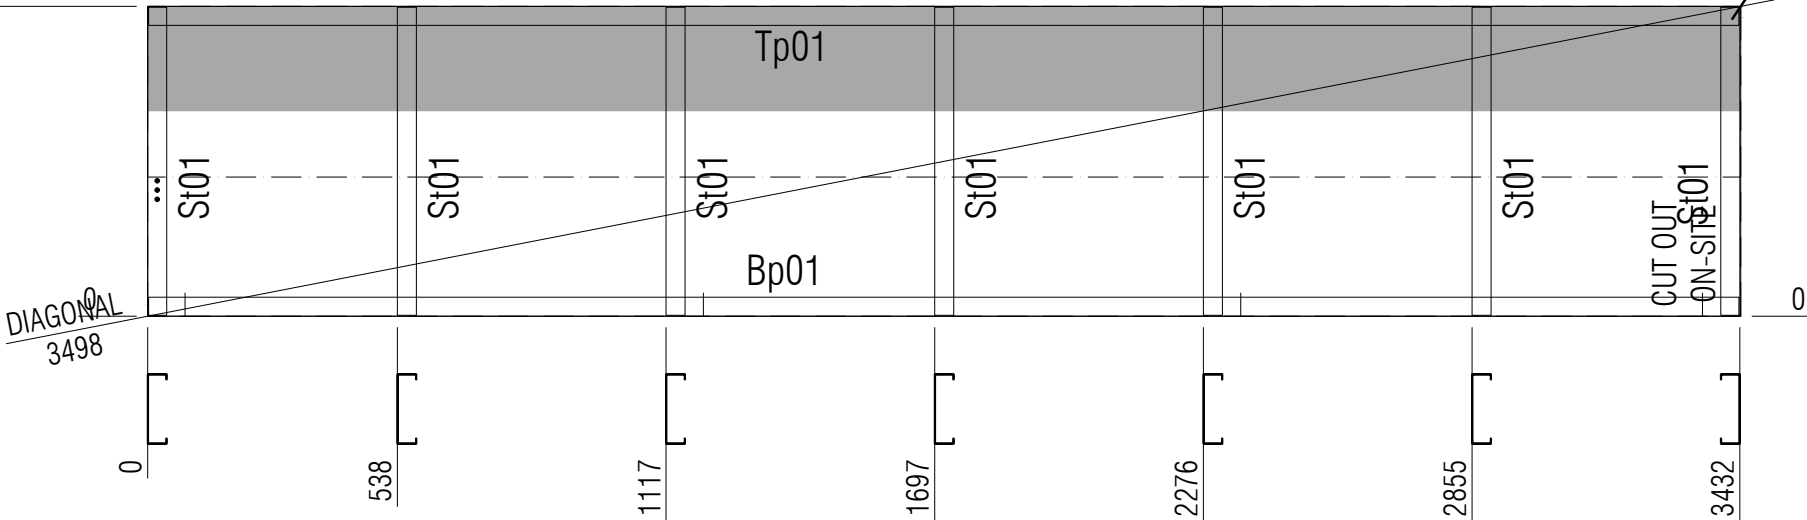

FRAME STICKS NAME	LENGTH	WT	QTY	PROFILE
Tp01	3428	6.3	1	150S41-950-500
Bp01	3428	6.3	1	150S41-950-500
St01	664	1.2	7	150S41-950-500
TOTAL	11504	21.2	9	

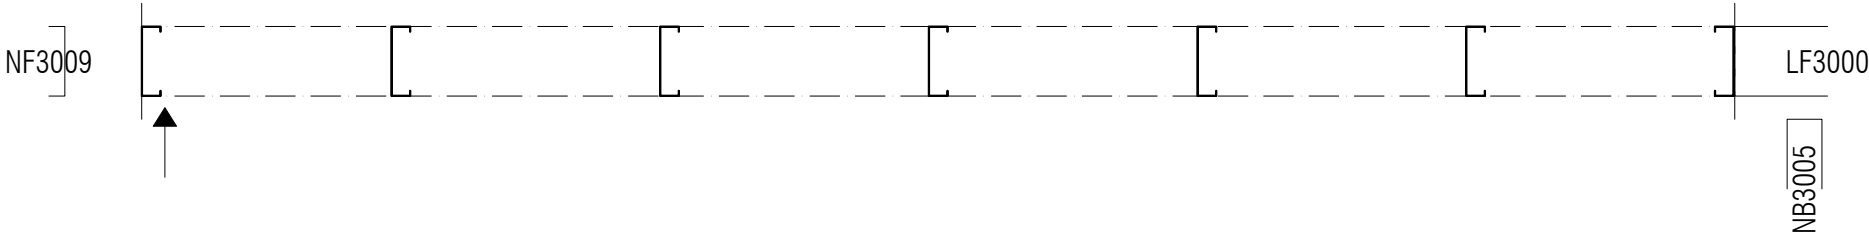

NF3010



DELIVERING SINCE 2003

DRAWN: N.N

PH: 02 4860 1416

OFFICE: 02 4860 1400

REV	DATE	REASON
A	15/09/26	IFC — Issued for construction

AUSTRUSS PROJECT NAME

CALDERWOOD

AUSTRUSS ZONE NUMBER

A3

CLIENT NAME

ADCO

PROJECT ADDRESS

179 CALDERWOOD ROAD

CALDERWOOD NSW 2527

AUSTRUSS PROJECT NUMBER

25363

DRAWING NAME

150 - PANELS

DRAWING NUMBER

LGS-A3-200

REV

A




SCAN FOR 3D


WELD PART

212x2.4mm PURLIN COIL WELDED TO FRONT SIDE

OVERALL HEIGHT = 668

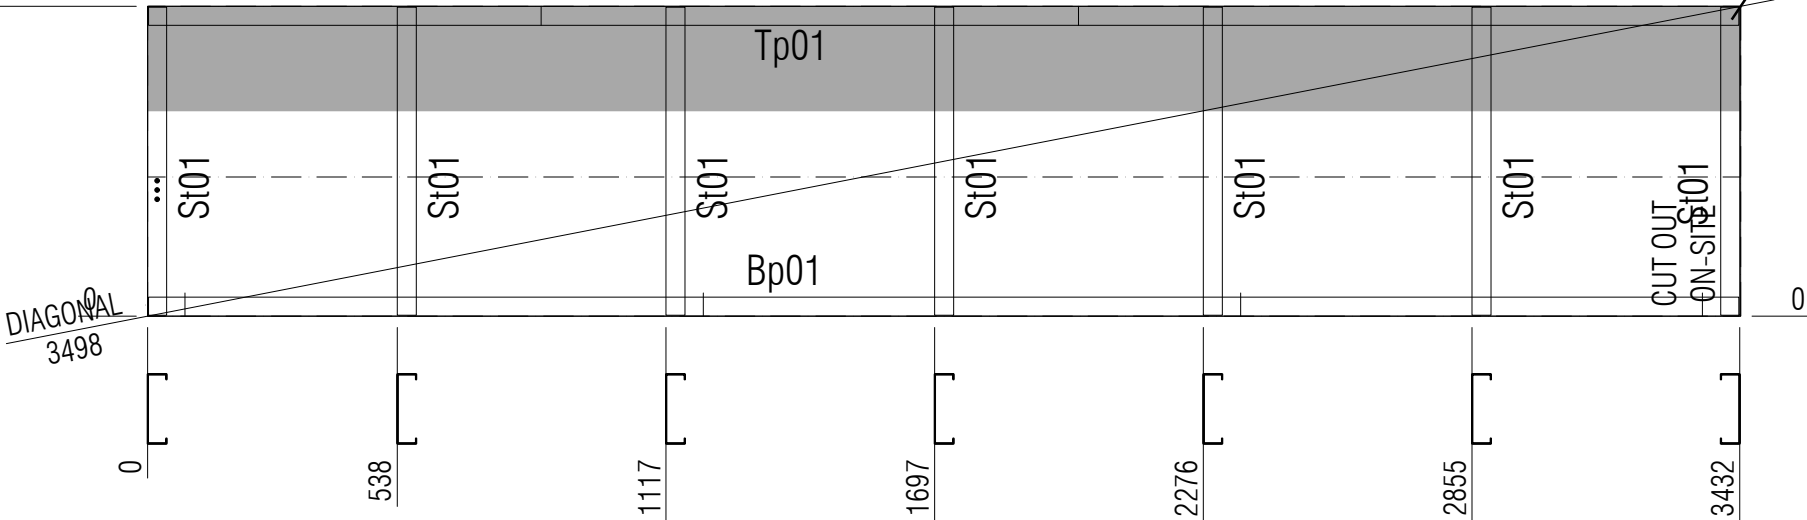

FRAME STICKS NAME	LENGTH	WT	QTY	PROFILE
Tp01	3428	6.3	1	150S41-950-500
Bp01	3428	6.3	1	150S41-950-500
St01	664	1.2	7	150S41-950-500
TOTAL	11504	21.2	9	

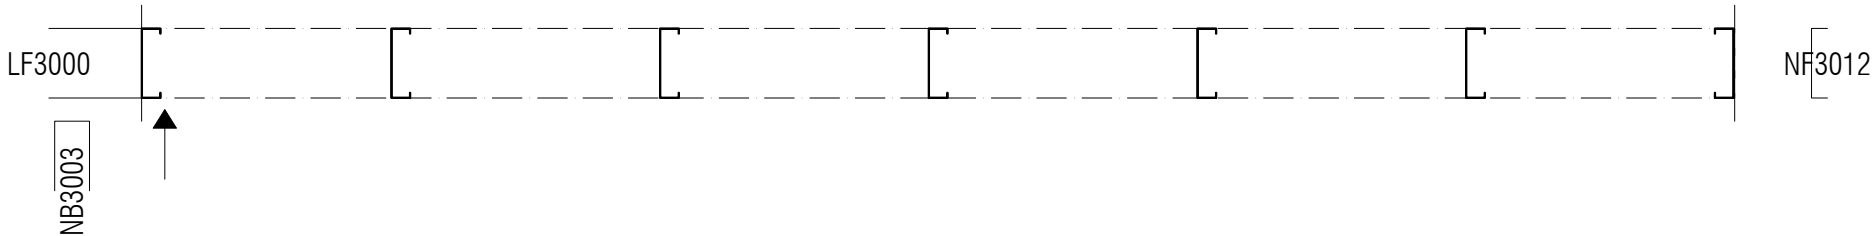

SCAN FOR 3D

NF3011



DELIVERING SINCE 2003

DRAWN: N.N

PH: 02 4860 1416

OFFICE: 02 4860 1400

REV	DATE	REASON
A	15/09/26	IFC — Issued for construction

AUSTRUSS PROJECT NAME

CALDERWOOD

AUSTRUSS ZONE NUMBER

A3

CLIENT NAME

ADCO

PROJECT ADDRESS

179 CALDERWOOD ROAD

CALDERWOOD NSW 2527

AUSTRUSS PROJECT NUMBER

25363

DRAWING NAME

150 - PANELS

DRAWING NUMBER

LGS-A3-200


REV

A


WELD PART

212x2.4mm PURLIN COIL WELDED TO FRONT SIDE

OVERALL HEIGHT = 668

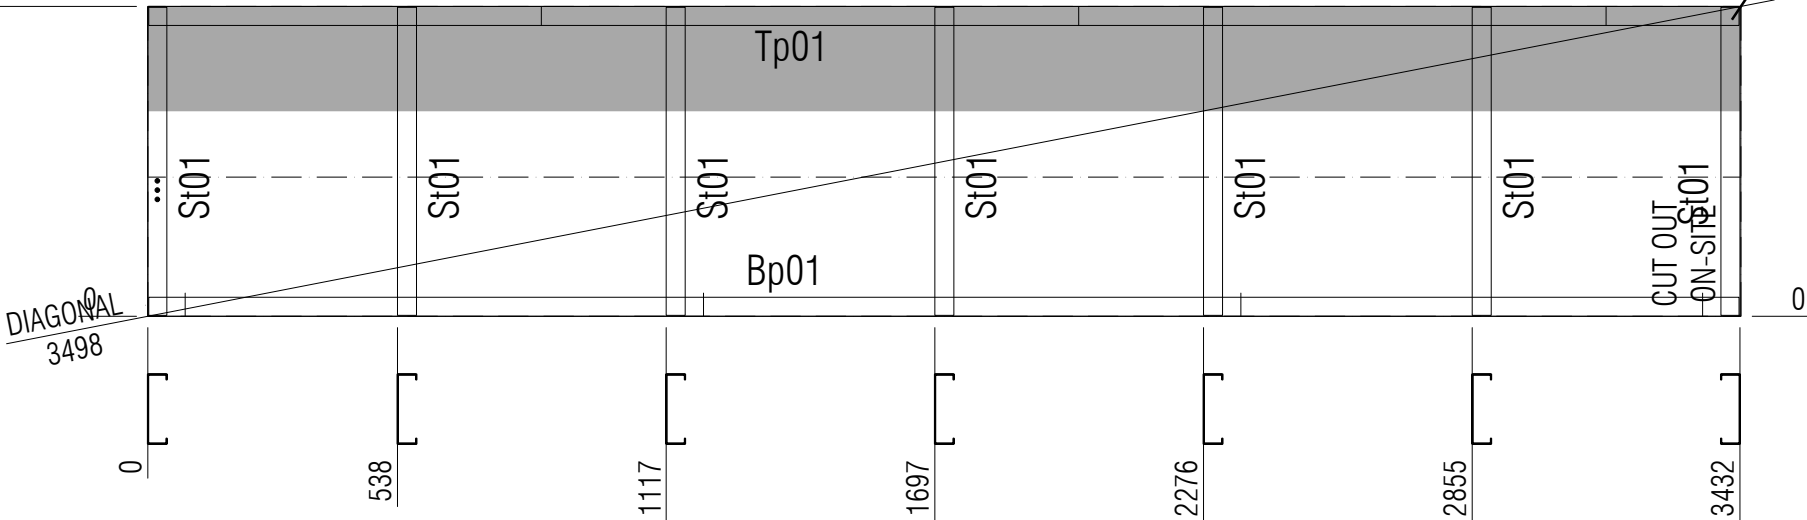

FRAME STICKS				
NAME	LENGTH	WT	QTY	PROFILE
Tp01	3428	6.3	1	150S41-950-500
Bp01	3428	6.3	1	150S41-950-500
St01	664	1.2	7	150S41-950-500
TOTAL	11504	21.2	9	

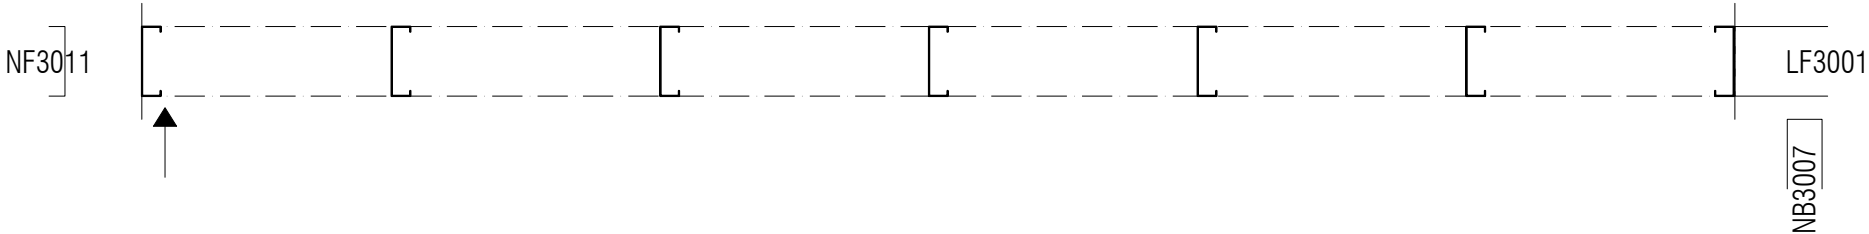

NF3012



DELIVERING SINCE 2003

DRAWN: N.N

PH: 02 4860 1416
OFFICE: 02 4860 1400

REV	DATE	REASON
A	15/09/26	IFC — Issued for construction

AUSTRUSS PROJECT NAME

CALDERWOOD

AUSTRUSS ZONE NUMBER

A3

CLIENT NAME

ADCO

PROJECT ADDRESS

179 CALDERWOOD ROAD
CALDERWOOD NSW 2527

AUSTRUSS PROJECT NUMBER

25363

DRAWING NAME

150 - PANELS

DRAWING NUMBER

LGS-A3-200

REV

A




SCAN FOR 3D


WELD PART

212x2.4mm PURLIN COIL WELDED TO FRONT SIDE

OVERALL HEIGHT = 668

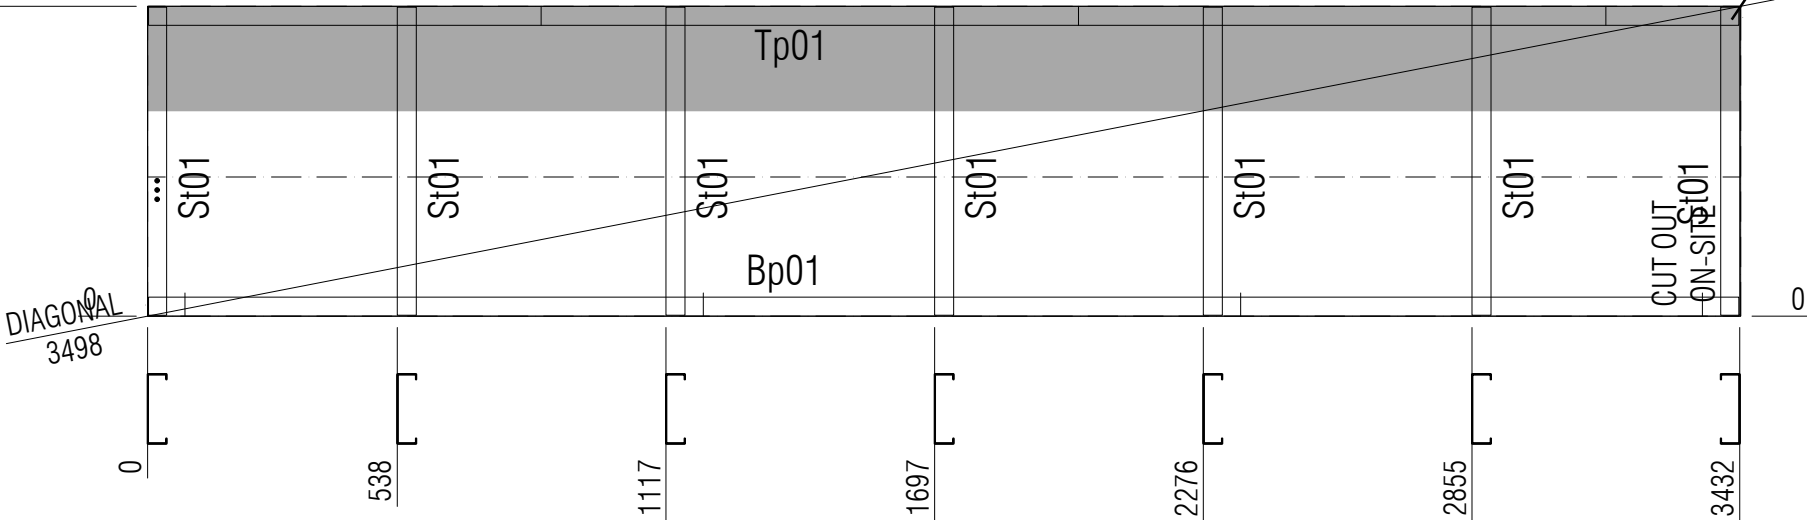

FRAME STICKS NAME	LENGTH	WT	QTY	PROFILE
Tp01	3428	6.3	1	150S41-950-500
Bp01	3428	6.3	1	150S41-950-500
St01	664	1.2	7	150S41-950-500
TOTAL	11504	21.2	9	

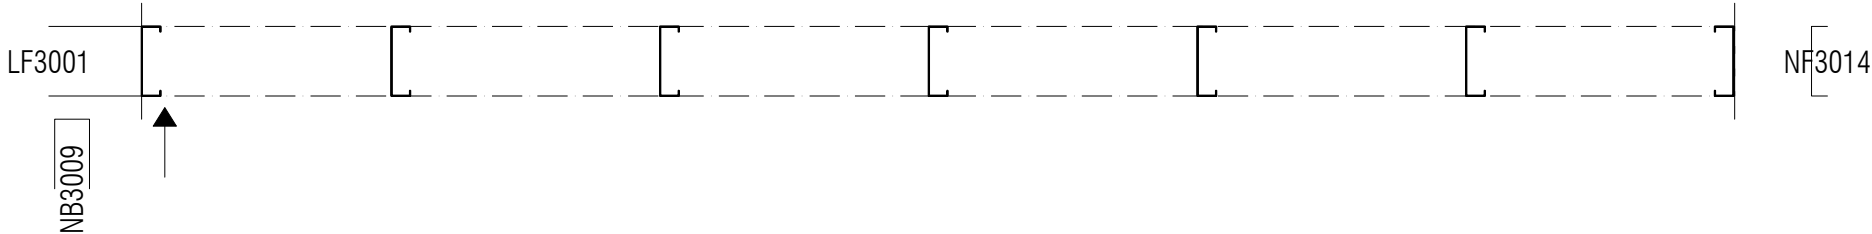

NF3013



DELIVERING SINCE 2003

DRAWN: N.N

PH: 02 4860 1416
OFFICE: 02 4860 1400

REV	DATE	REASON
A	15/09/26	IFC — Issued for construction

AUSTRUSS PROJECT NAME

CALDERWOOD

AUSTRUSS ZONE NUMBER

A3

CLIENT NAME

ADCO

PROJECT ADDRESS

179 CALDERWOOD ROAD
CALDERWOOD NSW 2527

AUSTRUSS PROJECT NUMBER

25363

DRAWING NAME

150 - PANELS

DRAWING NUMBER

LGS-A3-200

REV

A




SCAN FOR 3D


WELD PART

212x2.4mm PURLIN COIL WELDED TO FRONT SIDE

OVERALL HEIGHT = 668

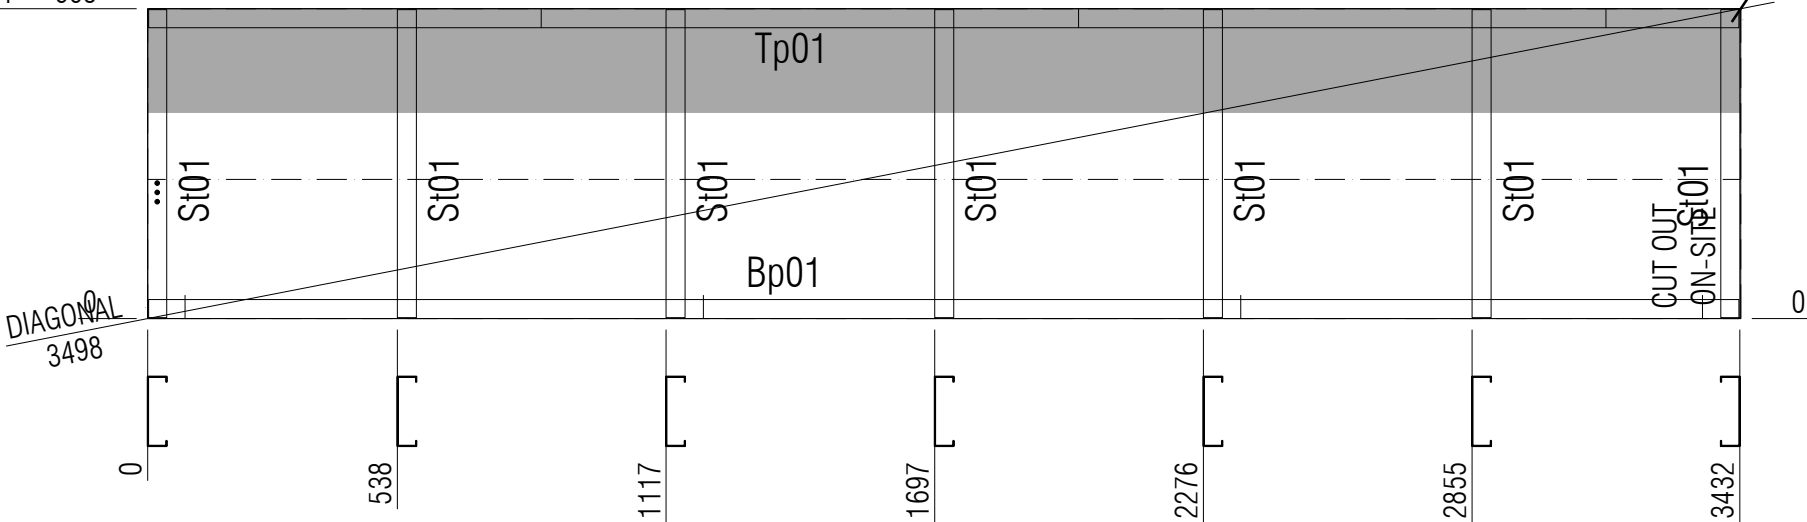

FRAME STICKS NAME	LENGTH	WT	QTY	PROFILE
Tp01	3428	6.3	1	150S41-950-500
Bp01	3428	6.3	1	150S41-950-500
St01	664	1.2	7	150S41-950-500
TOTAL	11504	21.2	9	

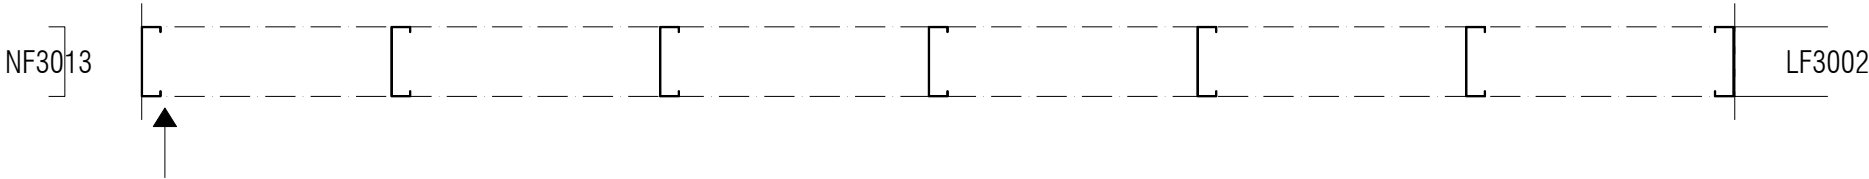

SCAN FOR 3D

NF3014



DELIVERING SINCE 2003

DRAWN: N.N

PH: 02 4860 1416
OFFICE: 02 4860 1400

REV	DATE	REASON
A	15/09/26	IFC — Issued for construction

AUSTRUSS PROJECT NAME

CALDERWOOD

AUSTRUSS ZONE NUMBER

A3

CLIENT NAME

ADCO

PROJECT ADDRESS

179 CALDERWOOD ROAD
CALDERWOOD NSW 2527

AUSTRUSS PROJECT NUMBER

25363

DRAWING NAME

150 - PANELS



DRAWING NUMBER

LGS-A3-200

REV

A

OVERALL HEIGHT = 2550

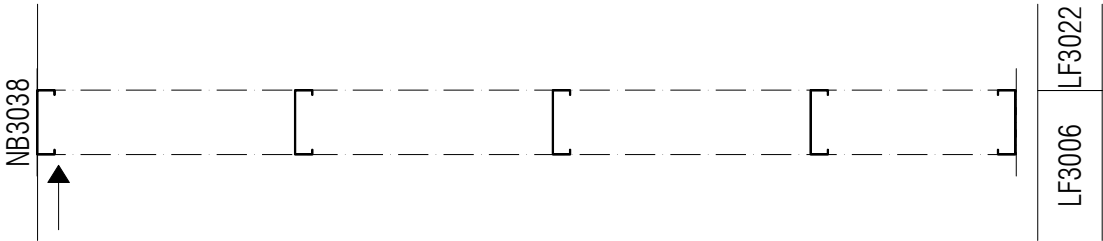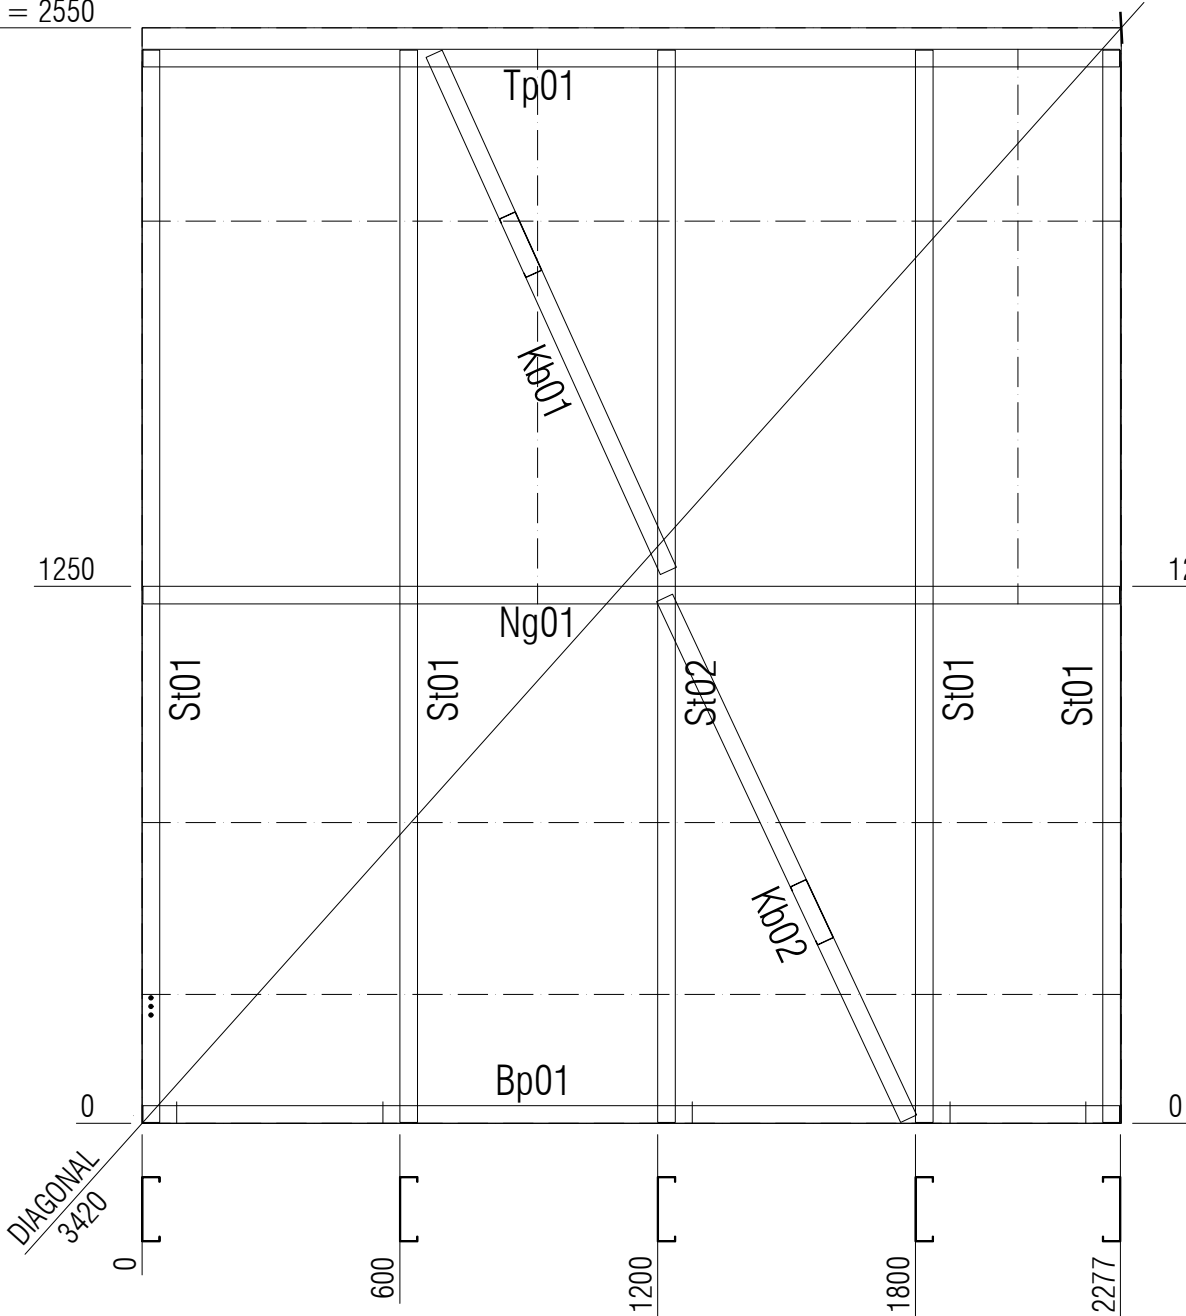

FRAME STICKS				
NAME	LENGTH	WT	QTY	PROFILE
Tp01	2273	4.2	1	150S41-950-500
Bp01	2273	4.2	1	150S41-950-500
St01	2496	4.6	4	150S41-950-500
St02	2496	4.6	1	150S41-950-500
Ng01	2273	4.2	1	150S41-950-500
Kb01	1321	2.4	1	150S41-950-500
Kb02	1339	2.5	1	150S41-950-500
TOTAL	21959	40.4	10	



SCAN FOR 3D

NB3037



DELIVERING SINCE 2003

DRAWN: N.N

PH: 02 4860 1416
OFFICE: 02 4860 1400

REV	DATE	REASON
A	15/09/26	IFC — Issued for construction

AUSTRUSS PROJECT NAME

CALDERWOOD

AUSTRUSS ZONE NUMBER

A3

CLIENT NAME

ADCO

PROJECT ADDRESS

179 CALDERWOOD ROAD
CALDERWOOD NSW 2527

AUSTRUSS PROJECT NUMBER

25363

DRAWING NAME

150 - PANELS


DRAWING NUMBER

LGS-A3-200

REV

A

OVERALL HEIGHT = 2550

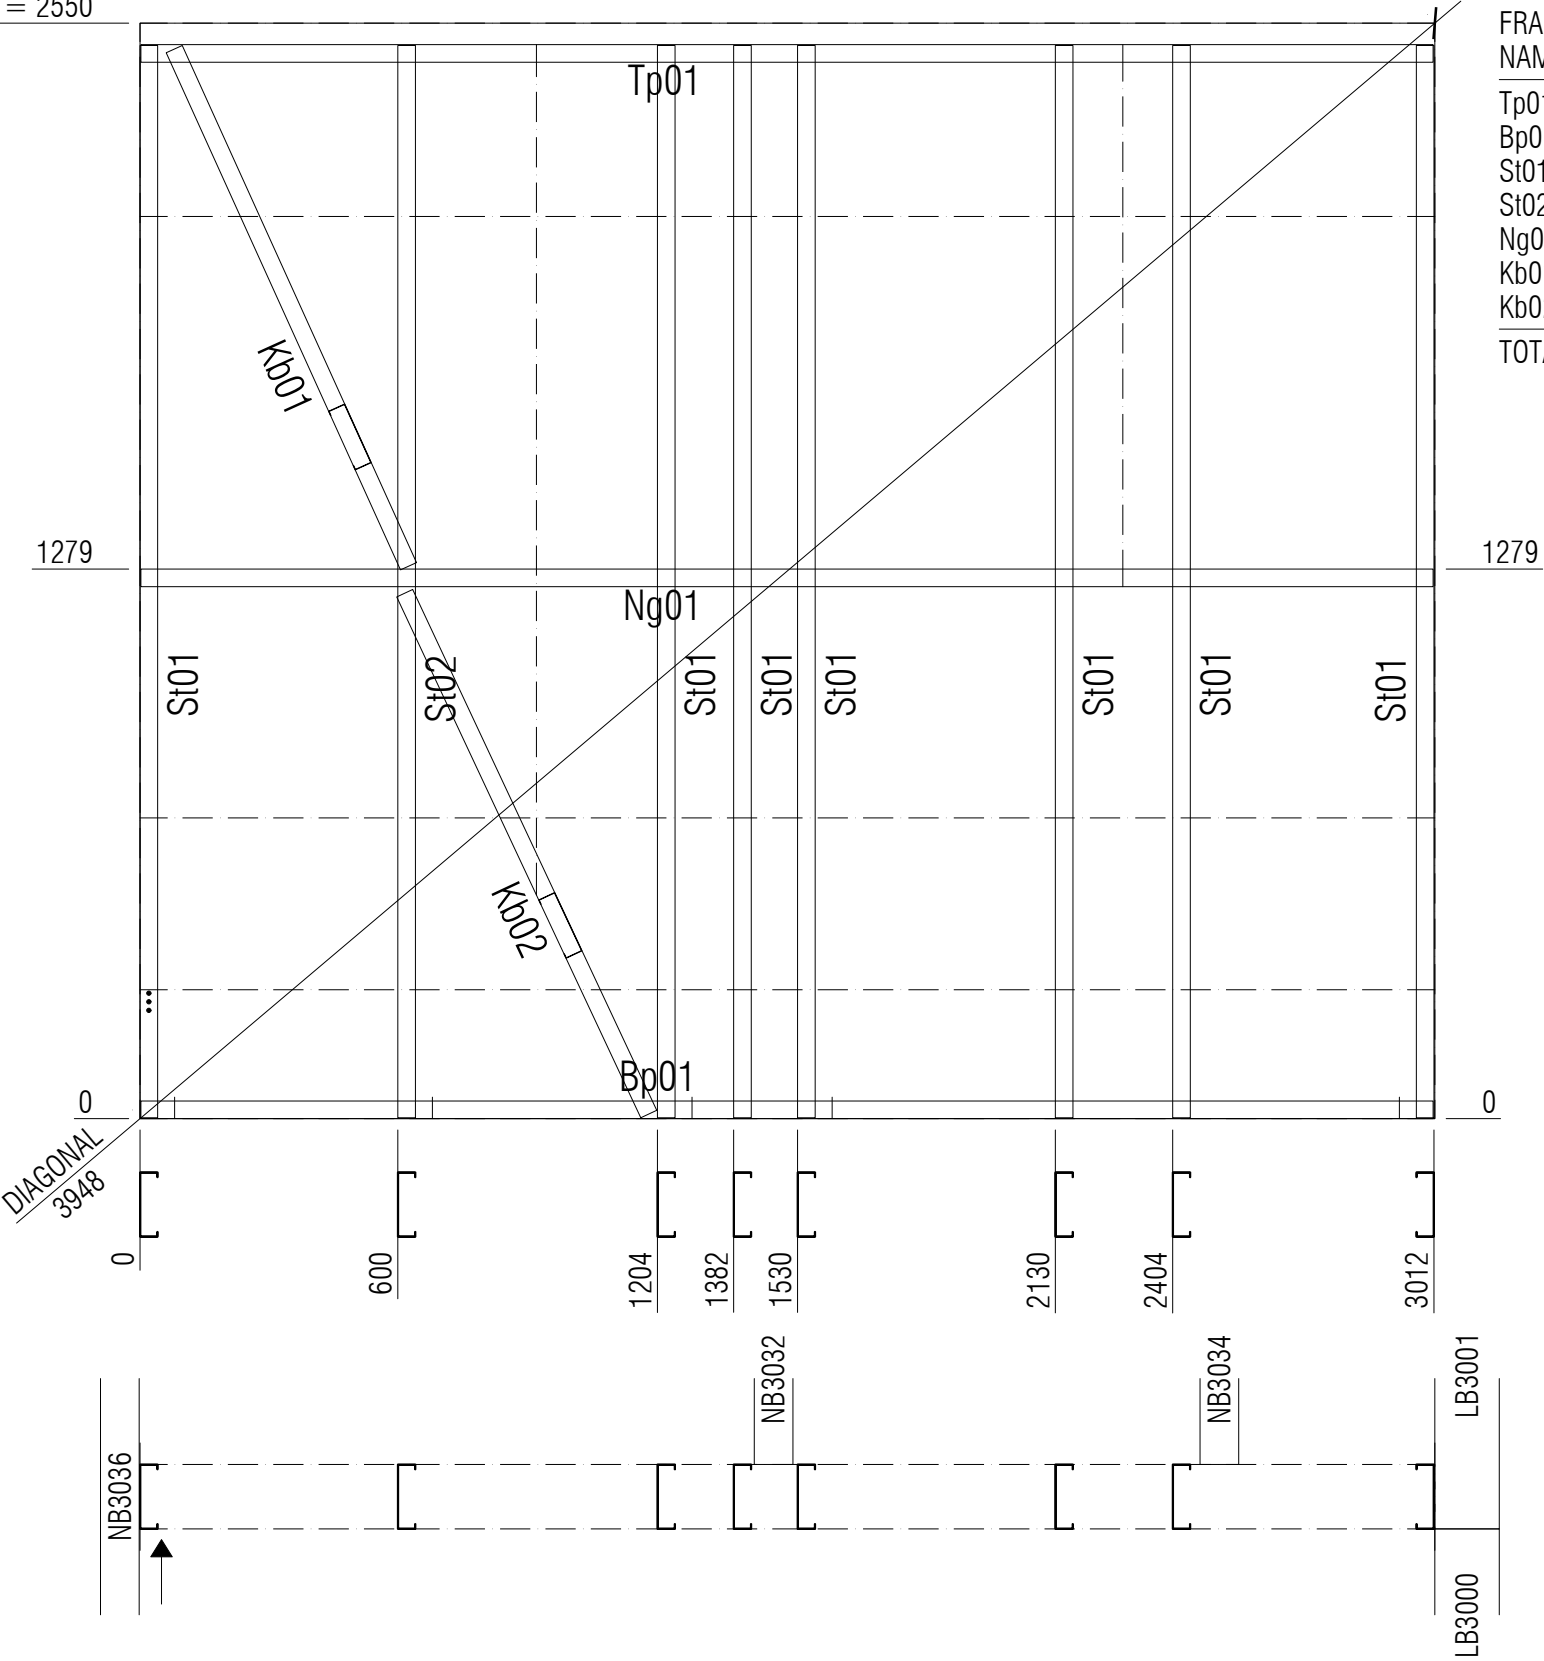

FRAME STICKS NAME	LENGTH	WT	QTY	PROFILE
Tp01	3008	5.5	1	150S41-950-500
Bp01	3008	5.5	1	150S41-950-500
St01	2496	4.6	7	150S41-950-500
St02	2496	4.6	1	150S41-950-500
Ng01	3008	5.5	1	150S41-950-500
Kb01	1321	2.4	1	150S41-950-500
Kb02	1339	2.5	1	150S41-950-500
TOTAL	31651	58.2	13	

NB3035



DRAWN: N.N PH: 02 4860 1416
OFFICE: 02 4860 1400

REV	DATE	REASON
A	15/09/26	IFC — Issued for construction

AUSTRUSS PROJECT NAME
CALDERWOOD
AUSTRUSS ZONE NUMBER
A3
CLIENT NAME
ADCO
PROJECT ADDRESS
**179 CALDERWOOD ROAD
CALDERWOOD NSW 2527**



SCAN FOR 3D

AUSTRUSS PROJECT NUMBER
25363
DRAWING NAME
150 - PANELS
DRAWING NUMBER
LGS-A3-200
REV
A